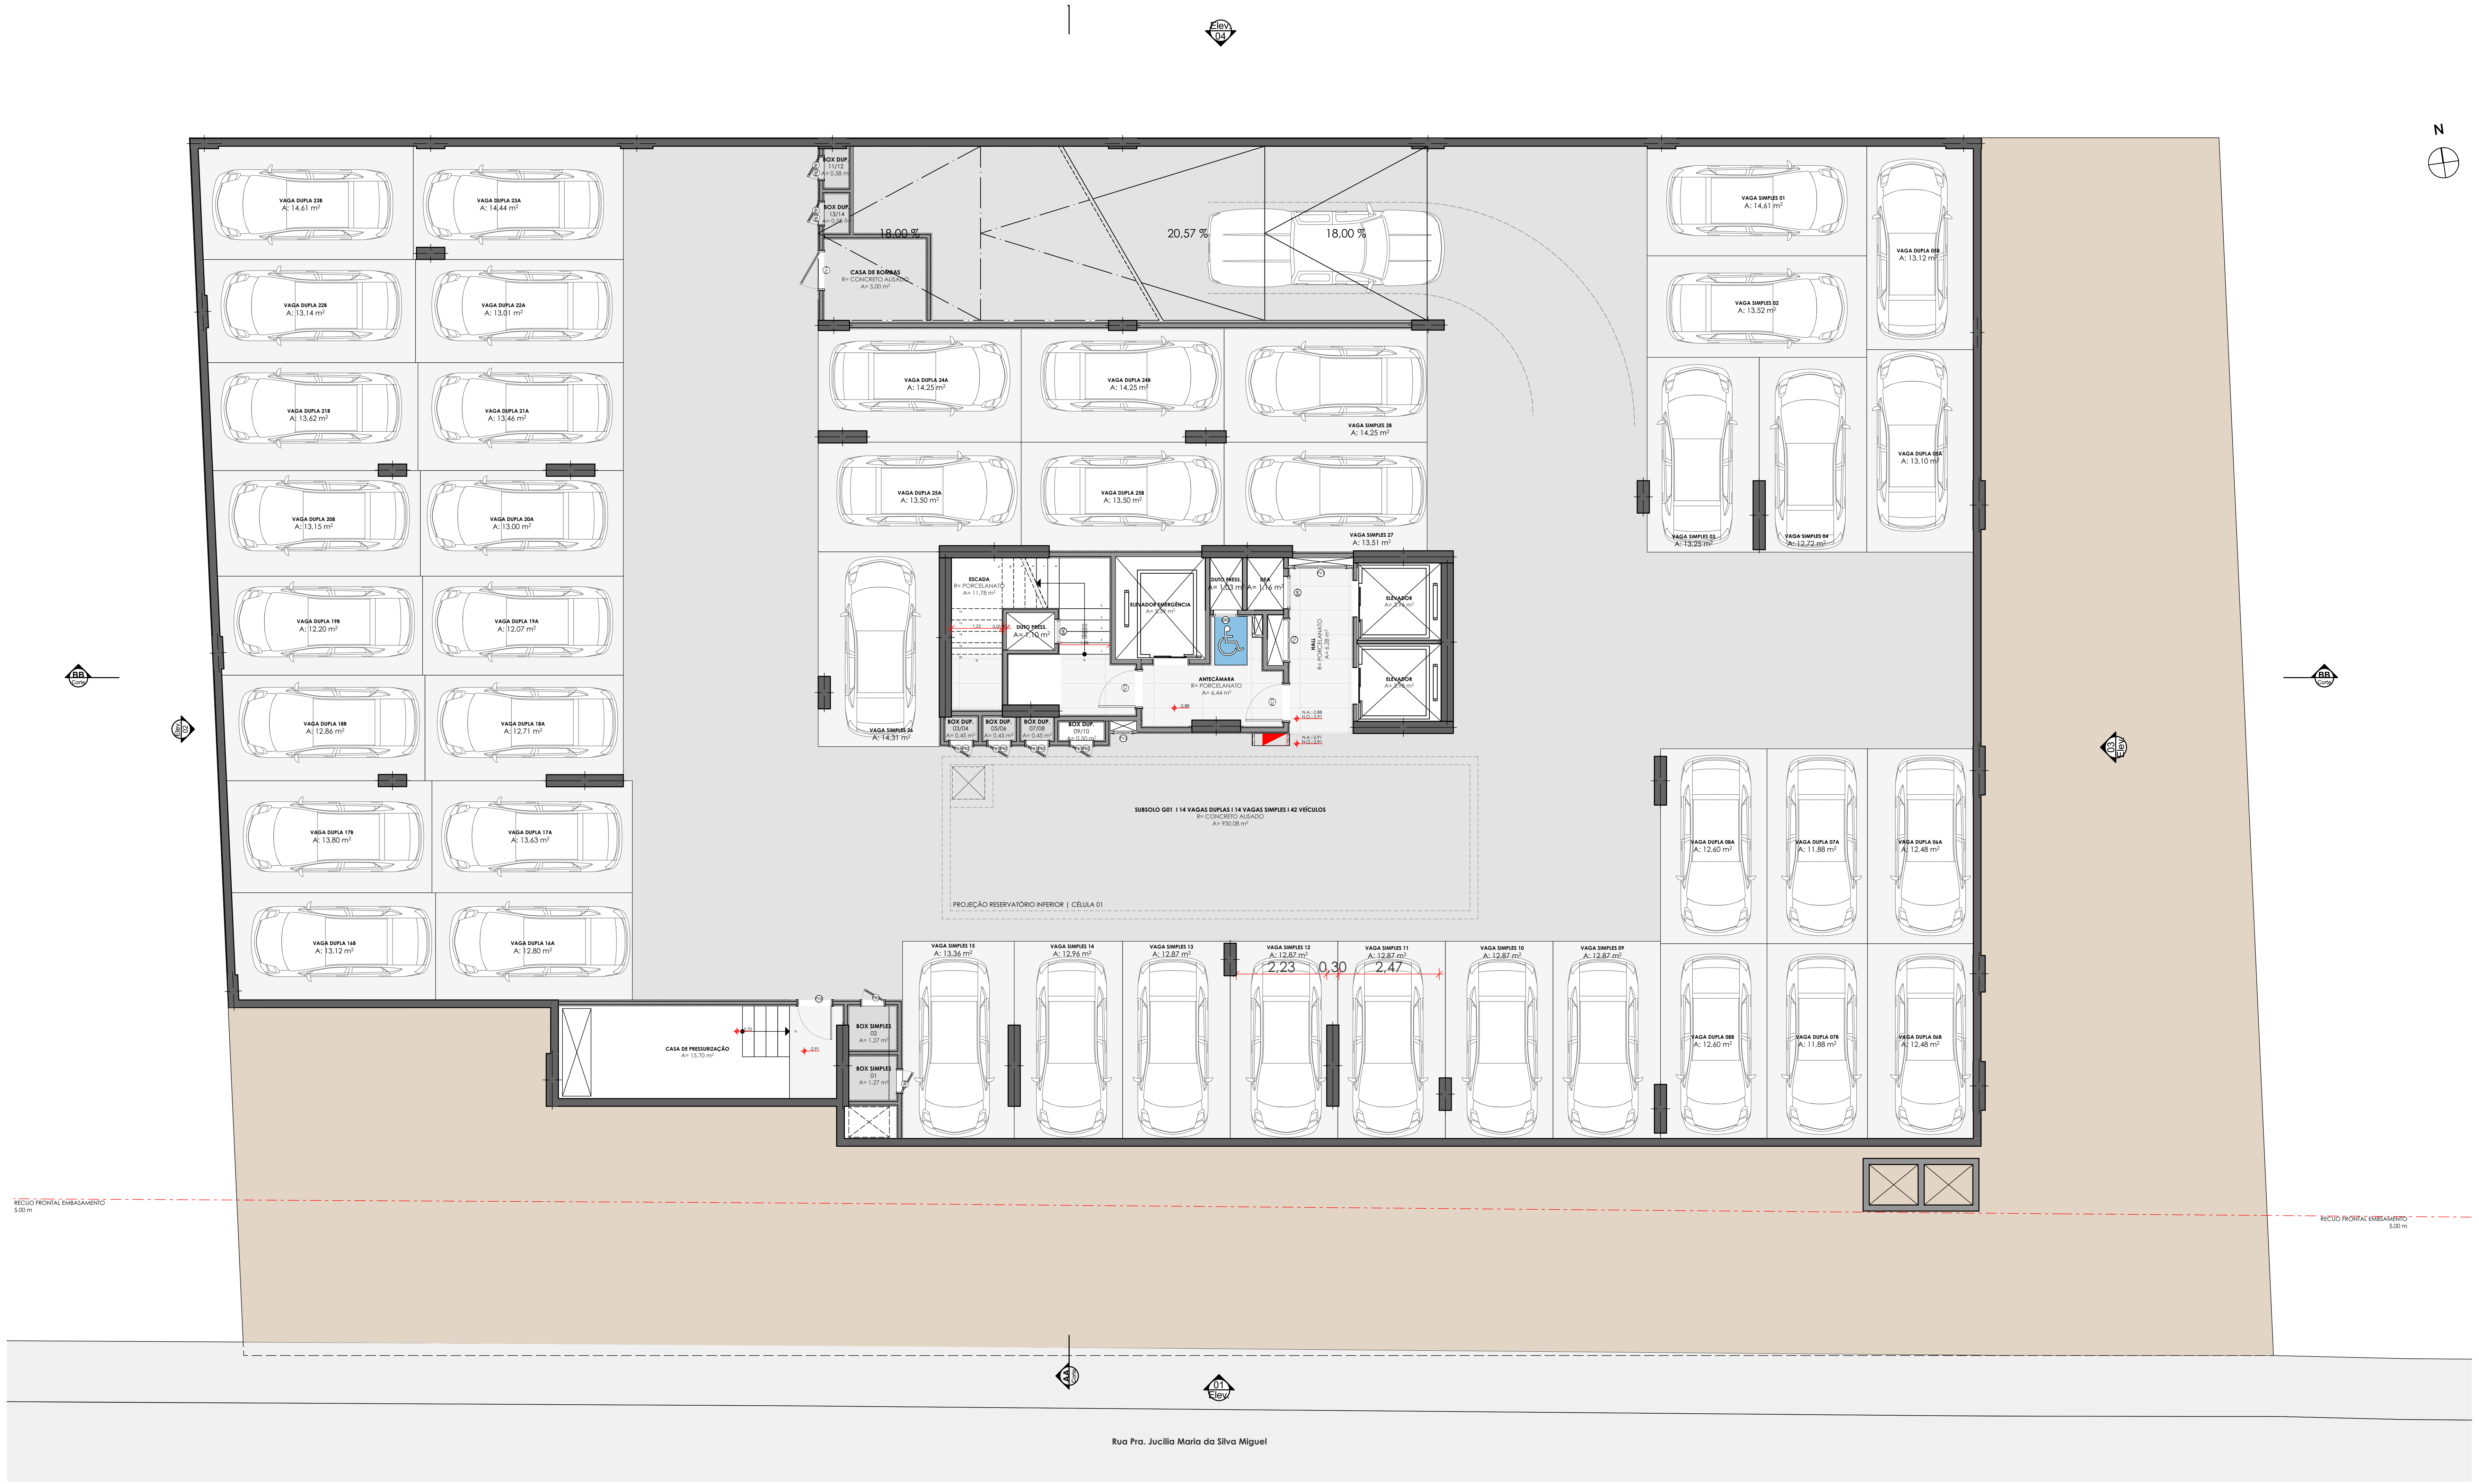
N
18,00 %
20,57 %
18,00 %
ANTECÂMARA
R= PORCELANATO
A= 6,44 m²
ELEVADOR
A= 3,98 m²
BOX DUP. 03/04 A= 0,45 m²
BOX DUP. 05/06 A= 0,45 m²
BOX DUP. 07/08 A= 0,45 m²
BOX DUP. 09/10 A= 0,50 m²
VAGA SIMPLES 26 A: 14,31 m²
SUBSOLO G01 I 14 VAGAS DUPLAS I 14 VAGAS SIMPLES I 42 VEÍCULOS
R= CONCRETO ALISADO
A= 930,08 m²
PROJEÇÃO RESERVATÓRIO INFERIOR | CÉLULA 01
VAGA SIMPLES 15 A: 13,36 m²
VAGA SIMPLES 14 A: 12,96 m²
VAGA SIMPLES 13 A: 12,87 m²
VAGA SIMPLES 12 A: 12,87 m²
VAGA SIMPLES 11 A: 12,87 m²
VAGA SIMPLES 10 A: 12,87 m²
2,23
0,30
2,47
N.A.:-2,88
N.O.:-2,91
N.A.:-2,91
N.O.:-2,91
Rua Pra. Jucilia Maria da Silva Miguel

-1. Subsolo | Garagem 01
1:100

ESQ 03 ESQUADRIAS SUBSOLO | G1

NOME	DIMENSÕES	PEITORIL	TIPO	FOLHA	MATERIAL VISTA	COR	MATERIAL FECHAMENTO	COR FECHAMENTO	QTD
Janela									
GR1	0,80×1,20	1,00	Fixo		Alumínio				1
GR2	0,60×1,20	1,00	Fixo		Alumínio				1
GR2	1,20×1,00	0,45	Fixo		Alumínio				1
GR3	0,60×0,60	1,00	Fixo		Alumínio				1
GR3	1,20×1,00	0,45	Fixo		Alumínio				1
Porta									
P06	0,80×2,10	0,03	Abrir Simples		Madeira				1
PB1	0,60×1,10	0,03	Abrir Simples		Alumínio				3
PB1	0,60×1,10	0,03	Abrir Simples	01	Alumínio	Chumbo	Veneziana	Chumbo	3
PB2	0,60×1,10	1,33	Abrir Simples		Alumínio				6
PB3	0,60×1,80	0,03	Abrir Simples		Alumínio				2
PCF	0,90×2,10	0,00	Tipo P90		Aço Galvanizado				2
PV1	1,20×2,10	0,00	Abrir Simples		Madeira				1
PV2	1,00×2,10	0,00	Abrir Simples		Madeira				1
PV3	0,40×2,10	0,03	Abrir Simples		Madeira				1
PV4	0,90×2,10	0,03	Abrir Simples		Madeira				1

Projeto Pré-executivo

RODRIGO KIRCK ARQUITETURA
Av. Coronel Marcos Konder nº805, Sala 1108, Centro, Itajaí/Santa Catarina CEP 88301-470
Contato | (47) 3349-7161 | contato@rodrigokirck.com.br

DOM | RAYMUNDI BRAVA

ASSUNTO
PE | | Projeto Pré-executivo
Planta Baixa | Pavimento G04, -1. Subsolo | Garagem 01
552_EM_Raymundi_DOM_PE_R01.pln

ARQ RESP Danilo Garcia
DESENHO Thaís Pinheiro

REVISÃO
DATA 14/08/2026

PRANCHA
01

OBRA
DOM | RAYMUNDI BRAVA

LOCAL
R. Pra. Jucilia Maria da Silva Miguel - Itajaí - - Santa Catarina

RESPONSÁVEL TÉCNICO
Danilo dos Santos Garcia
A55244-5

PROPRIETÁRIO
Raymundi Brava RB SPE LTDA
56.344.375/0001-23

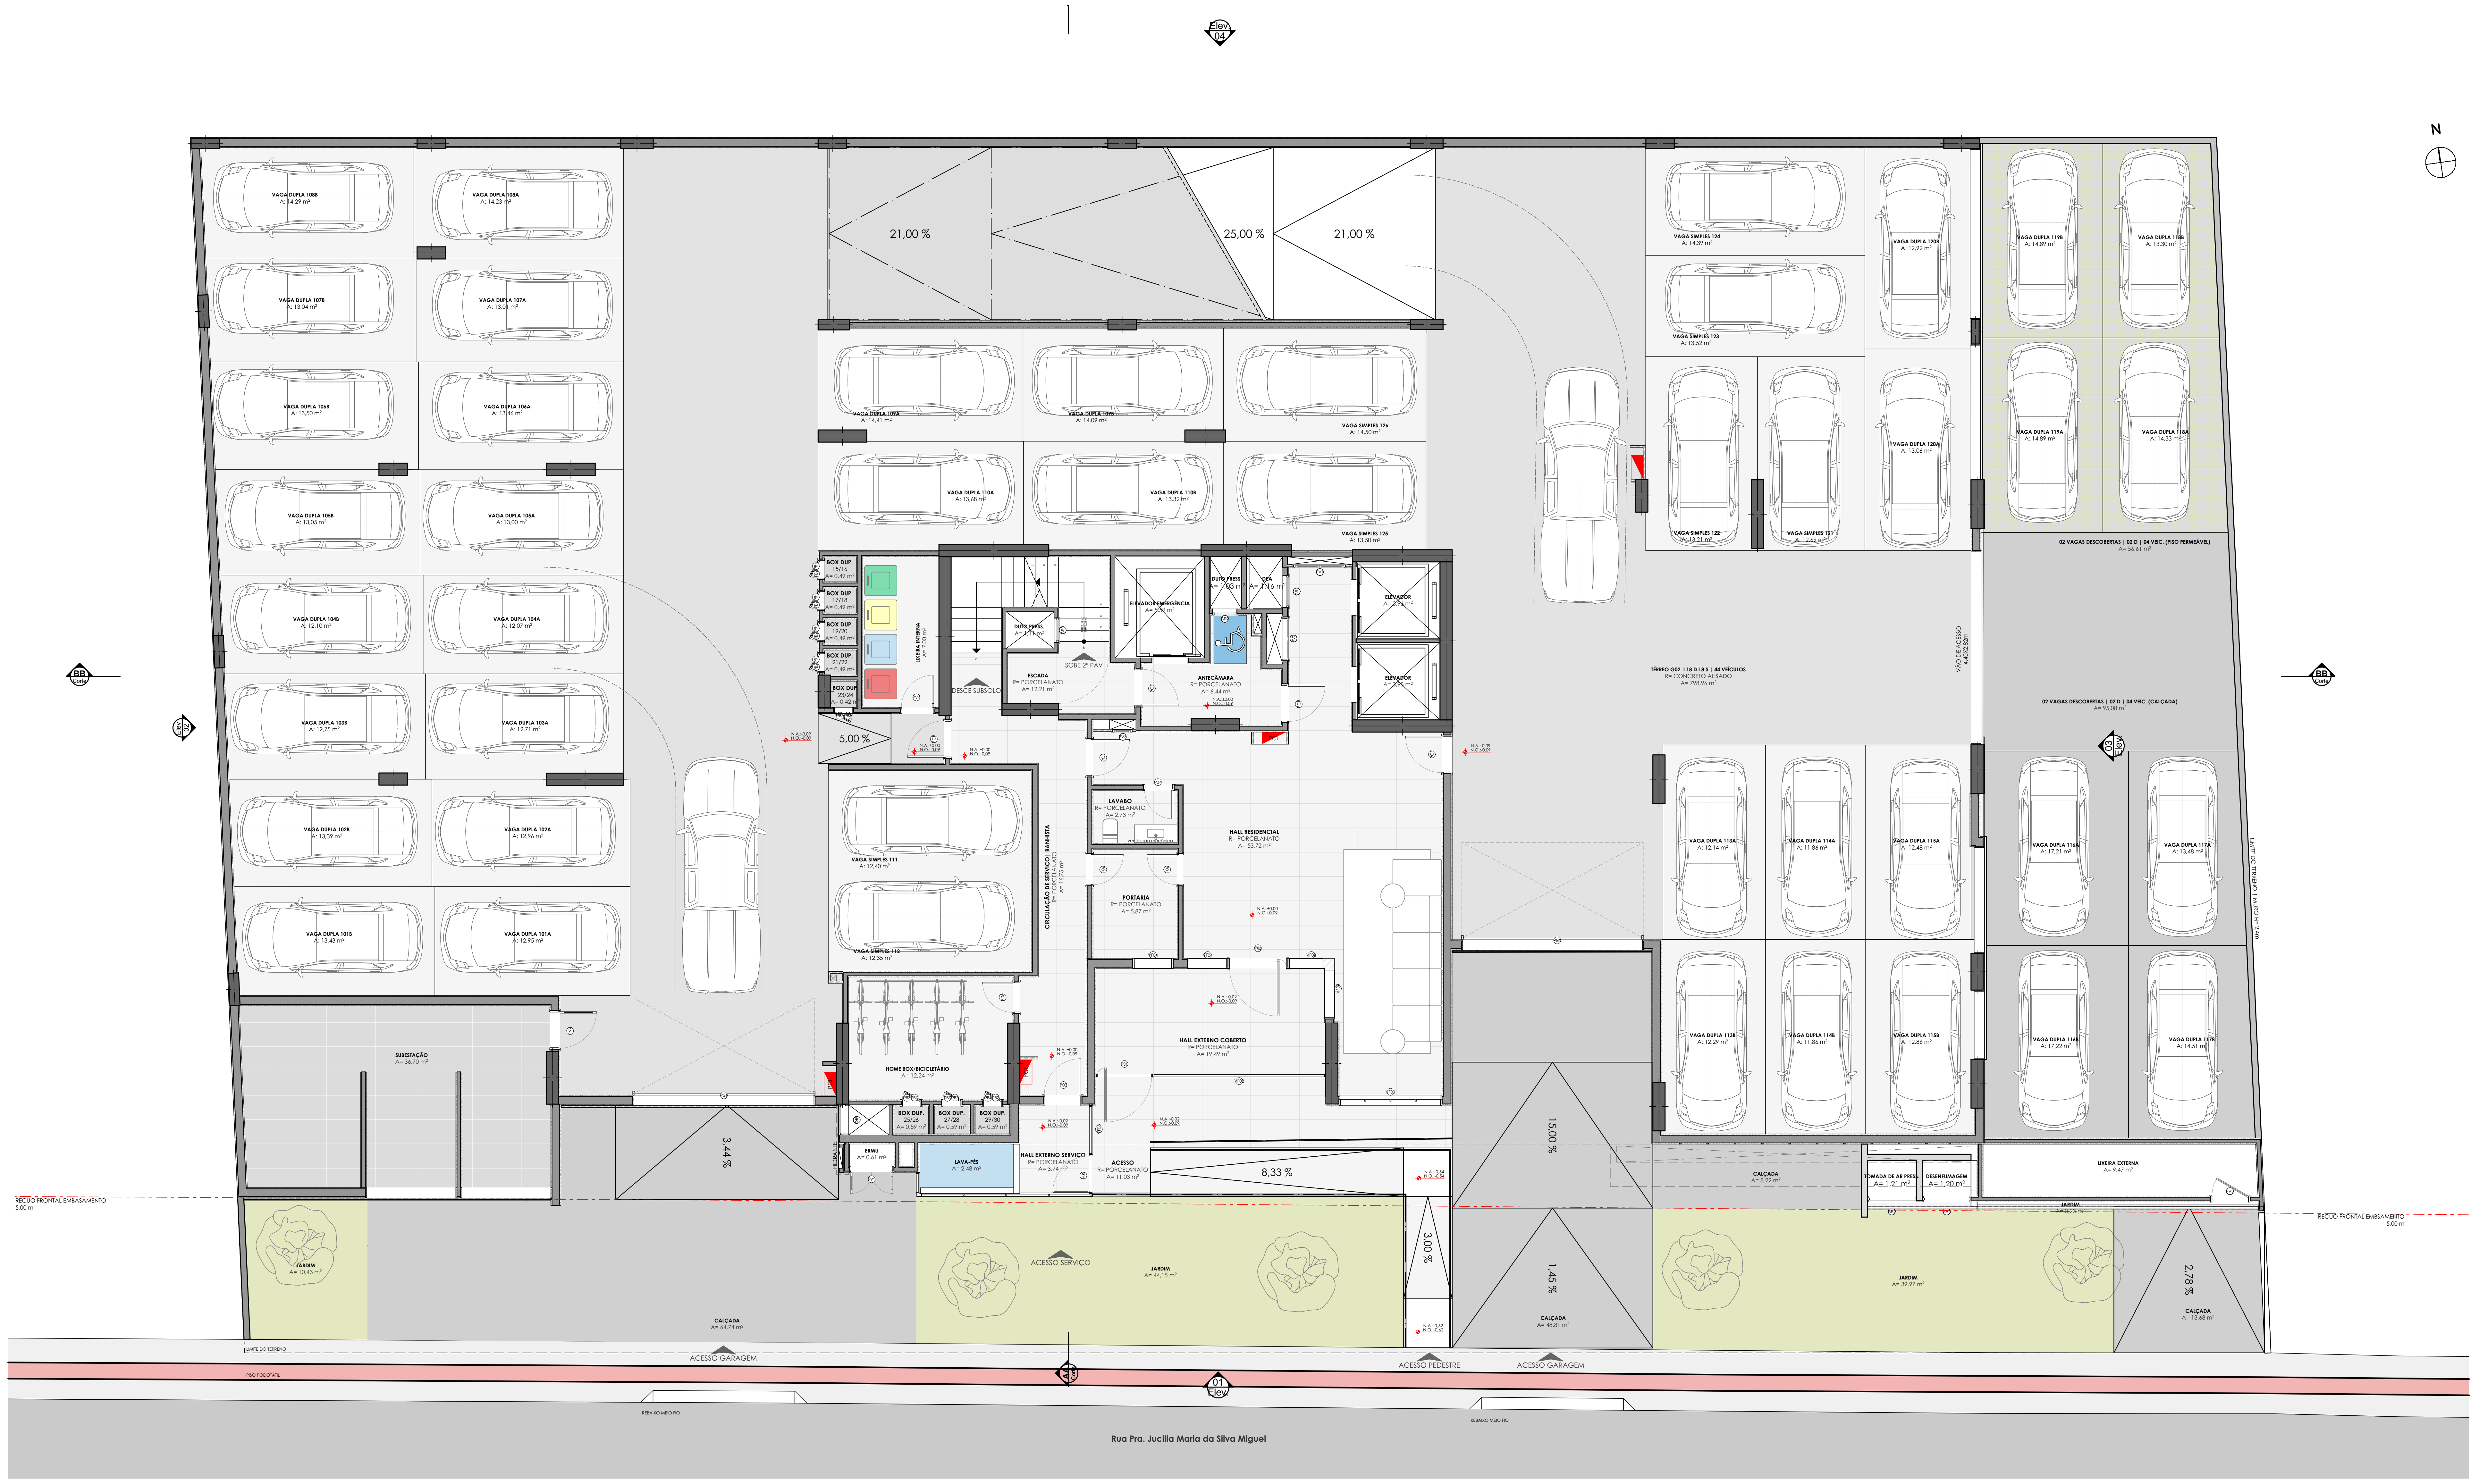

01° Pavimento | Térreo | Garagem 02

1:100

ESQ 01 ESQUADRIAS TÉRREO

NOME	DIMENSÕES	PEITORIL	TIPO	FOLHA	MATERIAL VISTA	COR	MATERIAL FECHAMENTO	COR FECHAMENTO	QTD
Janela									
GR1	0,80×1,20	1,07	Fixo		Alumínio				1
GR2	0,60×1,20	1,07	Fixo		Alumínio				1
GR2	0,75×2,40	0,07	Fixo		Alumínio				1
GR3	0,60×0,60	1,07	Fixo		Alumínio				1
VF01	2,54×2,40	0,07	Fixo	04	Alumínio	Chumbo	Vidro	Transparente	1
VF03	4,27×2,40	0,07	Fixo		Alumínio				1
VF04	1,00×2,40	0,07	Fixo		Alumínio				2
VF04	1,15×2,40	0,07	Fixo		Alumínio				1
VF04	1,50×2,40	0,07	Fixo		Alumínio				1
VF08	1,22×2,40	0,00	Fixo	03	Alumínio	Chumbo	Vidro	Transparente	1
Porta									
P01	1,40×2,40	0,07	Pivotante	01	Alumínio	Chumbo	Vidro	Transparente	1
P02	1,40×2,36	0,07	Pivotante	01	Alumínio	Chumbo	Vidro	Transparente	1
P03	0,90×2,40	0,07	Abrir Simples	01	Madeira	Branco	Madeira	Branco	1
P04	0,70×2,10	0,07	Abrir Simples	01	Madeira	Branco	Madeira	Branco	1
P05	0,90×2,37	0,00	Abrir Simples		Alumínio				1
P06	0,80×2,10	0,07	Abrir Simples		Madeira				3
PB1	0,50×1,10	0,07	Abrir Simples		Alumínio				5
PB2	0,50×1,10	0,07	Abrir Simples		Alumínio				3
PB2	0,50×1,10	1,37	Abrir Simples		Alumínio				5
PB3	0,50×1,10	1,37	Abrir Simples		Alumínio				2
PB4	0,50×1,10	1,37	Abrir Simples		Alumínio				1
PCF	0,90×2,10	0,07	Abrir Simples		Madeira				1
PCF	0,90×2,10	0,07	Abrir Simples	01	Madeira	Branco	Madeira	Branco	2
PCF	0,90×2,10	0,07	Tipo P90		Aço Galvanizado				2
PG1	4,50×2,40	0,00	Projetante	01	Alumínio	Chumbo	Veneziana	Chumbo	2
PV1	1,04×1,70	0,02	Abrir Simples		Alumínio				1
PV1	1,20×2,10	0,07	Abrir Simples		Madeira				1
PV2	0,90×2,10	0,00	Abrir Simples		Madeira				1
PV2	1,00×2,10	0,07	Abrir Simples		Madeira				1
PV3	0,40×2,10	0,07	Abrir Simples		Madeira				1
PV4	0,80×2,10	0,07	Abrir Simples		Madeira				1
PV4	0,90×2,10	0,07	Abrir Simples		Madeira				1

Projeto Pré-executivo

RODRIGO KIRCK ARQUITETURA

Av. Coronel Marcos Konder nº805, Sala 1108, Centro, Itajaí/Santa Catarina CEP 88301-470
Contato | (47) 3349-7161 | contato@rodrigokirck.com.br

DOM | RAYMUNDI BRAVA

ASSUNTO
PE | | Projeto Pré-executivo
Planta Baixa | Pavimento G04, 01° Pavimento | Térreo | Garagem 02
552_EM_Raymundi_DOM_PE_R01.pln

ARQ RESP: Danilo Garcia
DESENHO: Thaís Pinheiro
REVISÃO
DATA: 14/08/2026

PRANCHA
02

OBRA
DOM | RAYMUNDI BRAVA

LOCAL
R. Pra. Jucilia Maria da Silva Miguel - Itajaí - - Santa Catarina

RESPONSÁVEL TÉCNICO
Danilo dos Santos Garcia
A55244-5

PROPRIETÁRIO
Raymundi Brava RB SPE LTDA
56.344.375/0001-23

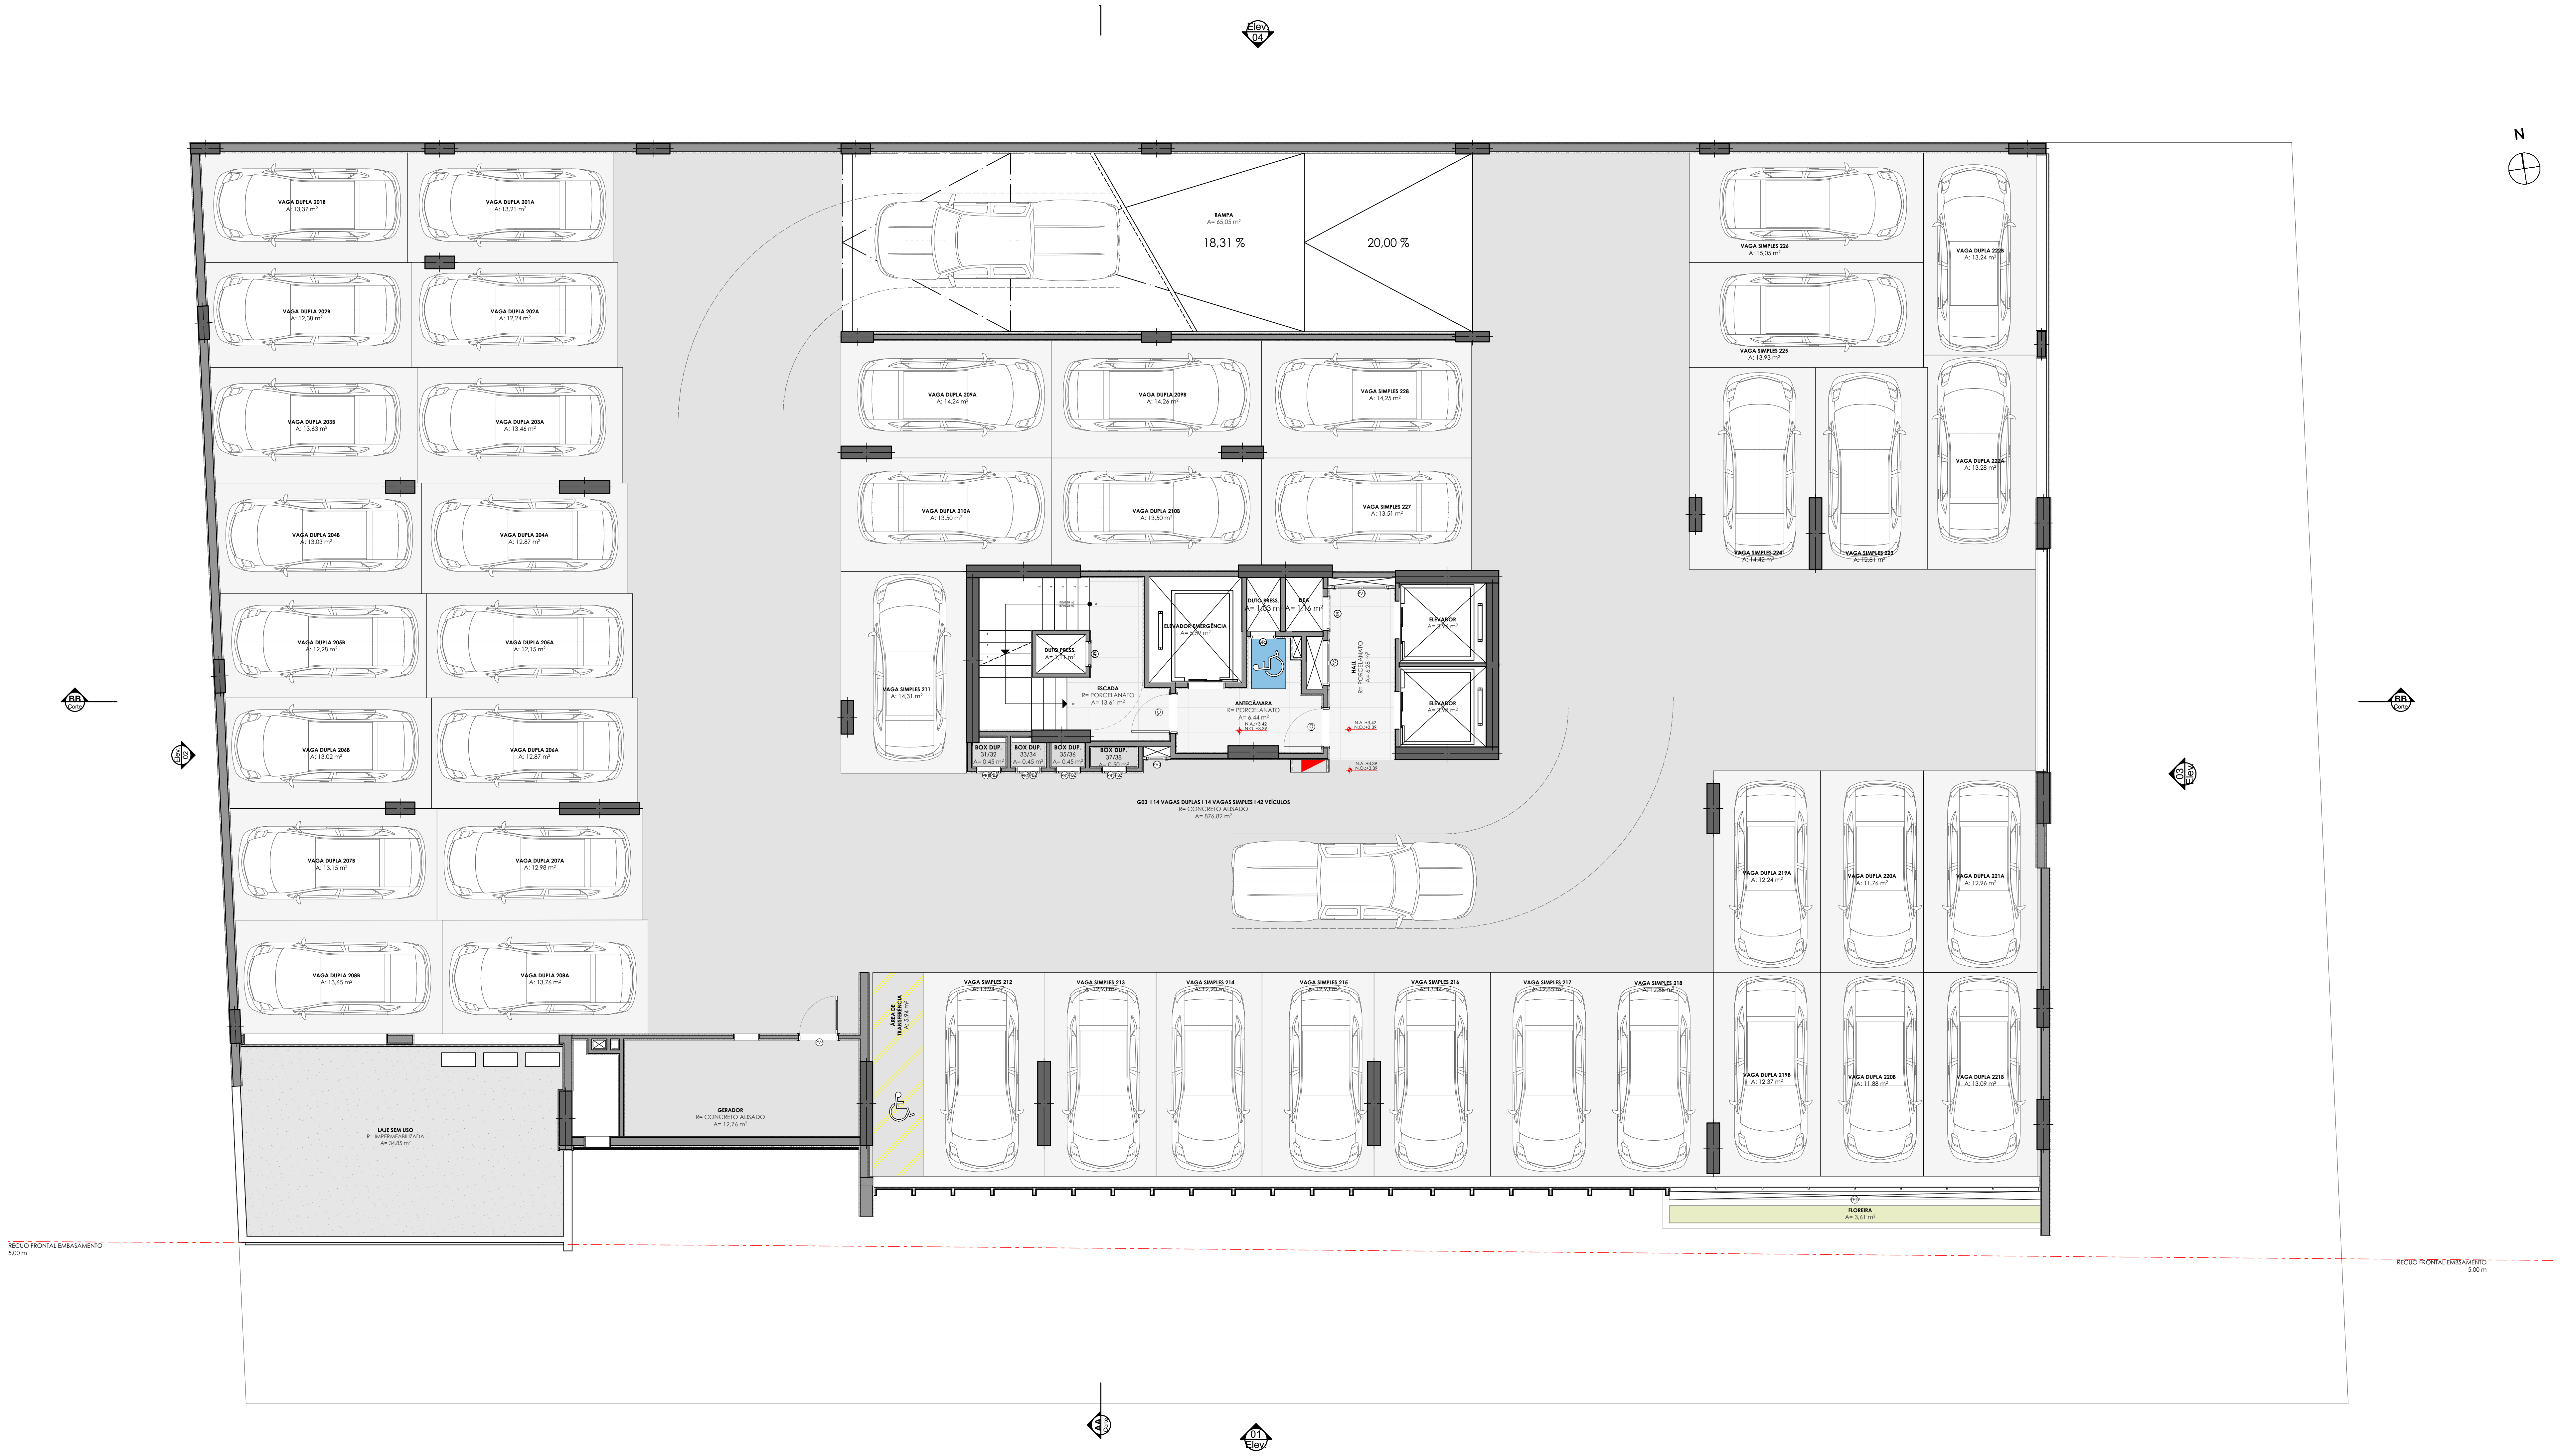
N
RAMPA
18,31 %
20,00 %
VAGA DUPLA 210A
A: 13,50 m²
VAGA DUPLA 210B
A: 13,50 m²
VAGA SIMPLES 227
A: 13,51 m²
VAGA SIMPLES 211
A: 14,31 m²
ESCADA
R= PORCELANATO
A= 13,61 m²
DUTO PRESS.
A= 1,11 m²
ELEVADOR EMERGÊNCIA
A= 5,59 m²
DUTO PRESS.
A= 1,03 m²
DEA
A= 1,16 m²
ANTECÂMARA
R= PORCELANATO
A= 6,44 m²
HALL
R= PORCELANATO
A= 6,28 m²
ELEVADOR
A= 3,96 m²
ELEVADOR
A= 3,98 m²
BOX DUP. 31/32
A= 0,45 m²
BOX DUP. 33/34
A= 0,45 m²
BOX DUP. 35/36
A= 0,45 m²
BOX DUP. 37/38
A= 0,50 m²
N.A.:+3,42
N.O.:+3,39
N.A.:+3,39
N.O.:+3,39
G03 I 14 VAGAS DUPLAS I 14 VAGAS SIMPLES I 42 VEÍCULOS
R= CONCRETO ALISADO
A= 876,82 m²
GERADOR
LAJE SEM USO
FLOREIRA
RECUO FRONTAL EMBASAMENTO

02º Pavimento | Garagem 03
1:100

ESQ 02 ESQUADRIAS G3									
NOME	DIMENSÕES	PEITORIL	TIPO	FOLHA	MATERIAL VISTA	COR	MATERIAL FECHAMENTO	COR FECHAMENTO	QTD
Janela									
GR1	0,80×1,20	1,00	Fixo		Alumínio				1
GR2	0,60×1,20	1,00	Fixo		Alumínio				1
GR3	0,60×0,60	1,07	Fixo		Alumínio				1
VF12	8,83×2,88	0,00	Fixo	08	Alumínio	Chumbo	Vidro	Trasnparente	1
Porta									
PB1	0,60×1,10	0,00	Abrir Simples		Alumínio				1
PB1	0,60×1,10	0,00	Abrir Simples	01	Alumínio	Chumbo	Veneziana	Chumbo	3
PB2	0,60×1,10	1,30	Abrir Simples		Alumínio				4
PCF	0,90×2,10	0,00	Tipo P90		Aço Galvanizado				2
PV1	1,20×2,10	0,00	Abrir Simples		Madeira				1
PV2	0,40×2,10	0,00	Abrir Simples		Madeira				1
PV2	1,00×2,10	0,00	Abrir Simples		Madeira				1
PV4	0,90×2,10	0,00	Abrir Simples		Madeira				1

Projeto Pré-executivo

RODRIGO KIRCK ARQUITETURA
Av. Coronel Marcos Konder nº805, Sala 1108, Centro, Itajaí/Santa Catarina CEP 88301-470
Contato | (47) 3349-7161 | contato@rodrigokirck.com.br

DOM | RAYMUNDI BRAVA

ASSUNTO
PE | | Projeto Pré-executivo
02º Pavimento | Garagem 03, Planta Baixa | Pavimento G04
552_EM_Raymundi_DOM_PE_R01.pln

ARQ RESP Danilo Garcia
DESENHO Thaís Pinheiro

REVISÃO
DATA 14/08/2026

PRANCHA
03

OBRA
DOM | RAYMUNDI BRAVA

LOCAL
R. Pra. Jucilia Maria da Silva Miguel - Itajaí - - Santa Catarina

RESPONSÁVEL TÉCNICO
Danilo dos Santos Garcia
A55244-5

PROPRIETÁRIO
Raymundi Brava RB SPE LTDA
56.344.375/0001-23

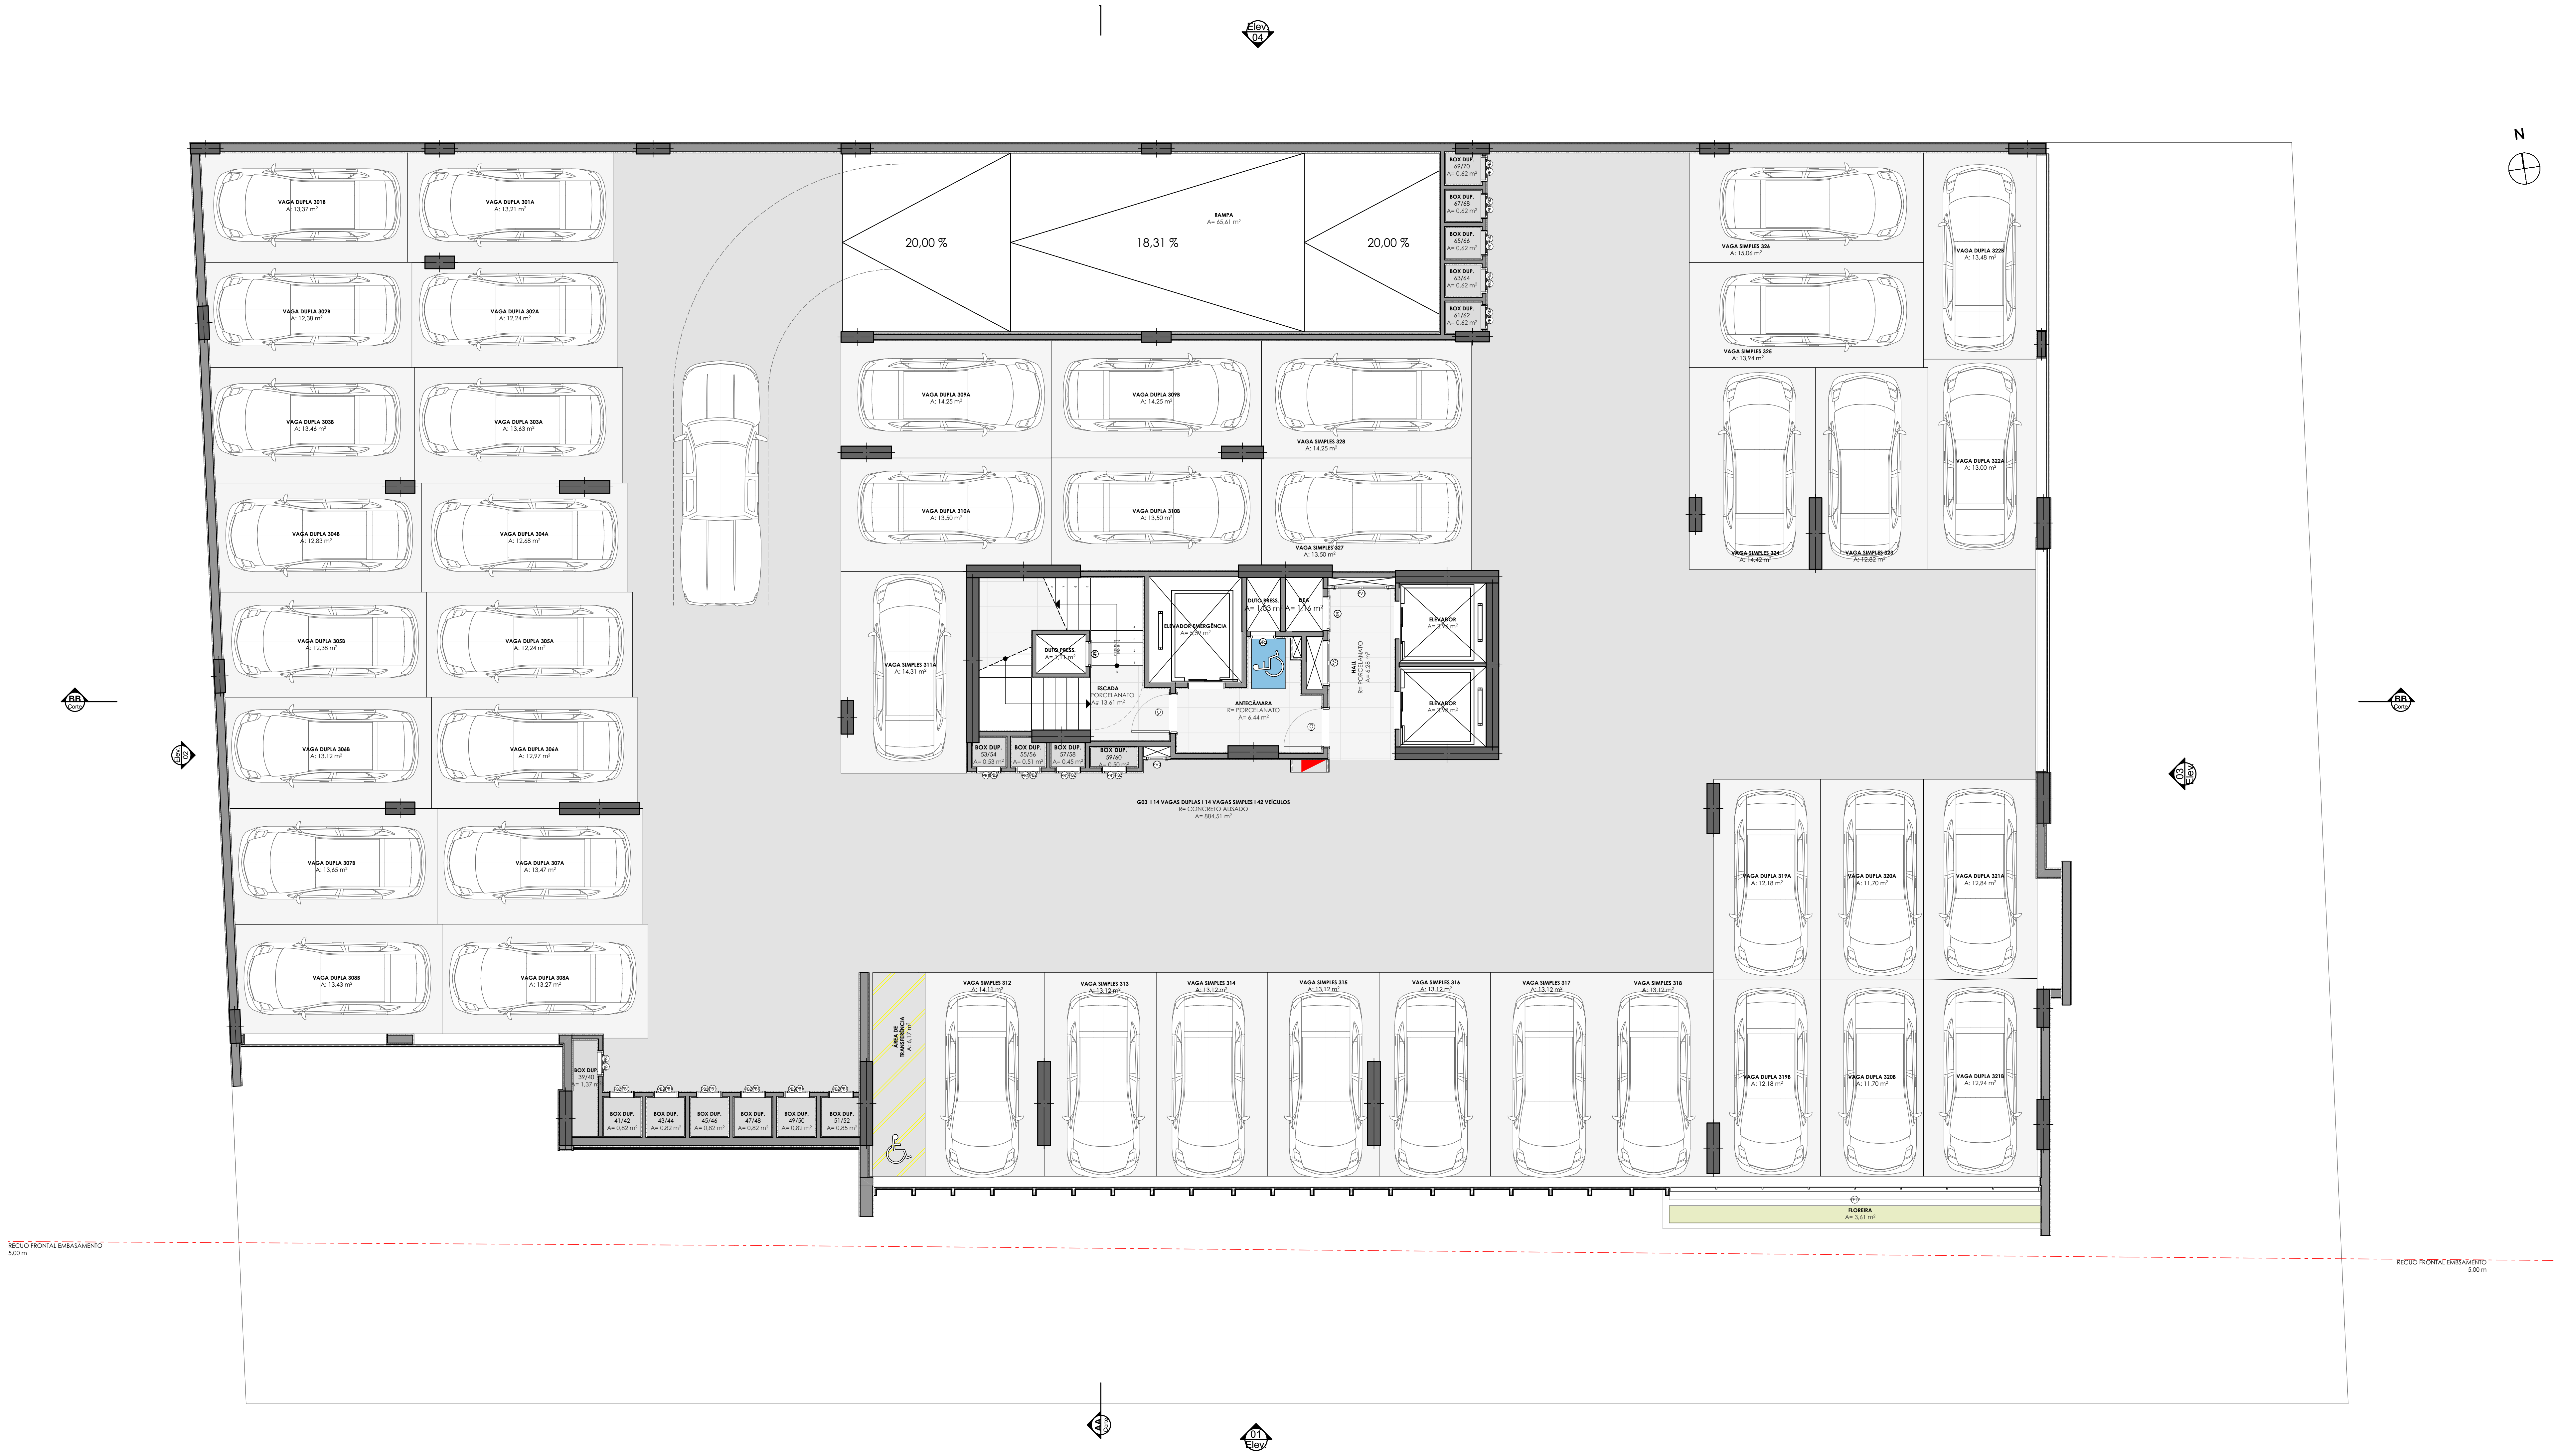
N
RAMPA
20,00 %
18,31 %
20,00 %
ESCADA
PORCELANATO
A= 13,61 m²
DUTO PRESS.
A= 1,11 m²
ANTECÂMARA
R= PORCELANATO
A= 6,44 m²
HALL
R= PORCELANATO
A= 6,28 m²
ELEVADOR
A= 3,98 m²
BOX DUP.
53/54
A= 0,53 m²
BOX DUP.
55/56
A= 0,51 m²
BOX DUP.
57/58
A= 0,45 m²
BOX DUP.
59/60
A= 0,50 m²
G03 I 14 VAGAS DUPLAS I 14 VAGAS SIMPLES I 42 VEÍCULOS
R= CONCRETO ALISADO
A= 884,51 m²
FLOREIRA
RECUO FRONTAL EMBASAMENTO

03º Pavimento | Garagem 04
1:100

ESQ 04 ESQUADRIAS G04

NOME	DIMENSÕES	PEITORIL	TIPO	FOLHA	MATERIAL VISTA	COR	MATERIAL FECHAMENTO	COR FECHAMENTO	QTD
Janela									
GR1	0,80×1,20	1,00	Fixo		Alumínio				1
GR2	0,60×1,20	1,00	Fixo		Alumínio				1
GR3	0,60×0,60	1,07	Fixo		Alumínio				1
VF12	8,83×2,40	0,00	Fixo	08	Alumínio	Chumbo	Vidro	Trasnparente	1
Porta									
PB1	0,60×1,10	0,00	Abrir Simples		Alumínio				13
PB1	0,60×1,10	0,00	Abrir Simples	01	Alumínio	Chumbo	Veneziana	Chumbo	3
PB2	0,60×1,10	1,30	Abrir Simples		Alumínio				16
PCF	0,90×2,10	0,00	Tipo P90		Aço Galvanizado				2
PV1	1,20×2,10	0,00	Abrir Simples		Madeira				1
PV2	0,40×2,10	0,00	Abrir Simples		Madeira				1
PV2	1,00×2,10	0,00	Abrir Simples		Madeira				1

Projeto Pré-executivo

RODRIGO KIRCK ARQUITETURA
Av. Coronel Marcos Konder nº805, Sala 1108, Centro, Itajaí/Santa Catarina CEP 88301-470
Contato | (47) 3349-7161 | contato@rodrigokirck.com.br

DOM | RAYMUNDI BRAVA

ASSUNTO
PE | | Projeto Pré-executivo
03º Pavimento | Garagem 04, Planta Baixa | Pavimento G04
552_EM_Raymundi_DOM_PE_R01.pln

ARQ RESP Danilo Garcia
DESENHO Thaís Pinheiro
REVISÃO
DATA 14/08/2026

PRANCHA
04

OBRA
DOM | RAYMUNDI BRAVA

LOCAL
R. Pra. Jucilia Maria da Silva Miguel - Itajaí - - Santa Catarina

RESPONSÁVEL TÉCNICO

PROPRIETÁRIO

Danilo dos Santos Garcia
A55244-5

Raymundi Brava RB SPE LTDA
56.344.375/0001-23

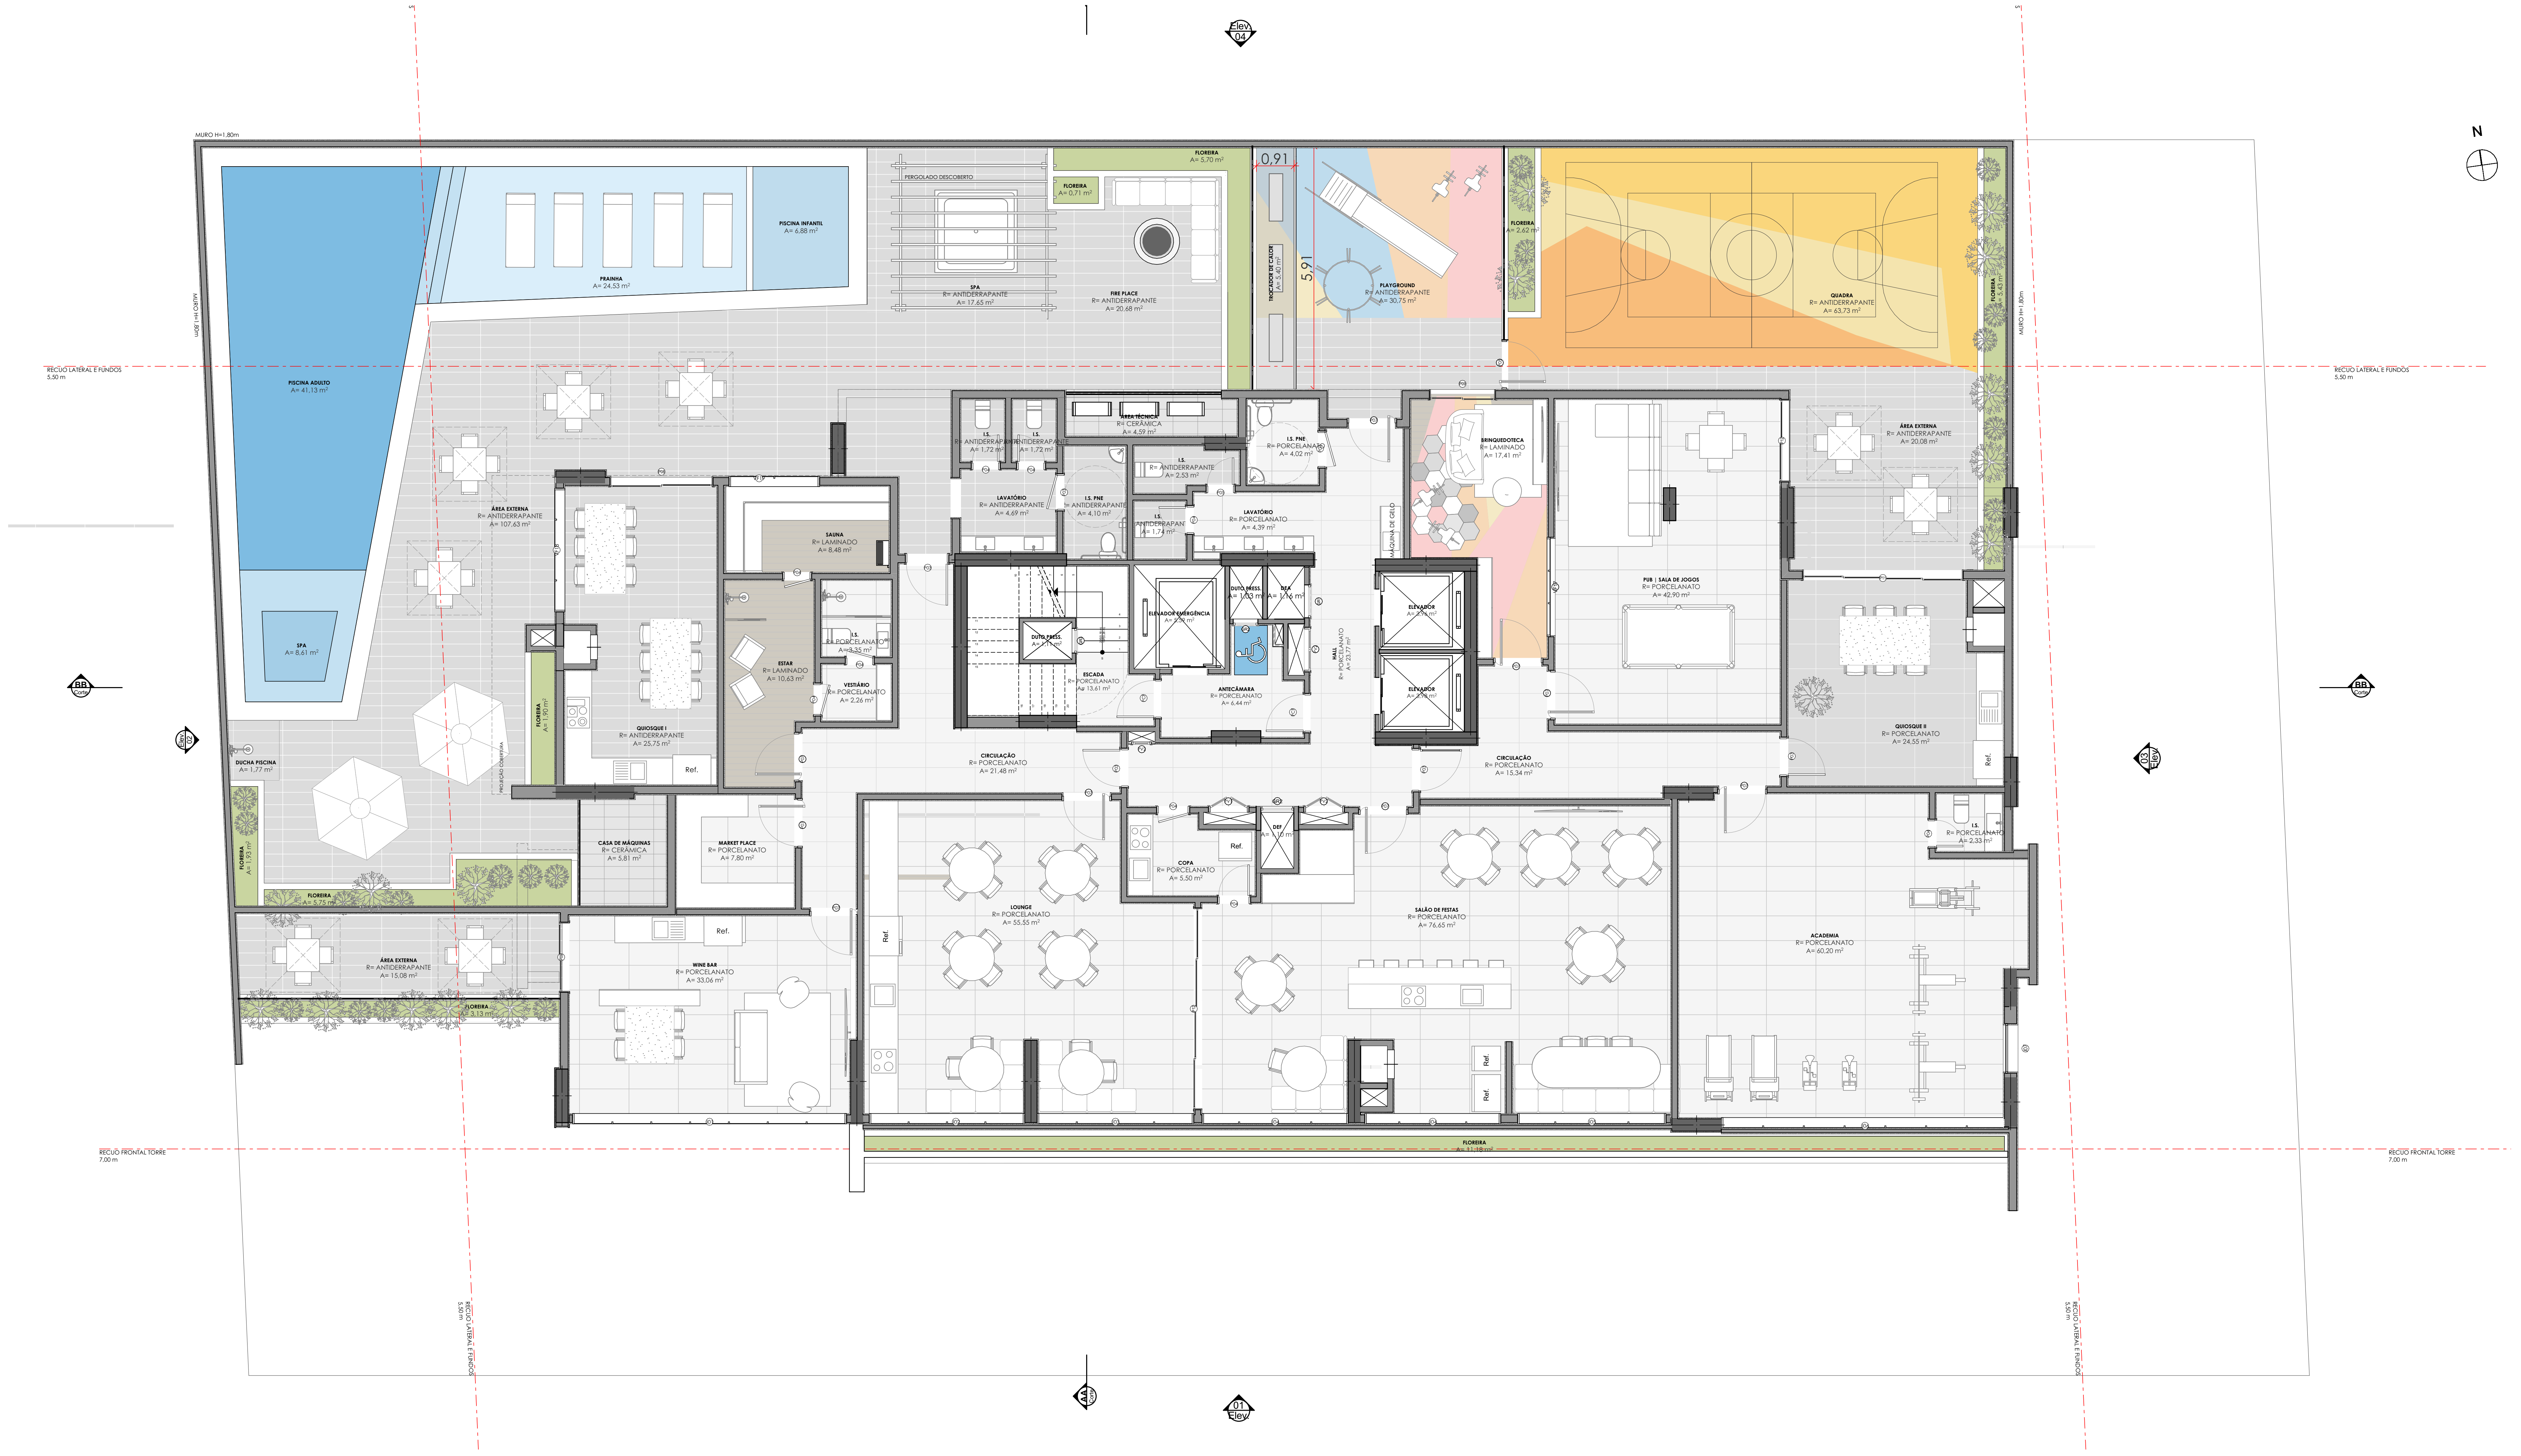
MURO H=1,80m
PISCINA ADULTO
A= 41,13 m²
PRAINHA
A= 24,53 m²
PISCINA INFANTIL
A= 6,88 m²
SPA
A= 8,61 m²
PERGOLADO DESCOBERTO
SPA
R= ANTIDERRAPANTE
A= 17,65 m²
FLOREIRA
A= 0,71 m²
FLOREIRA
A= 5,70 m²
FIRE PLACE
R= ANTIDERRAPANTE
A= 20,68 m²
0,91
5,91
TROCADOR DE CALOR
A= 5,40 m²
PLAYGROUND
R= ANTIDERRAPANTE
A= 30,75 m²
FLOREIRA
A= 2,62 m²
QUADRA
R= ANTIDERRAPANTE
A= 63,73 m²
FLOREIRA
A= 5,43 m²
ÁREA EXTERNA
R= ANTIDERRAPANTE
A= 107,63 m²
DUCHA PISCINA
A= 1,77 m²
PROJEÇÃO COBERTURA
FLOREIRA
A= 1,90 m²
QUIOSQUE I
R= ANTIDERRAPANTE
A= 25,75 m²
Ref.
SAUNA
R= LAMINADO
A= 8,48 m²
ESTAR
R= LAMINADO
A= 10,63 m²
I.S.
R= PORCELANATO
A= 3,35 m²
VESTIÁRIO
R= PORCELANATO
A= 2,26 m²
I.S.
R= ANTIDERRAPANTE
A= 1,72 m²
I.S.
R= ANTIDERRAPANTE
A= 1,72 m²
LAVATÓRIO
R= ANTIDERRAPANTE
A= 4,69 m²
I.S. PNE
R= ANTIDERRAPANTE
A= 4,10 m²
ÁREA TÉCNICA
R= CERÂMICA
A= 4,59 m²
I.S.
R= ANTIDERRAPANTE
A= 2,53 m²
I.S.
R= ANTIDERRAPANTE
A= 1,74 m²
I.S. PNE
R= PORCELANATO
A= 4,02 m²
LAVATÓRIO
R= PORCELANATO
A= 4,39 m²
MÁQUINA DE GELO
DUTO PRESS.
A= 1,11 m²
ESCADA
R= PORCELANATO
A= 13,61 m²
ELEVADOR EMERGÊNCIA
A= 5,59 m²
DUTO PRESS.
A= 1,03 m²
DEA
A= 1,16 m²
ANTECÂMARA
R= PORCELANATO
A= 6,44 m²
HALL
R= PORCELANATO
A= 23,77 m²
ELEVADOR
A= 3,96 m²
ELEVADOR
A= 3,98 m²
BRINQUEDOTECA
R= LAMINADO
A= 17,41 m²
PUB | SALA DE JOGOS
R= PORCELANATO
A= 42,90 m²
ÁREA EXTERNA
R= ANTIDERRAPANTE
A= 20,08 m²
QUIOSQUE II
R= PORCELANATO
A= 24,55 m²
CIRCULAÇÃO
R= PORCELANATO
A= 21,48 m²
CIRCULAÇÃO
R= PORCELANATO
A= 15,34 m²
CASA DE MÁQUINAS
R= CERÂMICA
A= 5,81 m²
MARKET PLACE
R= PORCELANATO
A= 7,80 m²
FLOREIRA
A= 1,93 m²
FLOREIRA
A= 5,75 m²
ÁREA EXTERNA
R= ANTIDERRAPANTE
A= 15,08 m²
FLOREIRA
A= 3,13 m²
WINE BAR
R= PORCELANATO
A= 33,06 m²
LOUNGE
R= PORCELANATO
A= 55,55 m²
COPA
R= PORCELANATO
A= 5,50 m²
DEF
A= 1,10 m²
SALÃO DE FESTAS
R= PORCELANATO
A= 76,65 m²
ACADEMIA
R= PORCELANATO
A= 60,20 m²
I.S.
R= PORCELANATO
A= 2,33 m²
FLOREIRA
A= 11,18 m²
Elev. 02
Elev. 04
N

04° Pavimento | Lazer
1:100

ESQ 05 ESQUADRIAS LAZER

NOME	DIMENSÕES	PEITORIL	TIPO	FOLHA	MATERIAL VISTA	COR	MATERIAL FECHAMENTO	COR FECHAMENTO	QTD
Janela									
GR1	0,80×1,20	1,00	Fixo		Alumínio				1
GR2	0,60×1,20	1,00	Fixo		Alumínio				1
GR2	0,80×1,20	1,80	Fixo		Alumínio				1
GR3	0,60×0,60	1,07	Fixo		Alumínio				1
J01	6,65×2,50	0,00	Basculante; Fixo	07	Alumínio	Chumbo	Vidro	Transparente	1
J02	3,77×2,50	0,00	Basculante; Fixo	04	Alumínio	Chumbo	Vidro	Transparente	1
J03	3,80×2,50	0,00	Basculante; Fixo	06	Alumínio	Chumbo	Vidro	Transparente	1
J04	3,30×2,50	0,00	Basculante; Fixo	06	Alumínio	Chumbo	Vidro	Transparente	1
J04	3,55×2,50	0,00	Basculante; Fixo	06	Alumínio	Chumbo	Vidro	Transparente	1
J05	3,60×2,50	0,00	Basculante; Fixo		Alumínio				1
J06	6,97×2,50	0,00	Basculante; Fixo	07	Alumínio	Chumbo	Vidro	Transparente	1
J07	1,20×1,80	0,00	Basculante; Fixo	03	Alumínio	Chumbo	Vidro	Transparente	1
VF17	2,41×2,50	0,00	Fixo	05	Alumínio	Chumbo	Vidro	Transparente	1
VF18	3,00×2,50	0,00	Fixo	04	Alumínio	Chumbo	Vidro	Transparente	1
VF19	2,20×2,50	0,00	Fixo	02	Alumínio	Chumbo	Vidro	Transparente	1
Porta									
P03	0,90×2,10	0,00	Abrir Simples		Madeira				1
P03	0,90×2,10	0,00	Abrir Simples	01	Madeira	Branco	Madeira	Branco	1
P03	0,90×2,10	0,00	Tipo P90		Aço Galvanizado				2
P03	1,00×2,10	0,00	Tipo P90		Aço Galvanizado				1
P03	1,00×2,10	0,00	Tipo P90	01	Aço Galvanizado	Chumbo	Vidro	Transparente	1
P04	0,70×2,10	0,00	Abrir Simples		Madeira				2
P04	0,70×2,10	0,00	Abrir Simples	01	Madeira	Branco	Madeira	Branco	4
P04	0,80×2,10	0,00	Abrir Simples		Madeira				3
P05	0,70×2,10	0,00	Abrir Simples		Madeira				1
P05	1,20×1,10	0,00	Pivotante	01	Alumínio	Chumbo	Vidro	Transparente	1
P07	1,20×2,40	0,00	Pivotante		Alumínio				2
P07	1,20×2,40	0,00	Pivotante	01	Alumínio	Chumbo	Vidro	Transparente	7
P08	2,50×2,50	0,00	Correr 4 Folhas	04	Alumínio	Chumbo	Vidro	Transparente	1
P09	1,60×2,50	0,00	Correr 4 Folhas	04	Alumínio	Chumbo	Vidro	Transparente	1
P09	1,70×2,50	0,00	Correr 4 Folhas	04	Alumínio	Chumbo	Vidro	Transparente	1
P11	3,90×2,50	0,00	Correr 4 Folhas	04	Alumínio	Chumbo	Vidro	Transparente	1

Projeto Pré-executivo

RODRIGO KIRCK ARQUITETURA

Av. Coronel Marcos Konder nº805, Sala 1108, Centro, Itajaí/Santa Catarina CEP 88301-470
Contato | (47) 3349-7161 | contato@rodrigokirck.com.br

DOM | RAYMUNDI BRAVA

ASSUNTO
PE | | Projeto Pré-executivo
Planta Baixa | Pavimento G04, 04° Pavimento | Lazer
552_EM_Raymundi_DOM_PE_R01.pln

ARQ RESP Danilo Garcia
DESENHO Thaís Pinheiro

REVISÃO
DATA 14/08/2026

PRANCHA
05

OBRA
DOM | RAYMUNDI BRAVA

LOCAL
R. Pra. Jucilia Maria da Silva Miguel - Itajaí - -
Santa Catarina

RESPONSÁVEL TÉCNICO
Danilo dos Santos Garcia
A55244-5

PROPRIETÁRIO
Raymundi Brava RB SPE LTDA
56.344.375/0001-23

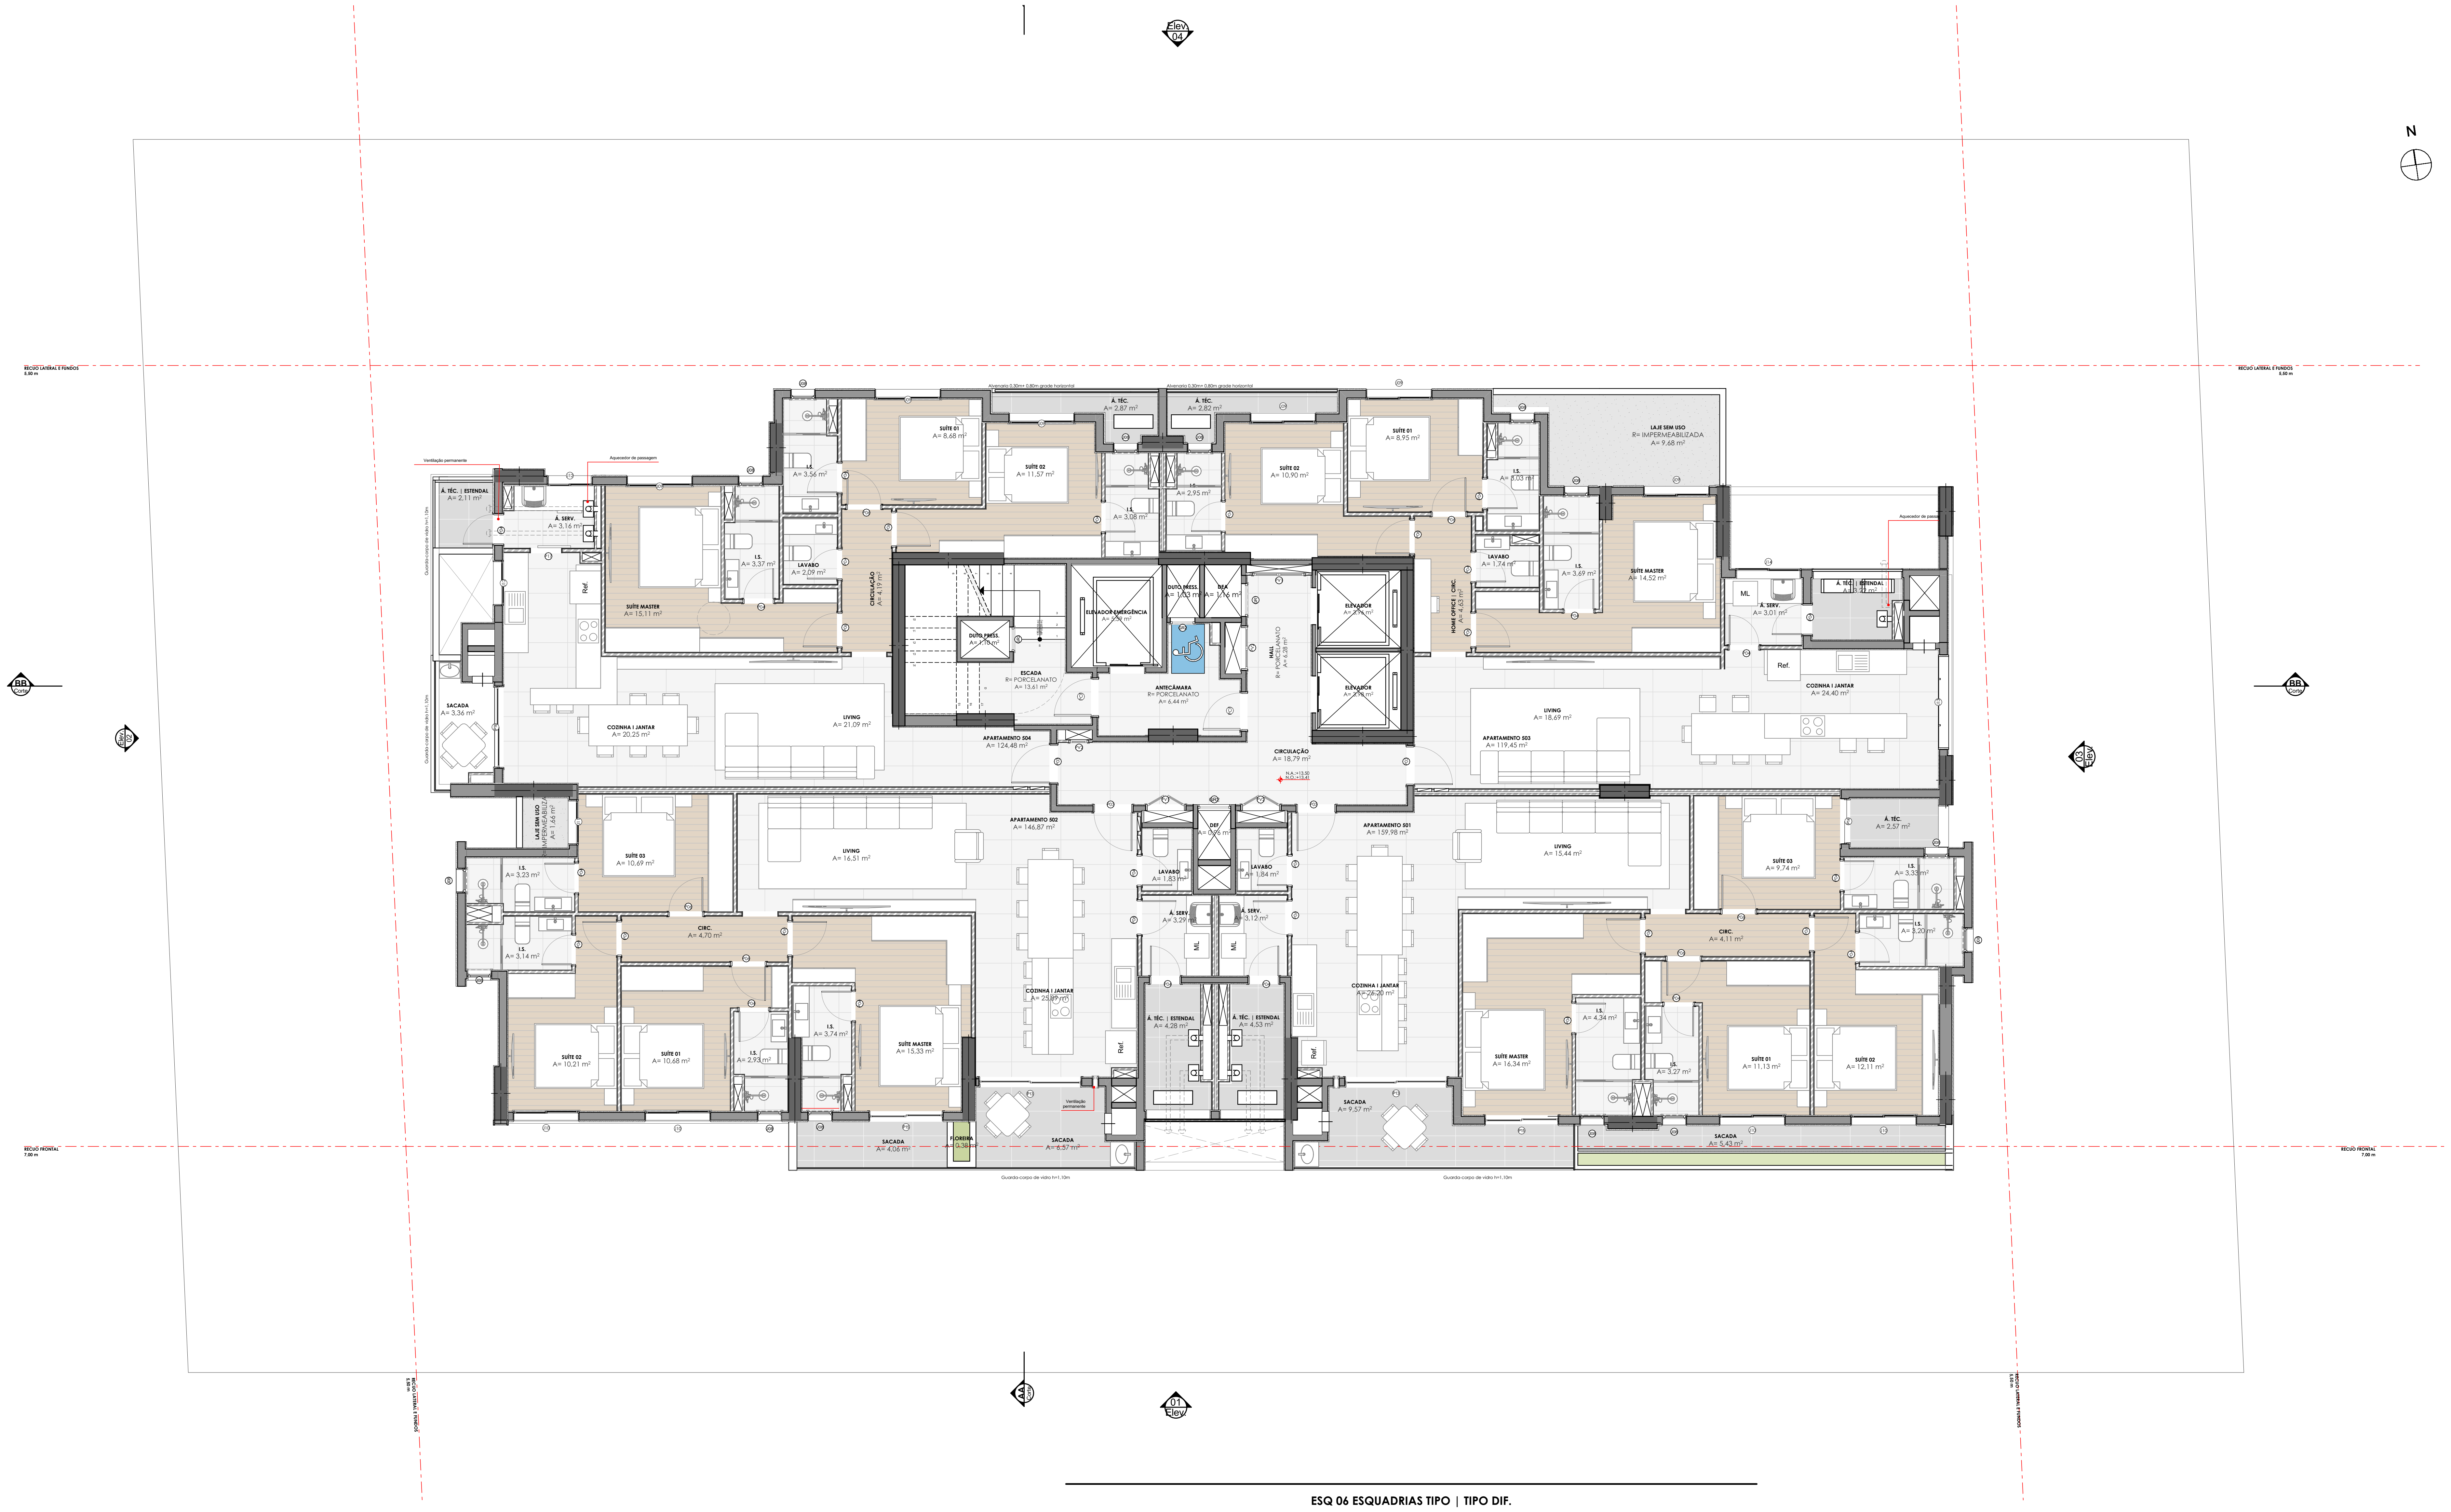
N
Ventilação permanente
Aquecedor de passagem
Á. TÉC. | ESTENDAL A= 2,11 m²
Á. SERV. A= 3,16 m²
SUÍTE MASTER A= 15,11 m²
I.S. A= 3,37 m²
LAVABO A= 2,09 m²
I.S. A= 3,56 m²
SUÍTE 01 A= 8,68 m²
SUÍTE 02 A= 11,57 m²
CIRCULAÇÃO A= 4,19 m²
SACADA A= 3,36 m²
COZINHA I JANTAR A= 20,25 m²
LIVING A= 21,09 m²
Guarda-corpo de vidro h=1,10m
Alvenaria 0,30m+ 0,80m grade horizontal
Á. TÉC. A= 2,87 m²
Á. TÉC. A= 2,82 m²
I.S. A= 3,08 m²
I.S. A= 2,95 m²
SUÍTE 02 A= 10,90 m²
SUÍTE 01 A= 8,95 m²
I.S. A= 3,03 m²
LAJE SEM USO R= IMPERMEABILIZADA A= 9,68 m²
LAVABO A= 1,74 m²
I.S. A= 3,69 m²
SUÍTE MASTER A= 14,52 m²
HOME OFFICE | CIRC. A= 4,63 m²
ML
Á. SERV. A= 3,01 m²
Á. TÉC. | ESTENDAL A= 3,22 m²
Ref.
COZINHA I JANTAR A= 24,40 m²
LIVING A= 18,69 m²
APARTAMENTO 503 A= 119,45 m²
ESCADA R= PORCELANATO A= 13,61 m²
DUTO PRESS. A= 1,10 m²
ELEVADOR EMERGÊNCIA A= 5,59 m²
DUTO PRESS. A= 1,03 m²
DEA A= 1,16 m²
ANTECÂMARA R= PORCELANATO A= 6,44 m²
HALL R= PORCELANATO A= 6,28 m²
ELEVADOR A= 3,96 m²
ELEVADOR A= 3,98 m²
CIRCULAÇÃO A= 18,79 m²
N.A.:+13,50
N.O.:+13,41
APARTAMENTO 504 A= 124,48 m²
APARTAMENTO 502 A= 146,87 m²
APARTAMENTO 501 A= 159,98 m²
LAJE SEM USO R= IMPERMEABILIZADA A= 1,66 m²
SUÍTE 03 A= 10,69 m²
LIVING A= 16,51 m²
I.S. A= 3,23 m²
I.S. A= 3,14 m²
CIRC. A= 4,70 m²
SUÍTE 02 A= 10,21 m²
SUÍTE 01 A= 10,68 m²
I.S. A= 2,93 m²
I.S. A= 3,74 m²
SUÍTE MASTER A= 15,33 m²
SACADA A= 4,06 m²
FLOREIRA A= 0,38 m²
SACADA A= 6,57 m²
COZINHA I JANTAR A= 25,89 m²
LAVABO A= 1,83 m²
Á. SERV. A= 3,29 m²
Á. TÉC. | ESTENDAL A= 4,28 m²
DEF A= 0,96 m²
LAVABO A= 1,84 m²
Á. SERV. A= 3,12 m²
Á. TÉC. | ESTENDAL A= 4,53 m²
COZINHA I JANTAR A= 26,20 m²
SACADA A= 9,57 m²
LIVING A= 15,44 m²
SUÍTE 03 A= 9,74 m²
Á. TÉC. A= 2,57 m²
I.S. A= 3,33 m²
I.S. A= 3,20 m²
CIRC. A= 4,11 m²
SUÍTE MASTER A= 16,34 m²
I.S. A= 4,34 m²
I.S. A= 3,27 m²
SUÍTE 01 A= 11,13 m²
SUÍTE 02 A= 12,11 m²
SACADA A= 5,43 m²
AA Corte
01 Elev.

4. 05º Pavimento | Tipo Diferenciado
1:100

ESQ 06 ESQUADRIAS TIPO | TIPO DIF.

NOME	DIMENSÕES	PEITORIL	TIPO	FOLHA	MATERIAL VISTA	COR	MATERIAL FECHAMENTO	COR FECHAMENTO	QTD
Janela									
GR1	0,80×1,20	1,00	Fixo		Alumínio				1
GR2	0,60×1,20	1,00	Fixo		Alumínio				1
GR2	0,80×1,20	1,80	Fixo		Alumínio				1
GR3	0,60×0,60	1,07	Fixo		Alumínio				1
J08	0,60×0,80	1,50	Basculante		Alumínio				13
J08	0,60×0,80	1,50	Basculante	01	Alumínio	Chumbo	Vidro	Transparente	1
J09	1,60×1,40	0,90	Correr 2 Folhas; Fixo	02	Alumínio	Chumbo	Vidro	Transparente	6
J10	1,60×1,80	0,50	Correr 2 Folhas; Fixo		Alumínio				4
J11	1,10×1,40	0,90	Correr 2 Folhas	02	Alumínio	Chumbo	Vidro	Transparente	1
J12	1,10×1,20	1,10	Correr 2 Folhas	02	Alumínio	Chumbo	Vidro	Transparente	1
J12	1,10×1,20	1,20	Correr 2 Folhas	02	Alumínio	Chumbo	Vidro	Transparente	1
J13	2,30×1,80	0,50	Basculante; Fixo	04	Alumínio	Chumbo	Vidro	Transparente	1
J14	1,60×1,20	1,10	Correr 2 Folhas	02	Alumínio	Chumbo	Vidro	Transparente	1
Porta									
P03	0,90×2,10	0,00	Abrir Simples	01	Madeira	Branco	Madeira	Branco	4
P04	0,70×2,10	0,00	Abrir Simples		Madeira				5
P04	0,70×2,10	0,00	Abrir Simples	01	Madeira	Branco	Madeira	Branco	18
P06	0,80×2,10	0,00	Abrir Simples	01	Madeira	Branco	Madeira	Branco	16
P13	2,50×2,30	0,00	Correr 3 Folhas	03	Alumínio	Chumbo	Vidro	Transparente	2
P14	1,10×2,30	0,00	Correr 2 Folhas	02	Alumínio	Chumbo	Vidro	Transparente	1
P15	1,80×2,30	0,00	Correr 2 Folhas		Alumínio				2
P16	2,00×2,30	0,00	Correr 2 Folhas	02	Alumínio	Chumbo	Vidro	Transparente	1
P17	0,80×2,10	0,00	Correr 1 Folha	01	Madeira	Branco	Madeira	Branco	1
PCF	0,90×2,10	0,00	Tipo P90		Aço Galvanizado				2
PV1	0,90×2,10	0,00	Abrir Simples		Madeira				1
PV1	1,20×2,10	0,00	Abrir Simples		Madeira				1

Projeto Pré-executivo

RODRIGO KIRCK ARQUITETURA

Av. Coronel Marcos Konder nº805, Sala 1108, Centro, Itajaí/Santa Catarina CEP 88301-470
Contato | (47) 3349-7161 | contato@rodrigokirck.com.br

DOM | RAYMUNDI BRAVA

ASSUNTO
PE | | Projeto Pré-executivo
Planta Baixa | Pavimento G04, 4. 05º Pavimento | Tipo Diferenciado
552_EM_Raymundi_DOM_PE_R01.pln

ARQ RESP: Danilo Garcia
DESENHO: Thaís Pinheiro

REVISÃO
DATA: 14/08/2026

PRANCHA
06

OBRA
DOM | RAYMUNDI BRAVA

LOCAL
R. Pra. Jucilia Maria da Silva Miguel - Itajaí - -
Santa Catarina

RESPONSÁVEL TÉCNICO

Danilo dos Santos Garcia
A55244-5

PROPRIETÁRIO

Raymundi Brava RB SPE LTDA
56.344.375/0001-23

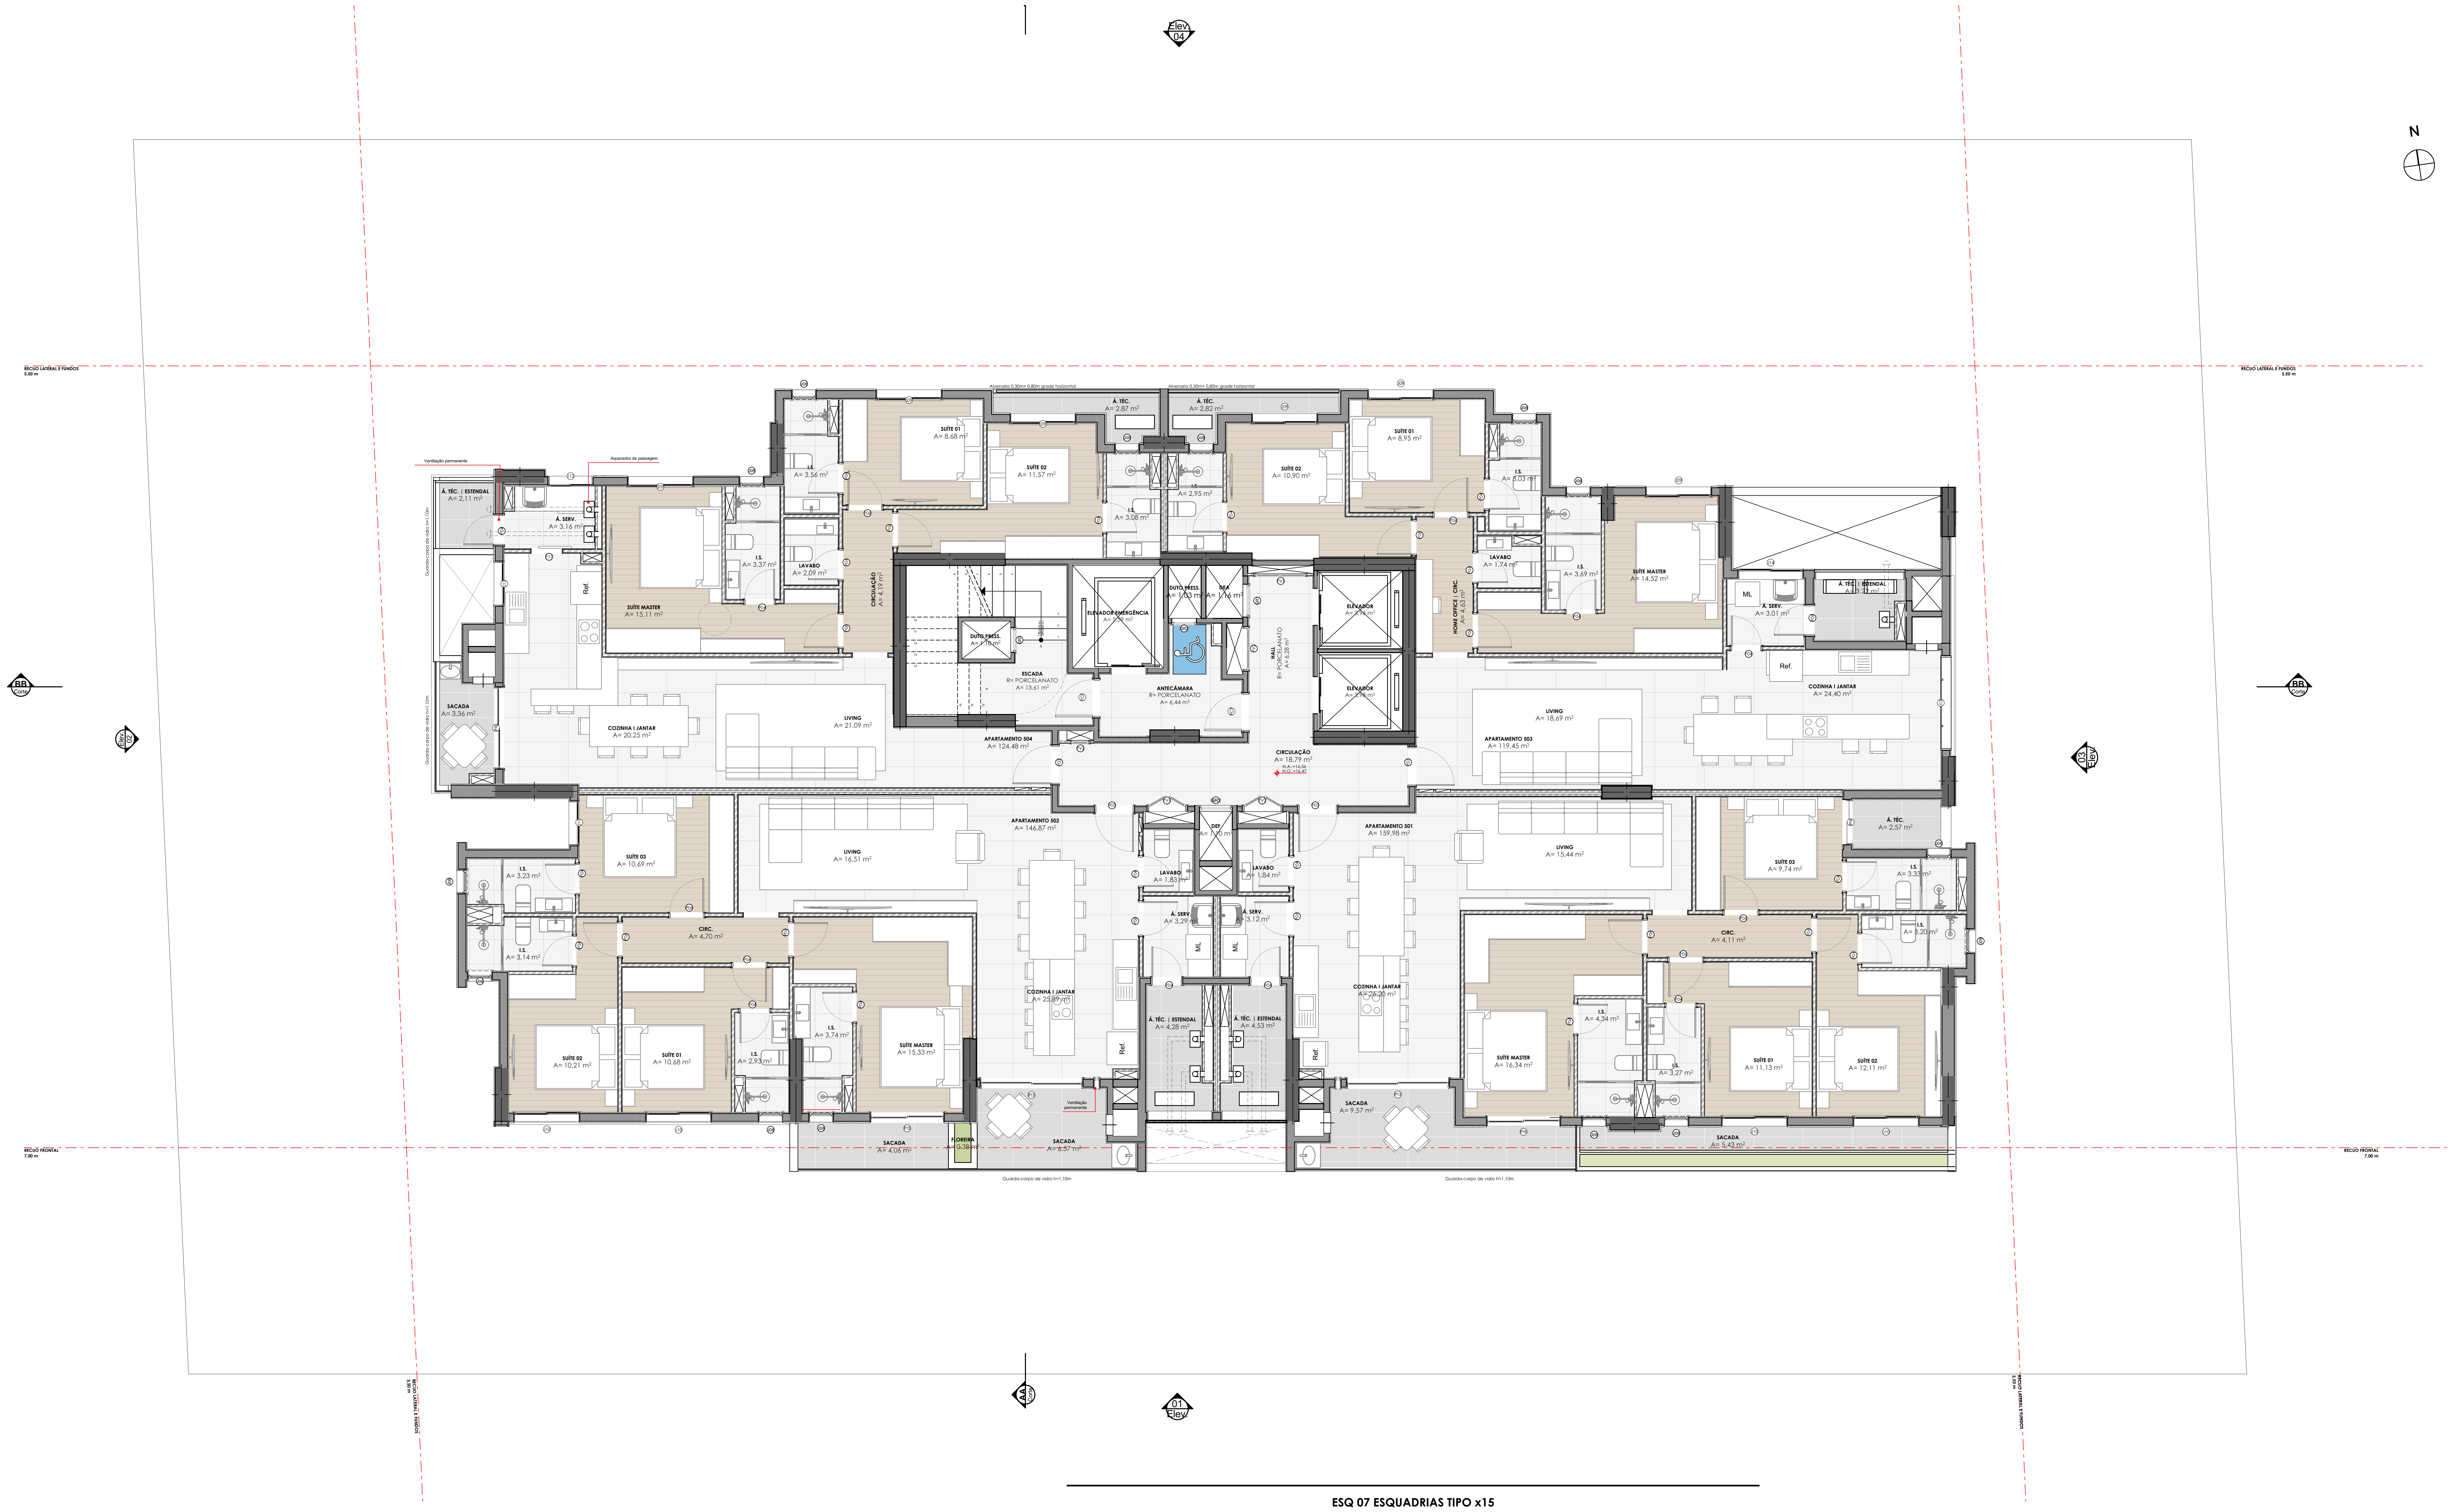

5. 06º Pavimento | Tipo X15
1:100

ESQ 07 ESQUADRIAS TIPO x15

NOME	DIMENSÕES	PEITORIL	TIPO	FOLHA	MATERIAL VISTA	COR	MATERIAL FECHAMENTO	COR FECHAMENTO	QTD
Janela									
GR1	0,80×1,20	1,00	Fixo		Alumínio				1
GR2	0,60×1,20	1,00	Fixo		Alumínio				1
GR2	0,80×1,20	1,80	Fixo		Alumínio				1
GR3	0,60×0,60	1,07	Fixo		Alumínio				1
J08	0,60×0,80	1,50	Basculante		Alumínio				13
J08	0,60×0,80	1,50	Basculante	01	Alumínio	Chumbo	Vidro	Transparente	1
J09	1,60×1,40	0,90	Correr 2 Folhas; Fixo	02	Alumínio	Chumbo	Vidro	Transparente	6
J10	1,60×1,80	0,50	Correr 2 Folhas; Fixo		Alumínio				4
J11	1,10×1,40	0,90	Correr 2 Folhas	02	Alumínio	Chumbo	Vidro	Transparente	1
J12	1,10×1,20	1,10	Correr 2 Folhas	02	Alumínio	Chumbo	Vidro	Transparente	1
J12	1,10×1,20	1,20	Correr 2 Folhas	02	Alumínio	Chumbo	Vidro	Transparente	1
J13	2,30×1,80	0,50	Basculante; Fixo	04	Alumínio	Chumbo	Vidro	Transparente	1
J14	1,60×1,20	1,10	Correr 2 Folhas	02	Alumínio	Chumbo	Vidro	Transparente	1
Porta									
P03	0,90×2,10	0,00	Abrir Simples	01	Madeira	Branco	Madeira	Branco	4
P04	0,70×2,10	0,00	Abrir Simples		Madeira				5
P04	0,70×2,10	0,00	Abrir Simples	01	Madeira	Branco	Madeira	Branco	18
P06	0,80×2,10	0,00	Abrir Simples	01	Madeira	Branco	Madeira	Branco	16
P13	2,50×2,30	0,00	Correr 3 Folhas	03	Alumínio	Chumbo	Vidro	Transparente	2
P14	1,10×2,30	0,00	Correr 2 Folhas	02	Alumínio	Chumbo	Vidro	Transparente	1
P15	1,80×2,30	0,00	Correr 2 Folhas		Alumínio				2
P16	2,00×2,30	0,00	Correr 2 Folhas	02	Alumínio	Chumbo	Vidro	Transparente	1
P17	0,80×2,10	0,00	Correr 1 Folha	01	Madeira	Branco	Madeira	Branco	1
PCF	0,90×2,10	0,00	Tipo P90		Aço Galvanizado				2
PV1	0,90×2,10	0,00	Abrir Simples		Madeira				1
PV1	1,20×2,10	0,00	Abrir Simples		Madeira				1

Projeto Pré-executivo

RODRIGO KIRCK ARQUITETURA

Av. Coronel Marcos Konder nº805, Sala 1108, Centro, Itajaí/Santa Catarina CEP 88301-470
Contato | (47) 3349-7161 | contato@rodrigokirck.com.br

DOM | RAYMUNDI BRAVA

ASSUNTO
PE | | Projeto Pré-executivo
Planta Baixa | Pavimento G04, 5. 06º Pavimento | Tipo X15
552_EM_Raymundi_DOM_PE_R01.pln

ARQ RESP Danilo Garcia
DESENHO Thaís Pinheiro

REVISÃO
DATA 14/08/2026

PRANCHA
07

OBRA
DOM | RAYMUNDI BRAVA

LOCAL
R. Pra. Jucilia Maria da Silva Miguel - Itajaí - -
Santa Catarina

RESPONSÁVEL TÉCNICO

Danilo dos Santos Garcia
A55244-5

PROPRIETÁRIO

Raymundi Brava RB SPE LTDA
56.344.375/0001-23

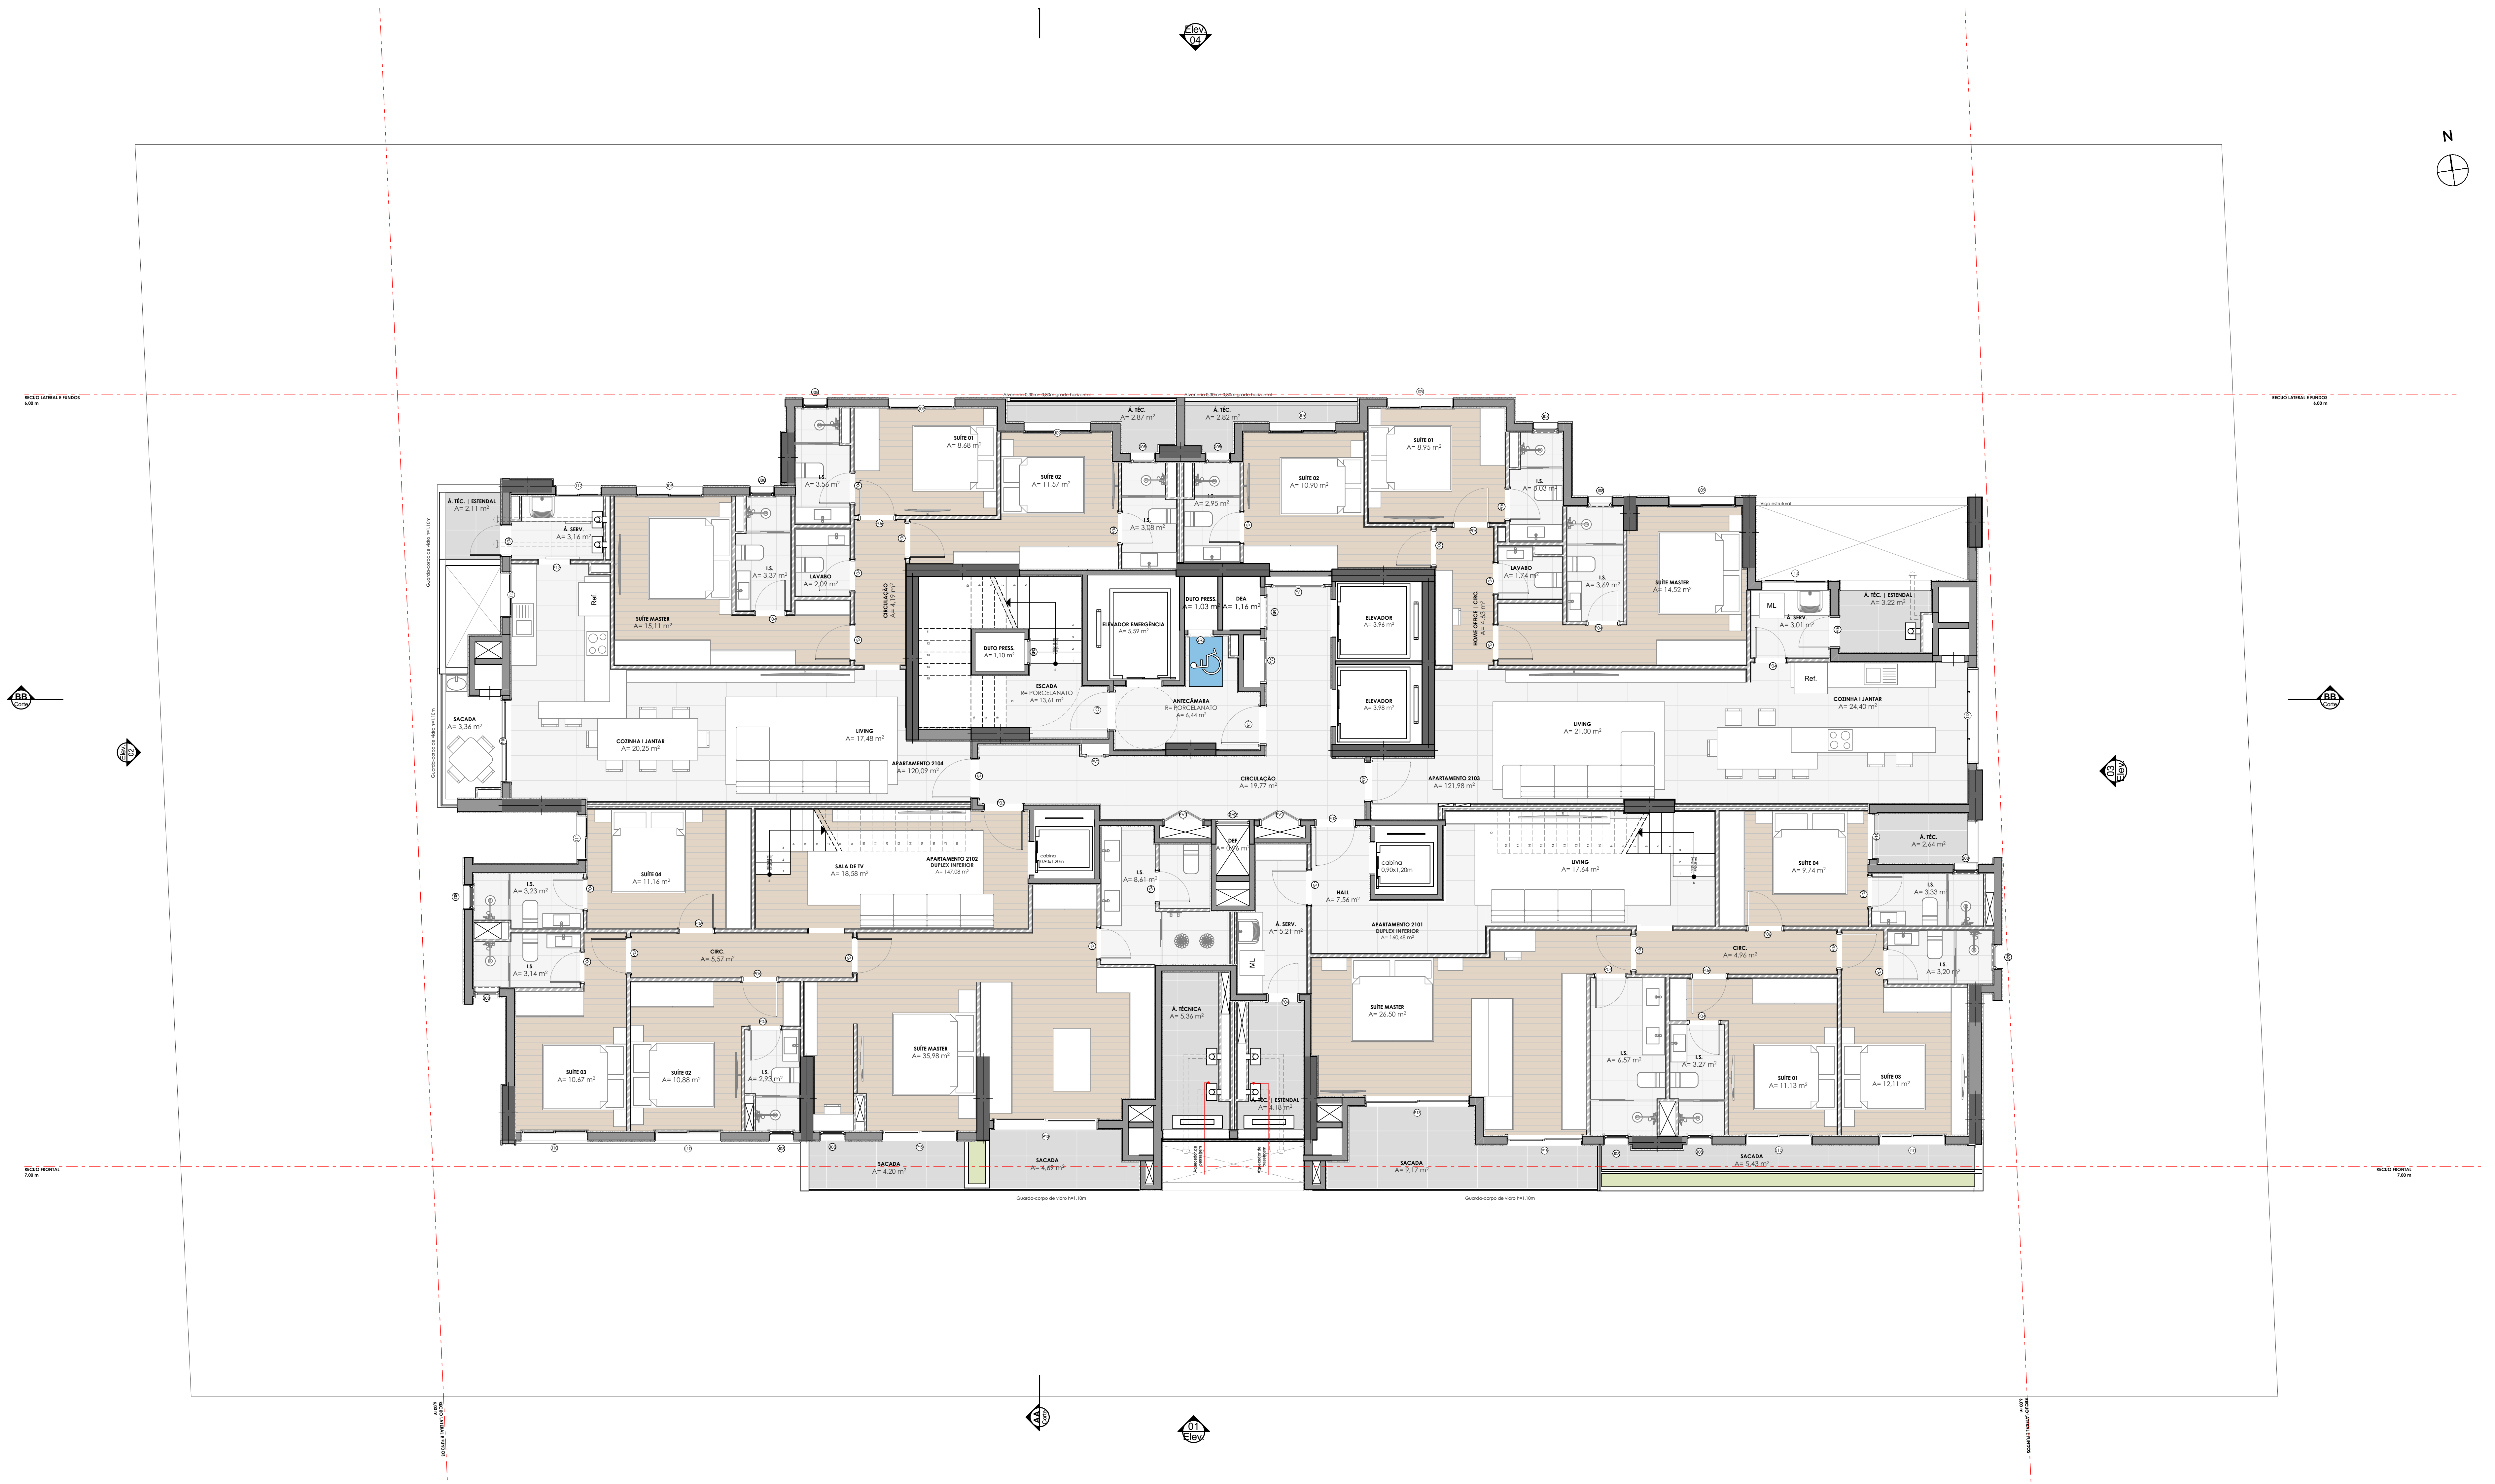

20. 21° Pavimento | Duplex Inferior
1:100

ESQ 06 ESQUADRIAS DUPLEX INFERIOR

NOME	DIMENSÕES	PEITORIL	TIPO	FOLHA	MATERIAL VISTA	COR	MATERIAL FECHAMENTO	COR FECHAMENTO	QTD
Janela									
GR1	0,80×1,20	1,00	Fixo		Alumínio				1
GR2	0,60×1,20	1,00	Fixo		Alumínio				1
GR2	0,80×1,20	1,80	Fixo		Alumínio				1
GR3	0,60×0,60	1,07	Fixo		Alumínio				1
J08	0,60×0,80	1,50	Basculante		Alumínio				13
J08	0,60×0,80	1,50	Basculante	01	Alumínio	Chumbo	Vidro	Transparente	1
J09	1,60×1,40	0,90	Correr 2 Folhas; Fixo	02	Alumínio	Chumbo	Vidro	Transparente	6
J10	1,60×1,80	0,50	Correr 2 Folhas; Fixo		Alumínio				4
J11	1,10×1,40	0,90	Correr 2 Folhas	02	Alumínio	Chumbo	Vidro	Transparente	1
J12	1,10×1,20	1,10	Correr 2 Folhas	02	Alumínio	Chumbo	Vidro	Transparente	1
J12	1,10×1,20	1,20	Correr 2 Folhas	02	Alumínio	Chumbo	Vidro	Transparente	1
J13	2,30×1,80	0,50	Basculante; Fixo	04	Alumínio	Chumbo	Vidro	Transparente	1
J14	1,60×1,20	1,10	Correr 2 Folhas	02	Alumínio	Chumbo	Vidro	Transparente	1
Porta									
P03	0,90×2,10	0,00	Abrir Simples		Madeira				1
P03	0,90×2,10	0,00	Abrir Simples	01	Madeira	Branco	Madeira	Branco	1
P03	0,90×2,10	0,07	Abrir Simples	01	Madeira	Branco	Madeira	Branco	2
P04	0,70×2,10	0,00	Abrir Simples		Madeira				5
P04	0,70×2,10	0,00	Abrir Simples	01	Madeira	Branco	Madeira	Branco	16
P06	0,80×2,10	0,00	Abrir Simples		Madeira				1
P06	0,80×2,10	0,00	Abrir Simples	01	Madeira	Branco	Madeira	Branco	14
P13	2,50×2,30	0,00	Correr 3 Folhas	03	Alumínio	Chumbo	Vidro	Transparente	2
P14	1,10×2,30	0,00	Correr 2 Folhas	02	Alumínio	Chumbo	Vidro	Transparente	1
P15	1,80×2,30	0,00	Correr 2 Folhas		Alumínio				2
P16	2,00×2,30	0,00	Correr 2 Folhas	02	Alumínio	Chumbo	Vidro	Transparente	1
P17	0,80×2,10	0,00	Correr 1 Folha	01	Madeira	Branco	Madeira	Branco	1

Projeto Pré-executivo

RODRIGO KIRCK ARQUITETURA

Av. Coronel Marcos Konder nº805, Sala 1108, Centro, Itajaí/Santa Catarina CEP 88301-470
Contato | (47) 3349-7161 | contato@rodrigokirck.com.br

DOM | RAYMUNDI BRAVA

ASSUNTO
PE | | Projeto Pré-executivo
Planta Baixa | Pavimento G04, 20. 21° Pavimento | Duplex Inferior
552_EM_Raymundi_DOM_PE_R01.pln

ARQ RESP Danilo Garcia
DESENHO Thaís Pinheiro

REVISÃO
DATA 14/08/2026

PRANCHA
08

OBRA
DOM | RAYMUNDI BRAVA

LOCAL
R. Pra. Jucilia Maria da Silva Miguel - Itajaí - - Santa Catarina

RESPONSÁVEL TÉCNICO
Danilo dos Santos Garcia
A55244-5

PROPRIETÁRIO
Raymundi Brava RB SPE LTDA
56.344.375/0001-23

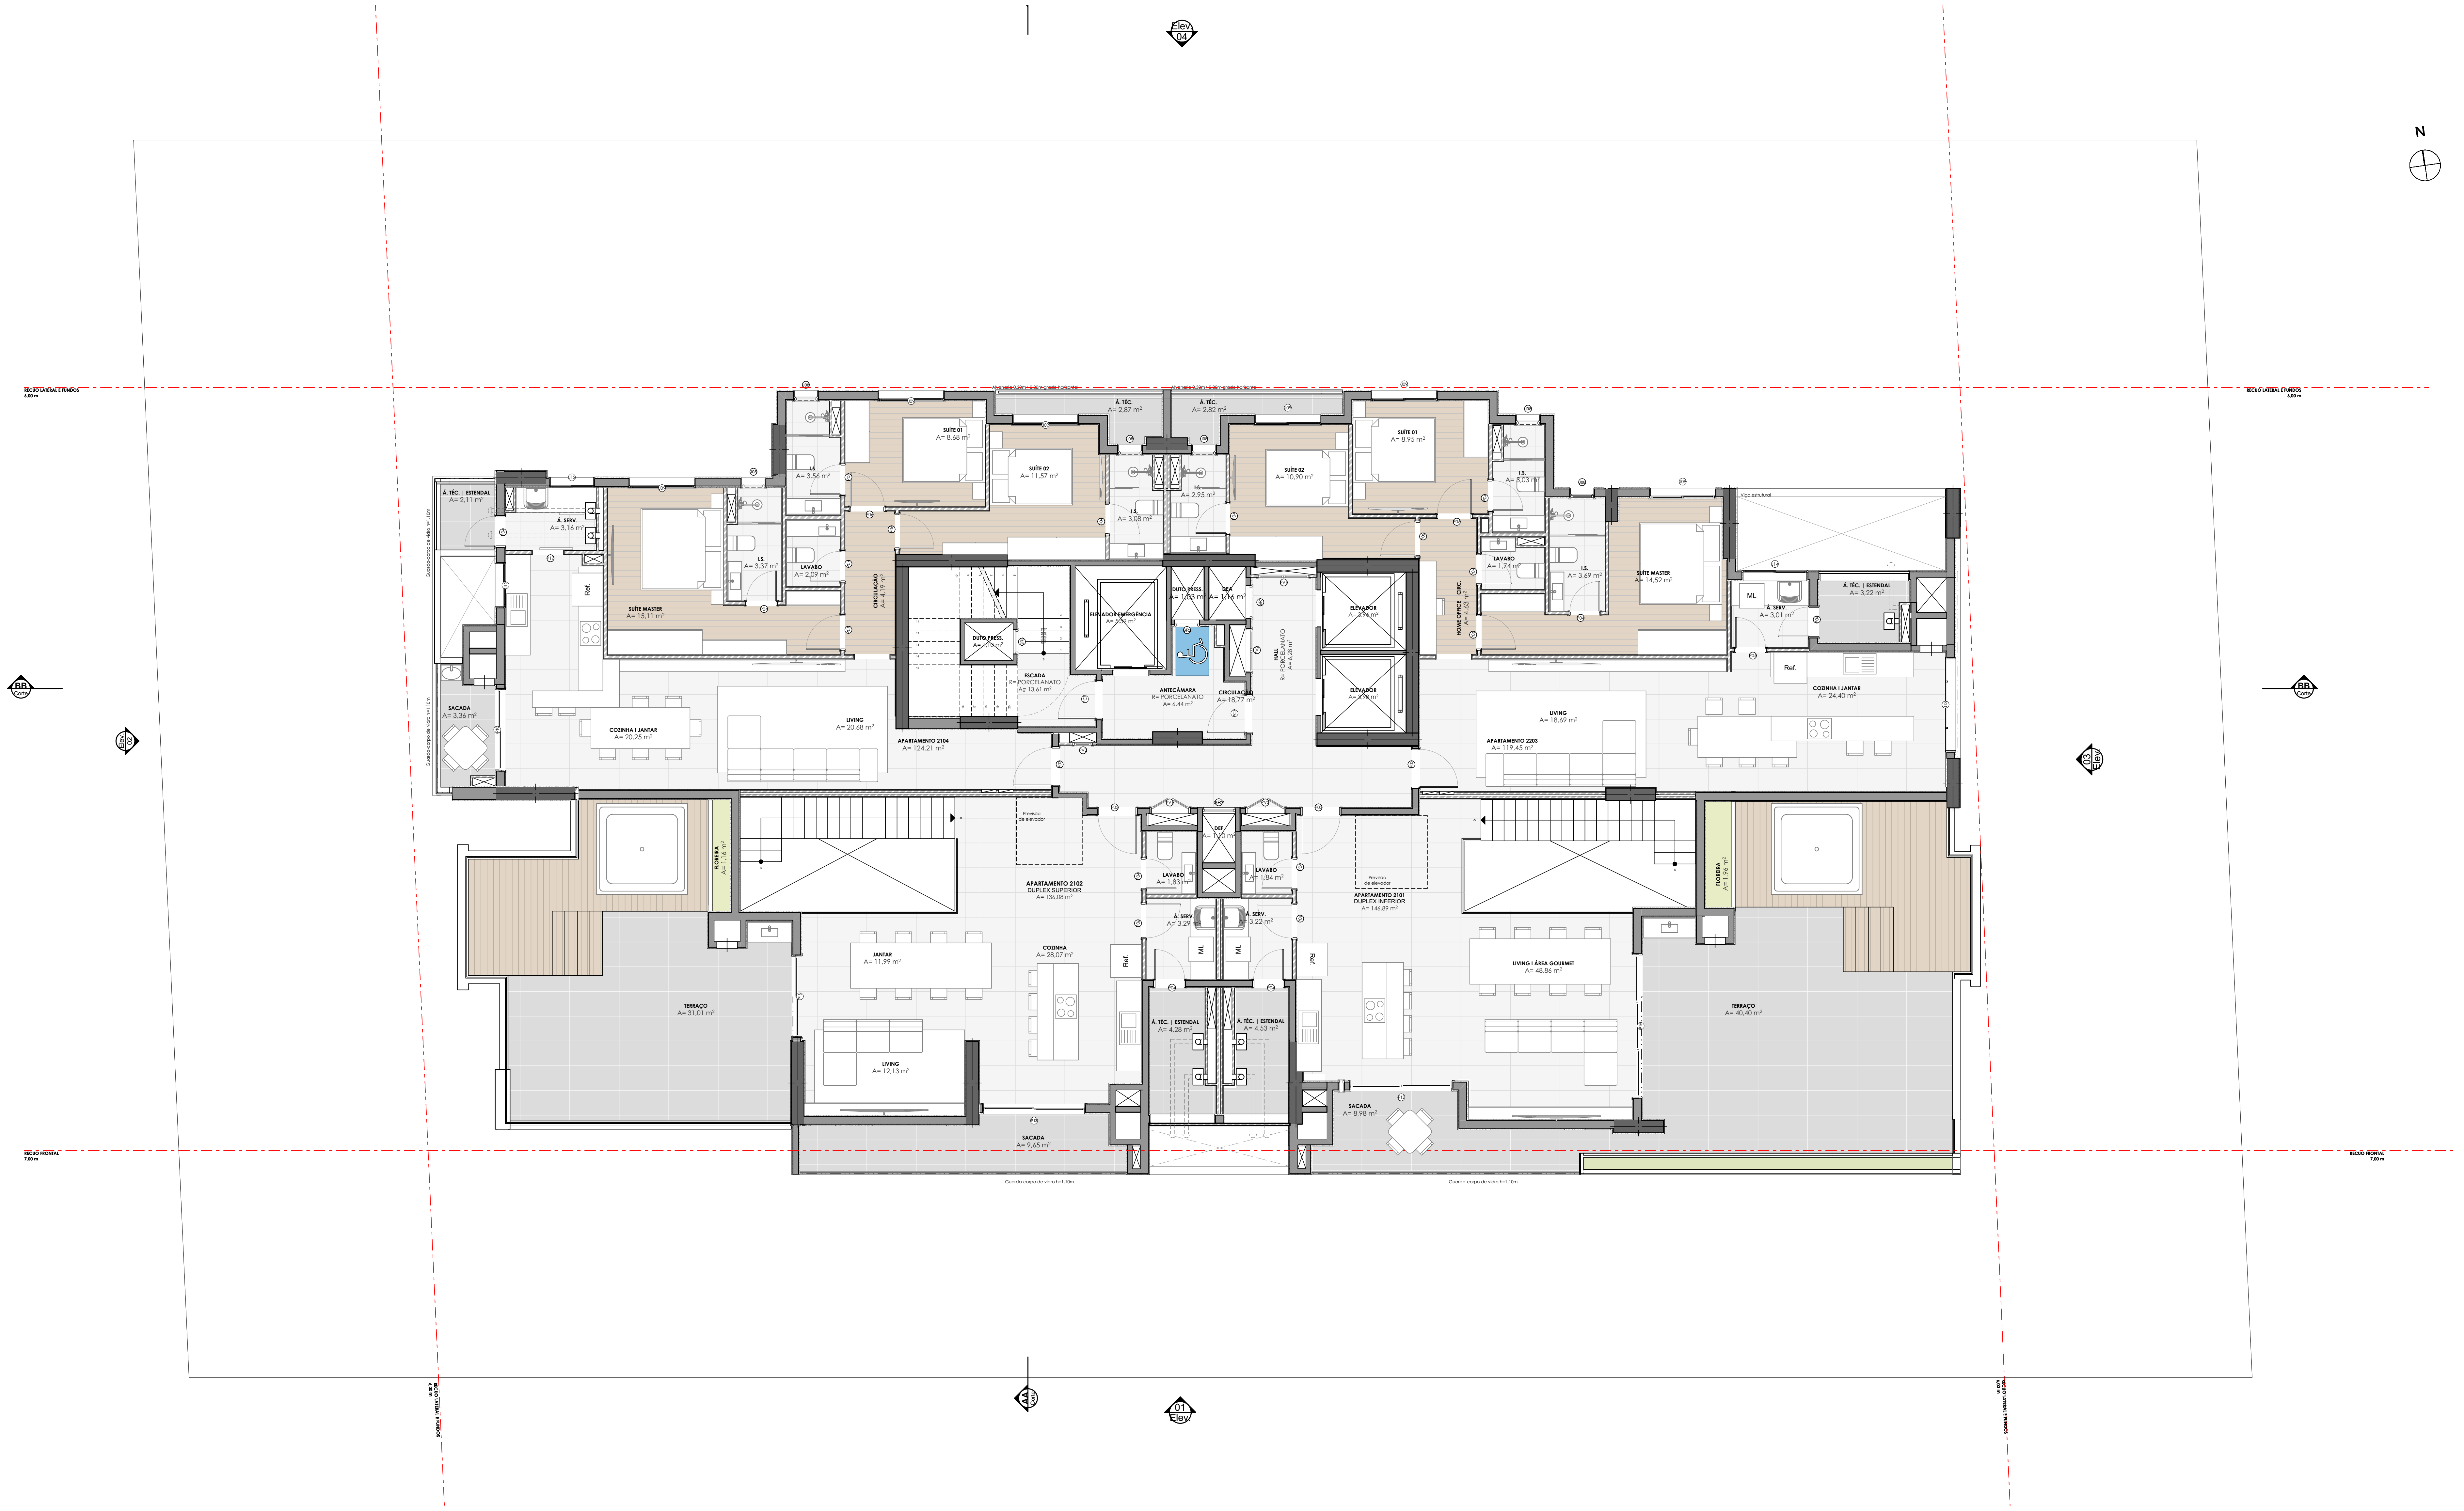
N
Á. TÉC. | ESTENDAL A= 2,11 m²
Á. SERV. A= 3,16 m²
SUÍTE MASTER A= 15,11 m²
I.S. A= 3,37 m²
LAVABO A= 2,09 m²
I.S. A= 3,56 m²
SUÍTE 01 A= 8,68 m²
SUÍTE 02 A= 11,57 m²
CIRCULAÇÃO A= 4,19 m²
Á. TÉC. A= 2,87 m²
Á. TÉC. A= 2,82 m²
I.S. A= 3,08 m²
I.S. A= 2,95 m²
SACADA A= 3,36 m²
COZINHA I JANTAR A= 20,25 m²
LIVING A= 20,68 m²
APARTAMENTO 2104 A= 124,21 m²
DUTO PRESS. A= 1,10 m²
ESCADA R= PORCELANATO A= 13,61 m²
ELEVADOR EMERGÊNCIA A= 5,59 m²
DUTO PRESS. A= 1,03 m²
DEA A= 1,16 m²
ANTECÂMARA R= PORCELANATO A= 6,44 m²
CIRCULAÇÃO A= 18,77 m²
HALL R= PORCELANATO A= 6,28 m²
ELEVADOR A= 3,96 m²
ELEVADOR A= 3,98 m²
SUÍTE 02 A= 10,90 m²
SUÍTE 01 A= 8,95 m²
I.S. A= 3,03 m²
HOME OFFICE | CIRC. A= 4,63 m²
LAVABO A= 1,74 m²
I.S. A= 3,69 m²
SUÍTE MASTER A= 14,52 m²
Viga estrutural
Á. SERV. A= 3,01 m²
Á. TÉC. | ESTENDAL A= 3,22 m²
ML
Ref.
COZINHA I JANTAR A= 24,40 m²
LIVING A= 18,69 m²
APARTAMENTO 2203 A= 119,45 m²
Previsão de elevador
DEF A= 1,10 m²
LAVABO A= 1,83 m²
LAVABO A= 1,84 m²
Á. SERV. A= 3,29 m²
Á. SERV. A= 3,22 m²
APARTAMENTO 2102 DUPLEX SUPERIOR A= 136,08 m²
APARTAMENTO 2101 DUPLEX INFERIOR A= 146,89 m²
FLOREIRA A= 1,16 m²
FLOREIRA A= 1,96 m²
TERRAÇO A= 31,01 m²
JANTAR A= 11,99 m²
COZINHA A= 28,07 m²
LIVING A= 12,13 m²
Á. TÉC. | ESTENDAL A= 4,28 m²
Á. TÉC. | ESTENDAL A= 4,53 m²
LIVING I ÁREA GOURMET A= 48,86 m²
TERRAÇO A= 40,40 m²
SACADA A= 9,65 m²
SACADA A= 8,98 m²
Guarda-corpo de vidro h=1,10m
Alvenaria 0,30m + 0,80m grade horizontal

21. 22º Pavimento | Duplex Superior
1:100

ESQ 08 ESQUADRIAS DUPLEX SUPERIOR

NOME	DIMENSÕES	PEITORIL	TIPO	FOLHA	MATERIAL VISTA	COR	MATERIAL FECHAMENTO	COR FECHAMENTO	QTD
Janela									
GR1	0,80×1,20	1,00	Fixo		Alumínio				1
GR2	0,60×1,20	1,00	Fixo		Alumínio				1
GR2	0,80×1,20	1,80	Fixo		Alumínio				1
GR3	0,60×0,60	1,07	Fixo		Alumínio				1
J08	0,60×0,80	1,50	Basculante		Alumínio				6
J09	1,60×1,40	0,90	Correr 2 Folhas; Fixo	02	Alumínio	Chumbo	Vidro	Transparente	6
J12	1,10×1,20	1,10	Correr 2 Folhas	02	Alumínio	Chumbo	Vidro	Transparente	1
J12	1,10×1,20	1,20	Correr 2 Folhas	02	Alumínio	Chumbo	Vidro	Transparente	1
J13	2,30×1,80	0,50	Basculante; Fixo	04	Alumínio	Chumbo	Vidro	Transparente	1
J14	1,60×1,20	1,10	Correr 2 Folhas	02	Alumínio	Chumbo	Vidro	Transparente	1
Porta									
P03	0,90×2,10	0,00	Abrir Simples	01	Madeira	Branco	Madeira	Branco	4
P04	0,70×2,10	0,00	Abrir Simples		Madeira				3
P04	0,70×2,10	0,00	Abrir Simples	01	Madeira	Branco	Madeira	Branco	12
P06	0,80×2,10	0,00	Abrir Simples	01	Madeira	Branco	Madeira	Branco	8
P13	2,50×2,30	0,00	Correr 3 Folhas	03	Alumínio	Chumbo	Vidro	Transparente	2
P16	2,00×2,30	0,00	Correr 2 Folhas	02	Alumínio	Chumbo	Vidro	Transparente	1
P16	2,00×2,30	0,00	Correr 2 Folhas	03	Alumínio	Chumbo	Vidro	Transparente	1
P16	3,50×2,30	0,00	Correr 2 Folhas		Alumínio				1
P17	0,80×2,10	0,00	Correr 1 Folha	01	Madeira	Branco	Madeira	Branco	1
PCF	0,90×2,10	0,00	Tipo P90		Aço Galvanizado				2
PV1	0,90×2,10	0,00	Abrir Simples		Madeira				1
PV1	1,20×2,10	0,00	Abrir Simples		Madeira				1

Projeto Pré-executivo

RODRIGO KIRCK ARQUITETURA

Av. Coronel Marcos Konder nº805, Sala 1108, Centro, Itajaí/Santa Catarina CEP 88301-470
Contato | (47) 3349-7161 | contato@rodrigokirck.com.br

DOM | RAYMUNDI BRAVA

ASSUNTO			**PRANCHA**
PE | | Projeto Pré-executivo Planta Baixa | Pavimento G04, 21. 22º Pavimento | Duplex Superior	ARQ RESP	Danilo Garcia	09
	DESENHO	Thaís Pinheiro	
	REVISÃO		
552_EM_Raymundi_DOM_PE_R01.pln	DATA	14/08/2026	

OBRA
DOM | RAYMUNDI BRAVA

LOCAL
R. Pra. Jucilia Maria da Silva Miguel - Itajaí - -
Santa Catarina

RESPONSÁVEL TÉCNICO

Danilo dos Santos Garcia
A55244-5

PROPRIETÁRIO

Raymundi Brava RB SPE LTDA
56.344.375/0001-23

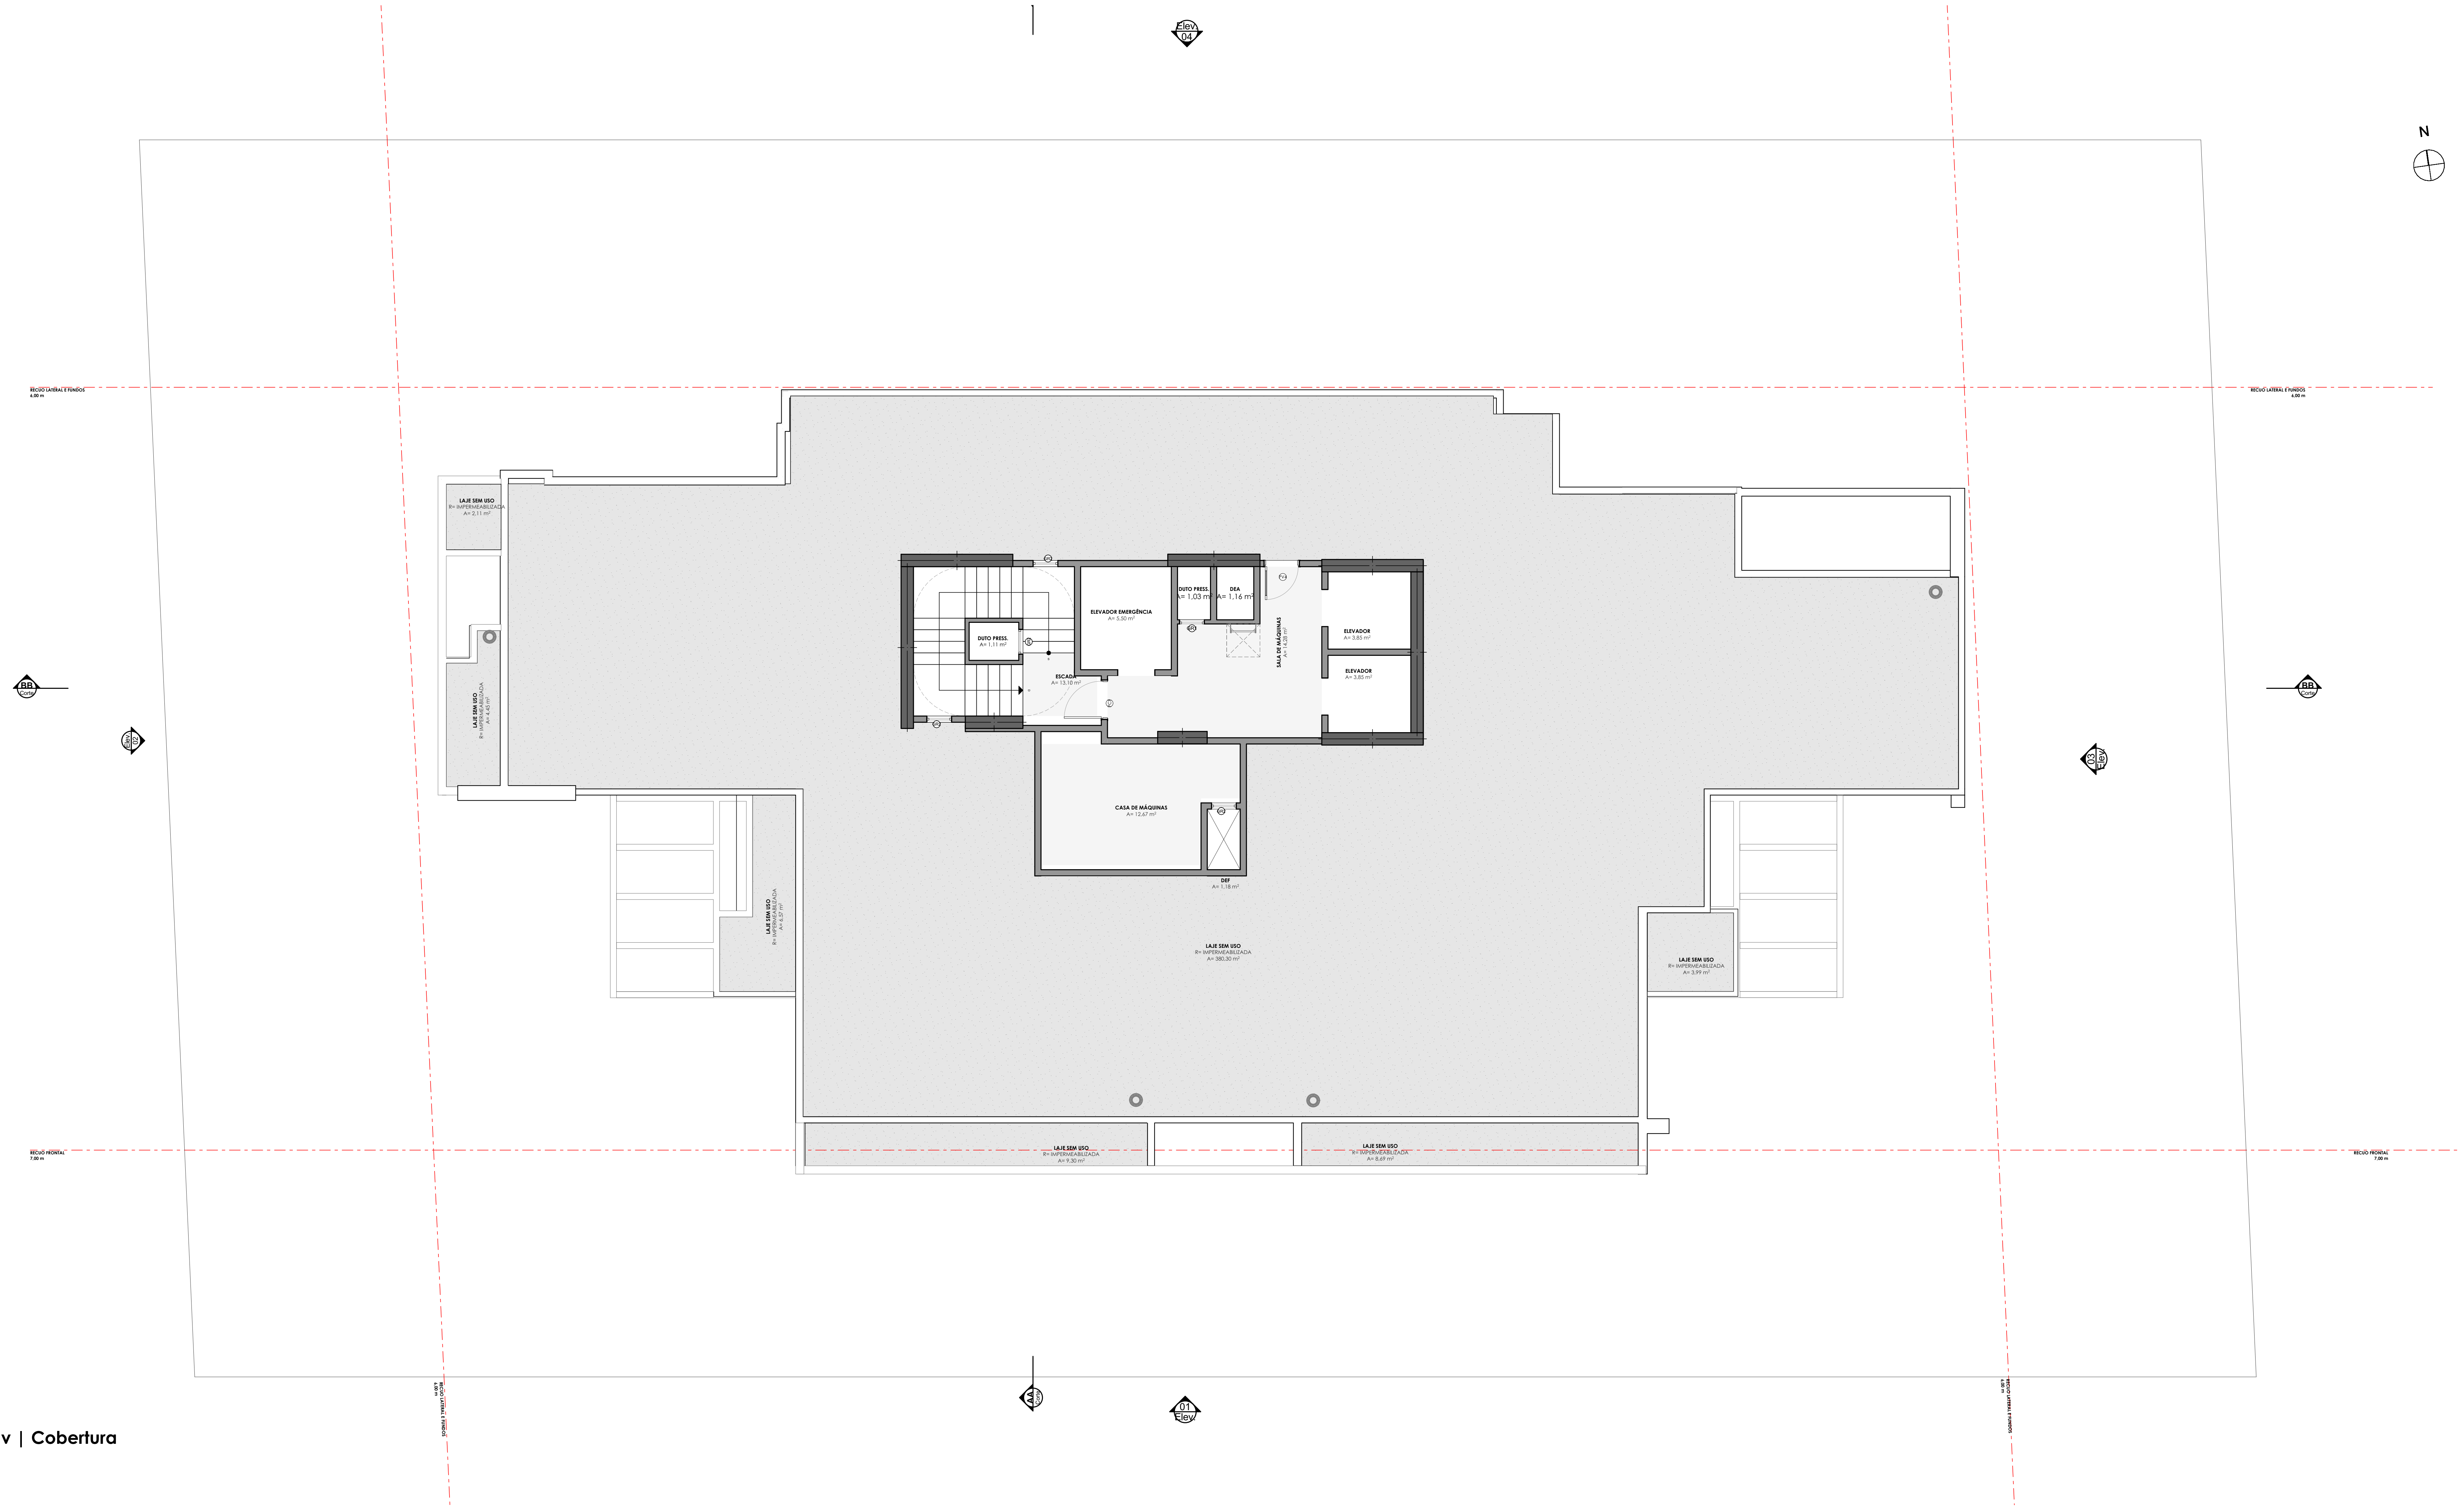
N
RECUO LATERAL E FUNDOS
6,00 m
RECUO FRONTAL
7,00 m
LAJE SEM USO
R= IMPERMEABILIZADA
A= 2,11 m²
LAJE SEM USO
R= IMPERMEABILIZADA
A= 4,45 m²
LAJE SEM USO
R= IMPERMEABILIZADA
A= 6,57 m²
DUTO PRESS.
A= 1,11 m²
ESCADA
A= 13,10 m²
ELEVADOR EMERGÊNCIA
A= 5,50 m²
DUTO PRESS.
A= 1,03 m²
DEA
A= 1,16 m²
SALA DE MÁQUINAS
A= 14,28 m²
ELEVADOR
A= 3,85 m²
ELEVADOR
A= 3,85 m²
GR1
GR2
PV4
PCF
CASA DE MÁQUINAS
A= 12,67 m²
DEF
A= 1,18 m²
LAJE SEM USO
R= IMPERMEABILIZADA
A= 380,30 m²
LAJE SEM USO
R= IMPERMEABILIZADA
A= 3,99 m²
LAJE SEM USO
R= IMPERMEABILIZADA
A= 9,30 m²
LAJE SEM USO
R= IMPERMEABILIZADA
A= 8,69 m²

23° Pav | Cobertura
1:100

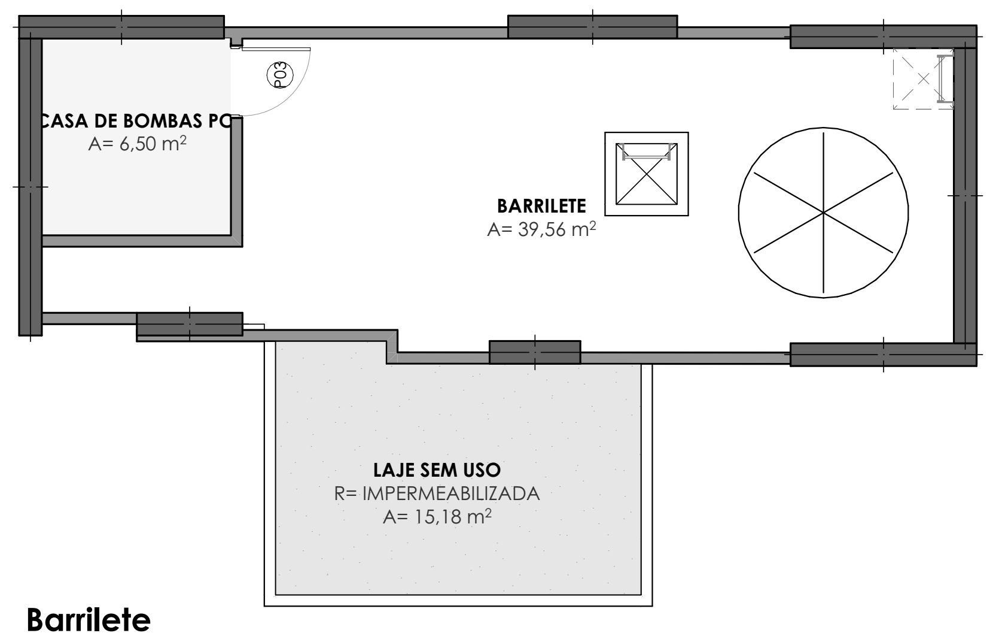
CASA DE BOMBAS PC
A= 6,50 m²
P03
BARRILETE
A= 39,56 m²
LAJE SEM USO
R= IMPERMEABILIZADA
A= 15,18 m²

Barrilete
1:100

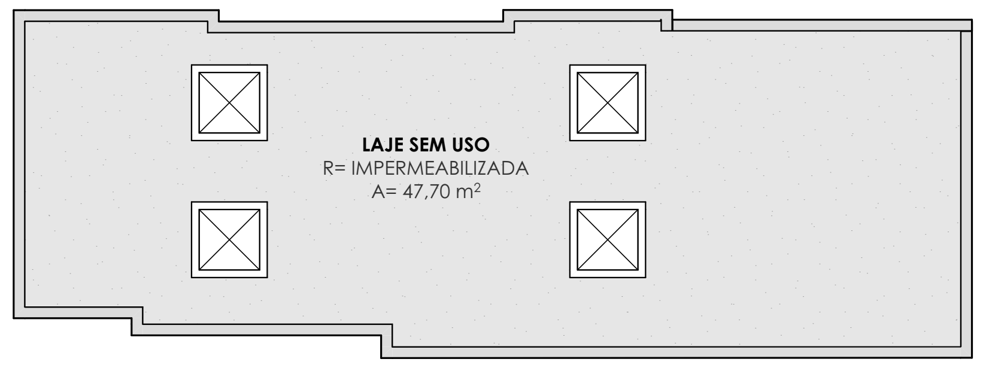
LAJE SEM USO
R= IMPERMEABILIZADA
A= 47,70 m²

Tampa - Reservatório
1:100

ESQ 11 ESQUADRIAS COBERTURA E BARRILETE

NOME	DIMENSÕES	PEITORIL	TIPO	FOLHA	MATERIAL VISTA	COR	MATERIAL FECHAMENTO	COR FECHAMENTO	QTD
Janela									
GR1	0,600×1,200	1,20	Fixo	01	Alumínio	Chumbo	Veneziana	Chumbo	1
GR2	0,600×1,200	0,20	Fixo		Alumínio				1
GR2	0,600×1,200	1,60	Fixo		Alumínio				1
GR2	0,600×1,200	1,80	Fixo		Alumínio				2
Porta									
PCF	0,900×2,100	0,00	Tipo P90	01	Aço Galvanizado	Branco	Aço Galvanizado	Branco	1
PV4	0,800×2,100	0,00	Abrir Simples		Madeira				1

Projeto Pré-executivo

RODRIGO KIRCK ARQUITETURA
Av. Coronel Marcos Konder nº805, Sala 1108, Centro, Itajaí/Santa Catarina CEP 88301-470
Contato | (47) 3349-7161 | contato@rodrigokirck.com.br

DOM | RAYMUNDI BRAVA

ASSUNTO
PE | | Projeto Pré-executivo
Barrilete, Tampa - Reservatório, 23° Pav | Cobertura
552_EM_Raymundi_DOM_PE_R01.pln

ARQ RESP Danilo Garcia
DESENHO Thaís Pinheiro
REVISÃO
DATA 14/08/2026

PRANCHA
10

OBRA
DOM | RAYMUNDI BRAVA

LOCAL
R. Pra. Jucilia Maria da Silva Miguel - Itajaí - - Santa Catarina

RESPONSÁVEL TÉCNICO
Danilo dos Santos Garcia
A55244-5

PROPRIETÁRIO
Raymundi Brava RB SPE LTDA
56.344.375/0001-23

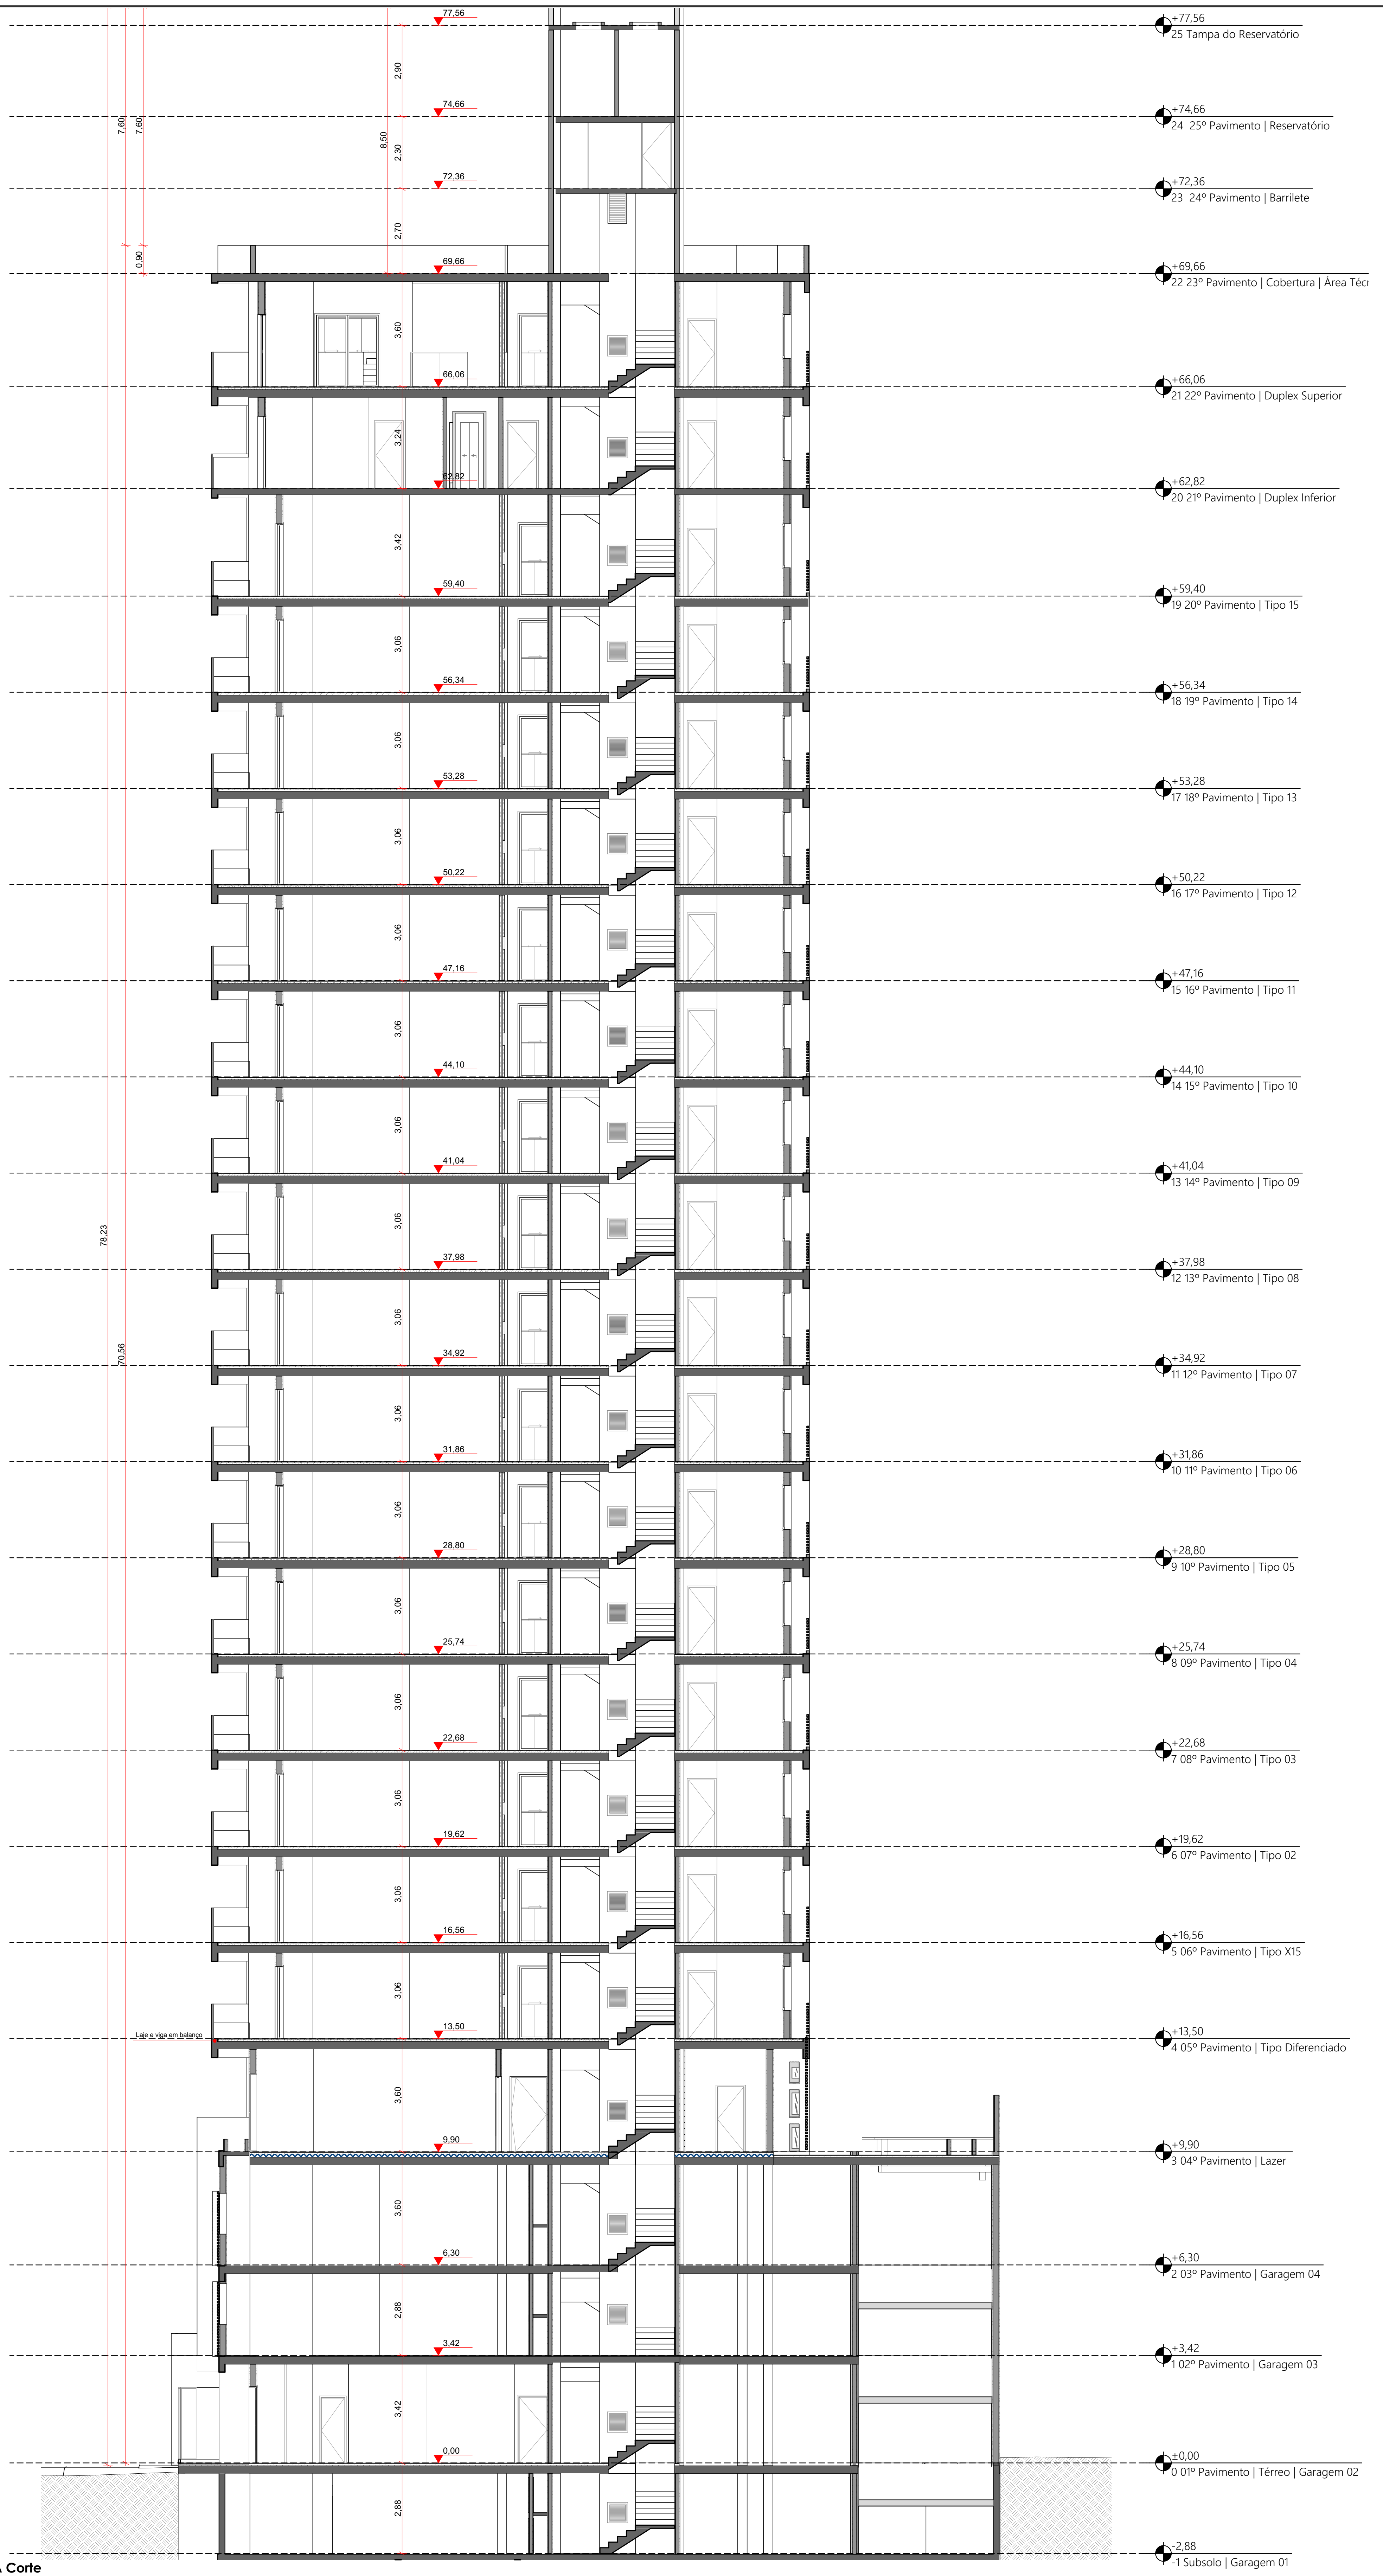
+77,56
25 Tampa do Reservatório
+74,66
24 25º Pavimento | Reservatório
+72,36
23 24º Pavimento | Barrilete
+69,66
22 23º Pavimento | Cobertura | Área Técı
+66,06
21 22º Pavimento | Duplex Superior
+62,82
20 21º Pavimento | Duplex Inferior
+59,40
19 20º Pavimento | Tipo 15
+56,34
18 19º Pavimento | Tipo 14
+53,28
17 18º Pavimento | Tipo 13
+50,22
16 17º Pavimento | Tipo 12
+47,16
15 16º Pavimento | Tipo 11
+44,10
14 15º Pavimento | Tipo 10
+41,04
13 14º Pavimento | Tipo 09
+37,98
12 13º Pavimento | Tipo 08
+34,92
11 12º Pavimento | Tipo 07
+31,86
10 11º Pavimento | Tipo 06
+28,80
9 10º Pavimento | Tipo 05
+25,74
8 09º Pavimento | Tipo 04
+22,68
7 08º Pavimento | Tipo 03
+19,62
6 07º Pavimento | Tipo 02
+16,56
5 06º Pavimento | Tipo X15
+13,50
4 05º Pavimento | Tipo Diferenciado
+9,90
3 04º Pavimento | Lazer
+6,30
2 03º Pavimento | Garagem 04
+3,42
1 02º Pavimento | Garagem 03
±0,00
0 01º Pavimento | Térreo | Garagem 02
-2,88
-1 Subsolo | Garagem 01
Laje e viga em balanço
3,06
3,60
16,56
13,50
9,90

AA Corte
1:100

Projeto Pré-executivo

RODRIGO KIRCK ARQUITETURA
Av. Coronel Marcos Konder nº805, Sala 1108, Centro, Itajaí/Santa Catarina CEP 88301-470
Contato | (47) 3349-7161 | contato@rodrigokirck.com.br

DOM | RAYMUNDI BRAVA

ASSUNTO
PE | | Projeto Pré-executivo
AA Corte
552_EM_Raymundi_DOM_PE_R01.pln

ARQ RESP Danilo Garcia
DESENHO Thaís Pinheiro

REVISÃO
DATA 14/08/2026

PRANCHA
11

OBRA
DOM | RAYMUNDI BRAVA

LOCAL
R. Pra. Jucilia Maria da Silva Miguel - Itajaí - -
Santa Catarina

RESPONSÁVEL TÉCNICO
Danilo dos Santos Garcia
A55244-5

PROPRIETÁRIO
Raymundi Brava RB SPE LTDA
56.344.375/0001-23

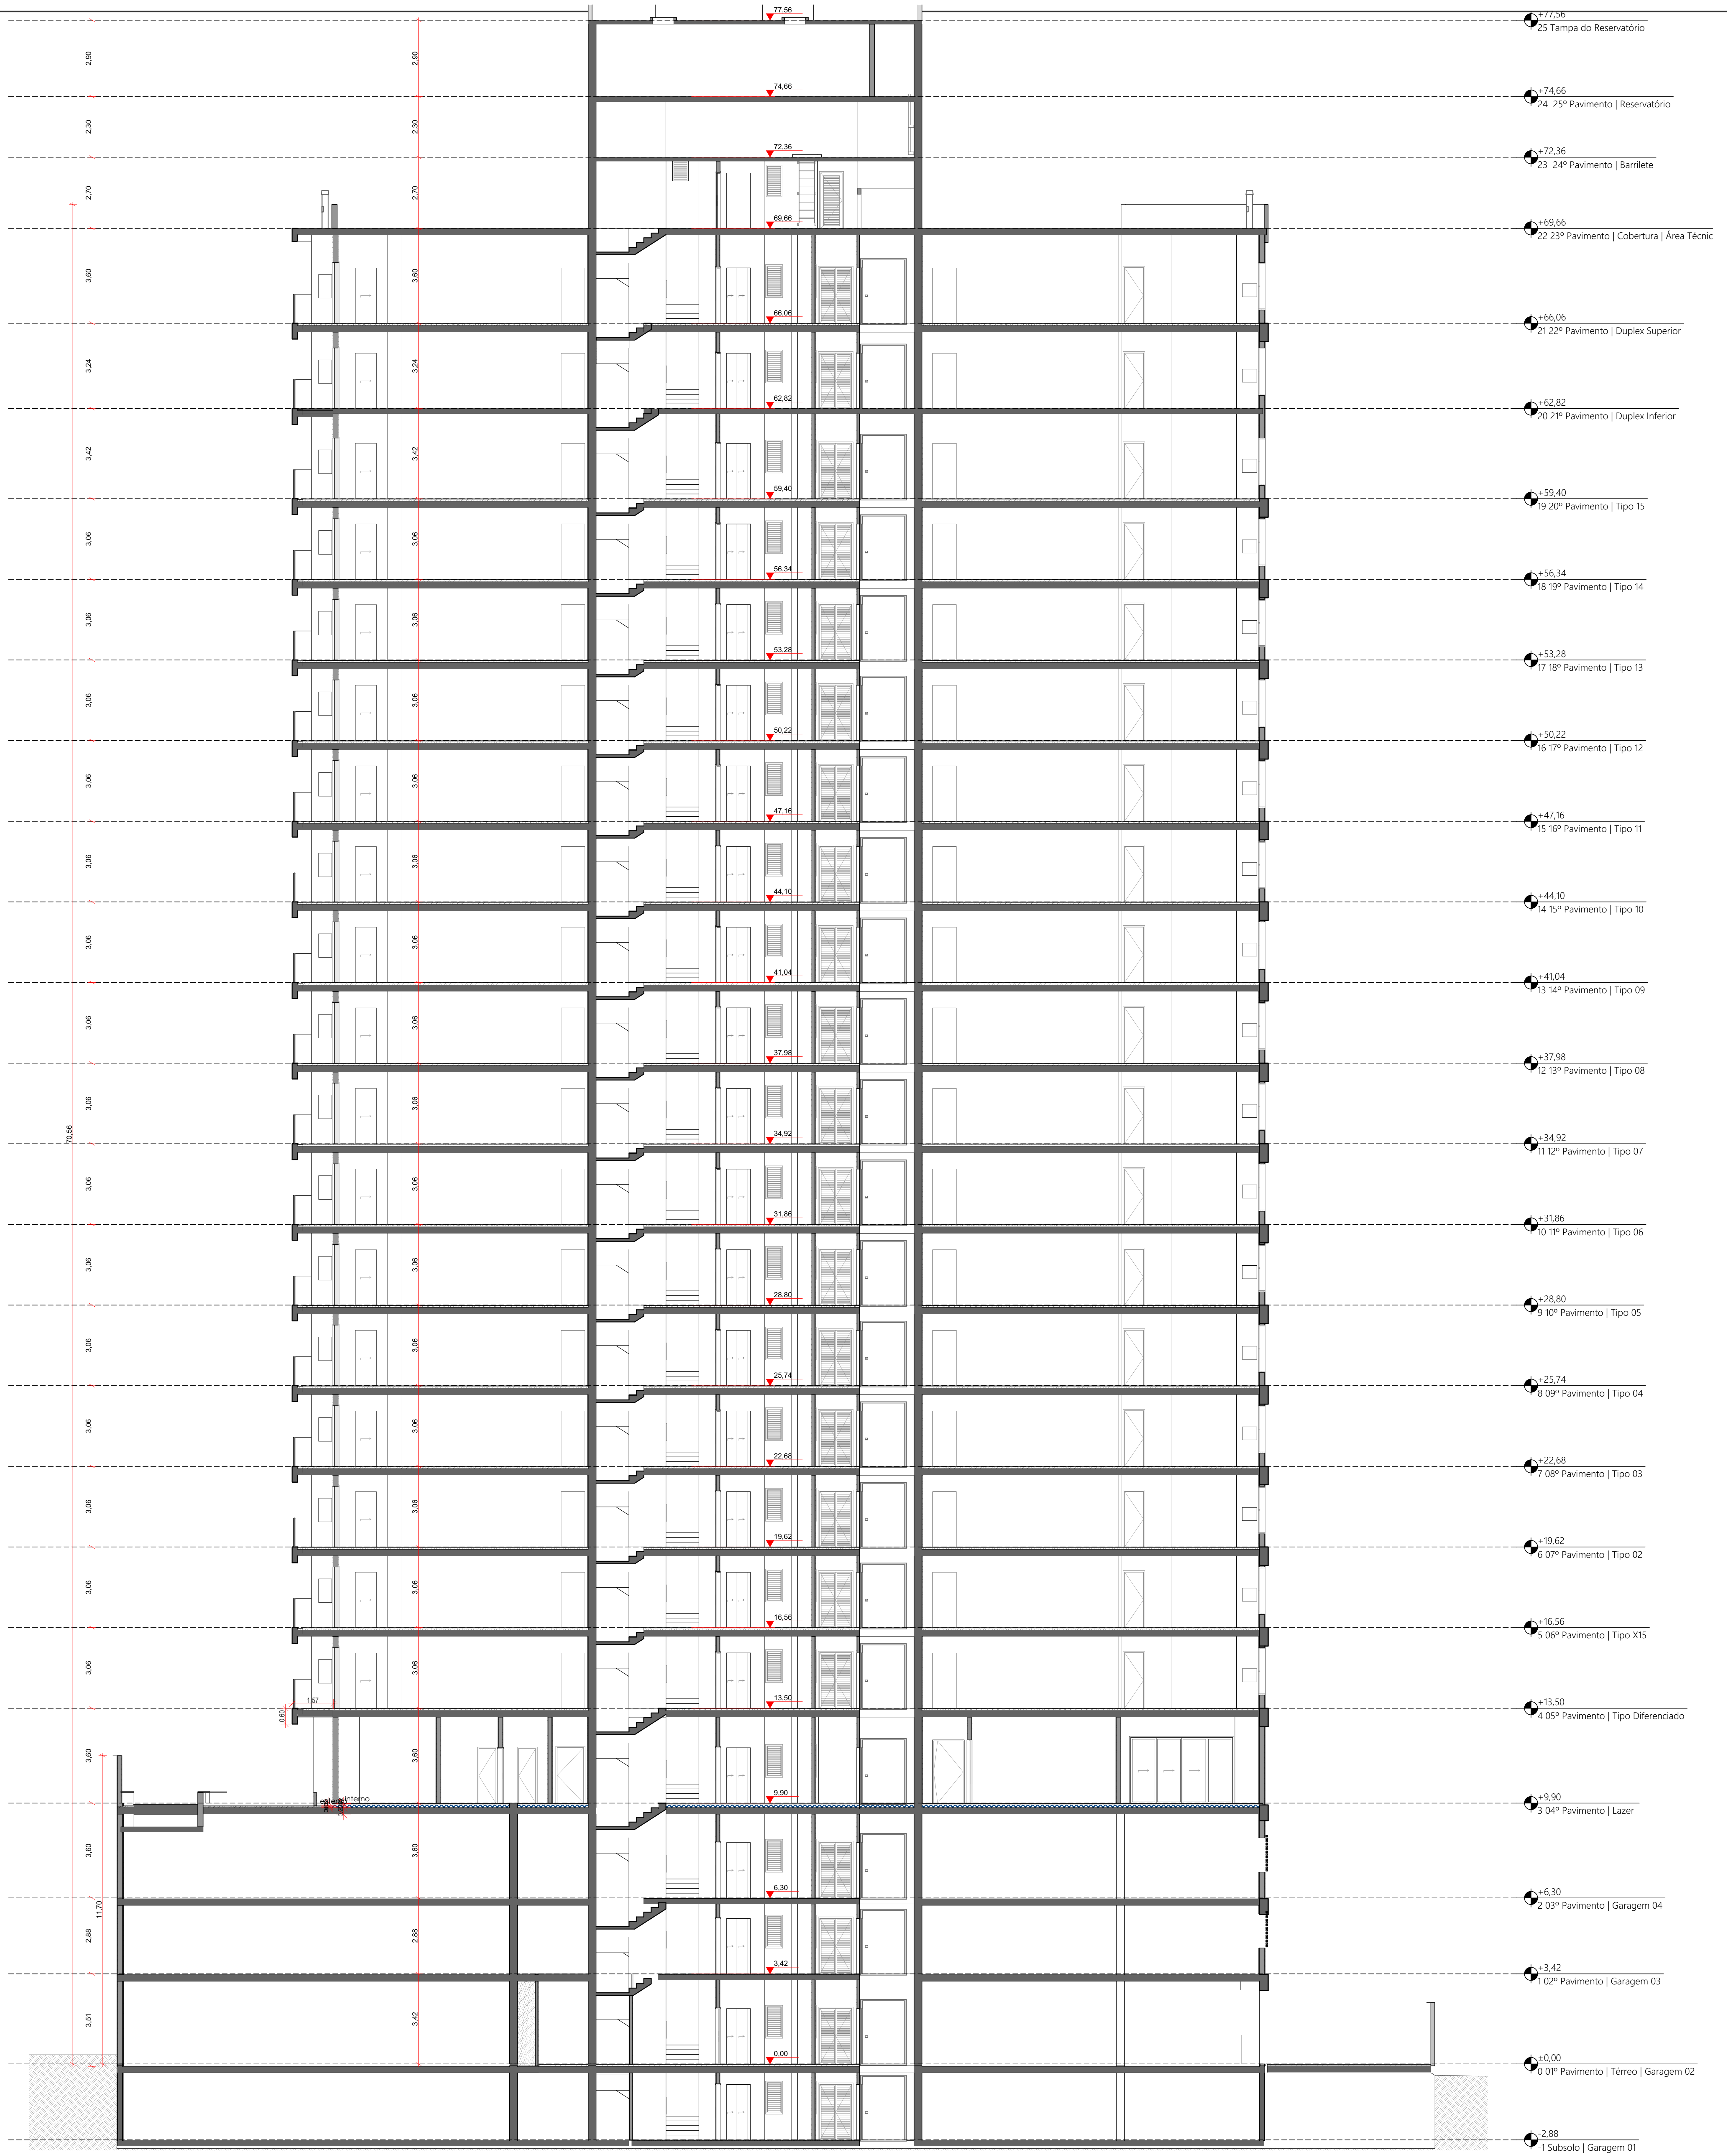
+77,56
25 Tampa do Reservatório
+74,66
24 25º Pavimento | Reservatório
+72,36
23 24º Pavimento | Barrilete
+69,66
22 23º Pavimento | Cobertura | Área Técnic
+66,06
21 22º Pavimento | Duplex Superior
+62,82
20 21º Pavimento | Duplex Inferior
+59,40
19 20º Pavimento | Tipo 15
+56,34
18 19º Pavimento | Tipo 14
+53,28
17 18º Pavimento | Tipo 13
+50,22
16 17º Pavimento | Tipo 12
+47,16
15 16º Pavimento | Tipo 11
+44,10
14 15º Pavimento | Tipo 10
+41,04
13 14º Pavimento | Tipo 09
+37,98
12 13º Pavimento | Tipo 08
+34,92
11 12º Pavimento | Tipo 07
+31,86
10 11º Pavimento | Tipo 06
+28,80
9 10º Pavimento | Tipo 05
+25,74
8 09º Pavimento | Tipo 04
+22,68
7 08º Pavimento | Tipo 03
+19,62
6 07º Pavimento | Tipo 02
+16,56
5 06º Pavimento | Tipo X15
+13,50
4 05º Pavimento | Tipo Diferenciado
+9,90
3 04º Pavimento | Lazer
+6,30
2 03º Pavimento | Garagem 04
+3,42
1 02º Pavimento | Garagem 03
±0,00
0 01º Pavimento | Térreo | Garagem 02
-2,88
-1 Subsolo | Garagem 01

BB Corte
1:100

Projeto Pré-executivo

RODRIGO KIRCK ARQUITETURA

Av. Coronel Marcos Konder nº805, Sala 1108, Centro, Itajaí/Santa Catarina CEP 88301-470
Contato | (47) 3349-7161 | contato@rodrigokirck.com.br

DOM | RAYMUNDI BRAVA

ASSUNTO
PE | | Projeto Pré-executivo
BB Corte
552_EM_Raymundi_DOM_PE_R01.pln

ARQ RESP Danilo Garcia
DESENHO Thaís Pinheiro
REVISÃO
DATA 14/08/2026

PRANCHA
12

OBRA
DOM | RAYMUNDI BRAVA

LOCAL
R. Pra. Jucilia Maria da Silva Miguel - Itajaí - -
Santa Catarina

RESPONSÁVEL TÉCNICO

PROPRIETÁRIO

Danilo dos Santos Garcia
A55244-5

Raymundi Brava RB SPE LTDA
56.344.375/0001-23

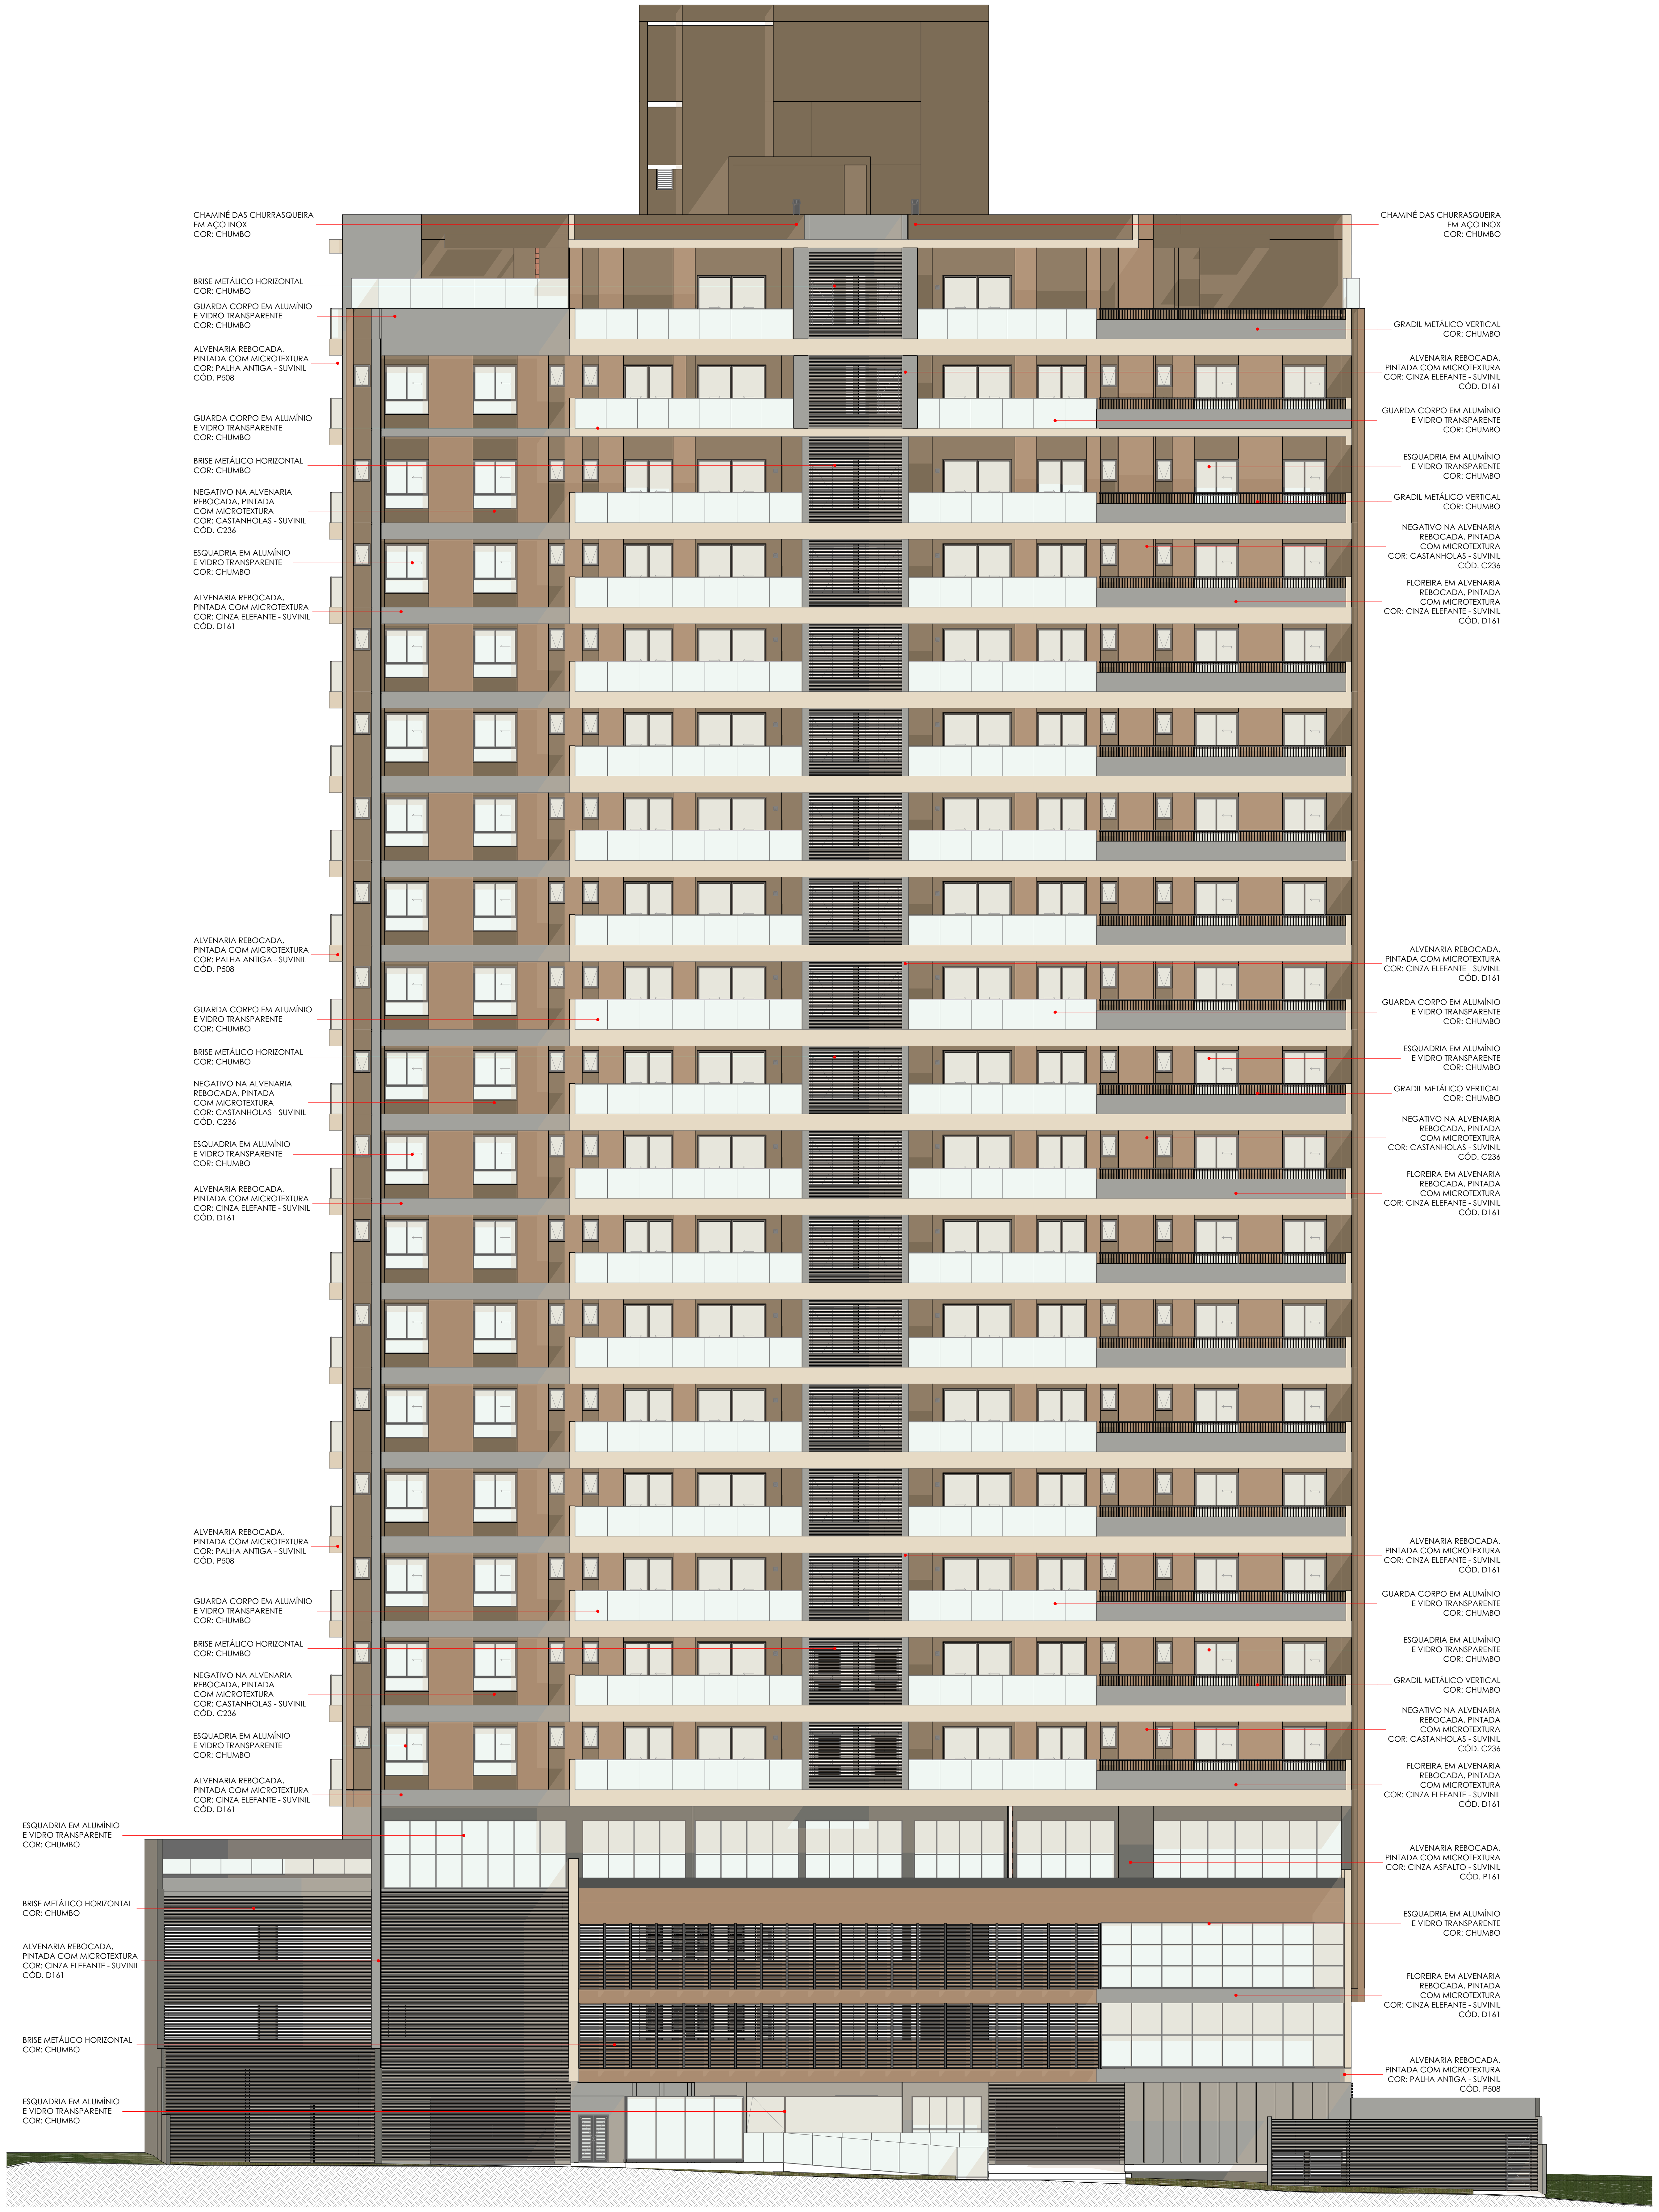
CHAMINÉ DAS CHURRASQUEIRA EM AÇO INOX COR: CHUMBO
BRISE METÁLICO HORIZONTAL COR: CHUMBO
GUARDA CORPO EM ALUMÍNIO E VIDRO TRANSPARENTE COR: CHUMBO
ALVENARIA REBOCADA, PINTADA COM MICROTEXTURA COR: PALHA ANTIGA - SUVINIL CÓD. P508
GUARDA CORPO EM ALUMÍNIO E VIDRO TRANSPARENTE COR: CHUMBO
BRISE METÁLICO HORIZONTAL COR: CHUMBO
NEGATIVO NA ALVENARIA REBOCADA, PINTADA COM MICROTEXTURA COR: CASTANHOLAS - SUVINIL CÓD. C236
ESQUADRIA EM ALUMÍNIO E VIDRO TRANSPARENTE COR: CHUMBO
ALVENARIA REBOCADA, PINTADA COM MICROTEXTURA COR: CINZA ELEFANTE - SUVINIL CÓD. D161
ALVENARIA REBOCADA, PINTADA COM MICROTEXTURA COR: PALHA ANTIGA - SUVINIL CÓD. P508
GUARDA CORPO EM ALUMÍNIO E VIDRO TRANSPARENTE COR: CHUMBO
BRISE METÁLICO HORIZONTAL COR: CHUMBO
NEGATIVO NA ALVENARIA REBOCADA, PINTADA COM MICROTEXTURA COR: CASTANHOLAS - SUVINIL CÓD. C236
ESQUADRIA EM ALUMÍNIO E VIDRO TRANSPARENTE COR: CHUMBO
ALVENARIA REBOCADA, PINTADA COM MICROTEXTURA COR: CINZA ELEFANTE - SUVINIL CÓD. D161
ALVENARIA REBOCADA, PINTADA COM MICROTEXTURA COR: PALHA ANTIGA - SUVINIL CÓD. P508
GUARDA CORPO EM ALUMÍNIO E VIDRO TRANSPARENTE COR: CHUMBO
BRISE METÁLICO HORIZONTAL COR: CHUMBO
NEGATIVO NA ALVENARIA REBOCADA, PINTADA COM MICROTEXTURA COR: CASTANHOLAS - SUVINIL CÓD. C236
ESQUADRIA EM ALUMÍNIO E VIDRO TRANSPARENTE COR: CHUMBO
ALVENARIA REBOCADA, PINTADA COM MICROTEXTURA COR: CINZA ELEFANTE - SUVINIL CÓD. D161
ESQUADRIA EM ALUMÍNIO E VIDRO TRANSPARENTE COR: CHUMBO
BRISE METÁLICO HORIZONTAL COR: CHUMBO
ALVENARIA REBOCADA, PINTADA COM MICROTEXTURA COR: CINZA ELEFANTE - SUVINIL CÓD. D161
BRISE METÁLICO HORIZONTAL COR: CHUMBO
ESQUADRIA EM ALUMÍNIO E VIDRO TRANSPARENTE COR: CHUMBO
CHAMINÉ DAS CHURRASQUEIRA EM AÇO INOX COR: CHUMBO
GRADIL METÁLICO VERTICAL COR: CHUMBO
ALVENARIA REBOCADA, PINTADA COM MICROTEXTURA COR: CINZA ELEFANTE - SUVINIL CÓD. D161
GUARDA CORPO EM ALUMÍNIO E VIDRO TRANSPARENTE COR: CHUMBO
ESQUADRIA EM ALUMÍNIO E VIDRO TRANSPARENTE COR: CHUMBO
GRADIL METÁLICO VERTICAL COR: CHUMBO
NEGATIVO NA ALVENARIA REBOCADA, PINTADA COM MICROTEXTURA COR: CASTANHOLAS - SUVINIL CÓD. C236
FLOREIRA EM ALVENARIA REBOCADA, PINTADA COM MICROTEXTURA COR: CINZA ELEFANTE - SUVINIL CÓD. D161
ALVENARIA REBOCADA, PINTADA COM MICROTEXTURA COR: CINZA ELEFANTE - SUVINIL CÓD. D161
GUARDA CORPO EM ALUMÍNIO E VIDRO TRANSPARENTE COR: CHUMBO
ESQUADRIA EM ALUMÍNIO E VIDRO TRANSPARENTE COR: CHUMBO
GRADIL METÁLICO VERTICAL COR: CHUMBO
NEGATIVO NA ALVENARIA REBOCADA, PINTADA COM MICROTEXTURA COR: CASTANHOLAS - SUVINIL CÓD. C236
FLOREIRA EM ALVENARIA REBOCADA, PINTADA COM MICROTEXTURA COR: CINZA ELEFANTE - SUVINIL CÓD. D161
ALVENARIA REBOCADA, PINTADA COM MICROTEXTURA COR: CINZA ELEFANTE - SUVINIL CÓD. D161
GUARDA CORPO EM ALUMÍNIO E VIDRO TRANSPARENTE COR: CHUMBO
ESQUADRIA EM ALUMÍNIO E VIDRO TRANSPARENTE COR: CHUMBO
GRADIL METÁLICO VERTICAL COR: CHUMBO
NEGATIVO NA ALVENARIA REBOCADA, PINTADA COM MICROTEXTURA COR: CASTANHOLAS - SUVINIL CÓD. C236
FLOREIRA EM ALVENARIA REBOCADA, PINTADA COM MICROTEXTURA COR: CINZA ELEFANTE - SUVINIL CÓD. D161
ALVENARIA REBOCADA, PINTADA COM MICROTEXTURA COR: CINZA ASFALTO - SUVINIL CÓD. P161
ESQUADRIA EM ALUMÍNIO E VIDRO TRANSPARENTE COR: CHUMBO
FLOREIRA EM ALVENARIA REBOCADA, PINTADA COM MICROTEXTURA COR: CINZA ELEFANTE - SUVINIL CÓD. D161
ALVENARIA REBOCADA, PINTADA COM MICROTEXTURA COR: PALHA ANTIGA - SUVINIL CÓD. P508

01 ELEVAÇÃO 01
1:100

Projeto Pré-executivo

RODRIGO KIRCK ARQUITETURA

Av. Coronel Marcos Konder nº805, Sala 1108, Centro, Itajaí/Santa Catarina CEP 88301-470
Contato | (47) 3349-7161 | contato@rodrigokirck.com.br

DOM | RAYMUNDI BRAVA

ASSUNTO
PE | | Projeto Pré-executivo
01 ELEVAÇÃO 01
552_EM_Raymundi_DOM_PE_R01.pln

ARQ RESP: Danilo Garcia
DESENHO: Thaís Pinheiro
REVISÃO
DATA: 14/08/2026

PRANCHA
13

OBRA
DOM | RAYMUNDI BRAVA

LOCAL
R. Pra. Jucilia Maria da Silva Miguel - Itajaí - -
Santa Catarina

RESPONSÁVEL TÉCNICO

Danilo dos Santos Garcia
A55244-5

PROPRIETÁRIO

Raymundi Brava RB SPE LTDA
56.344.375/0001-23

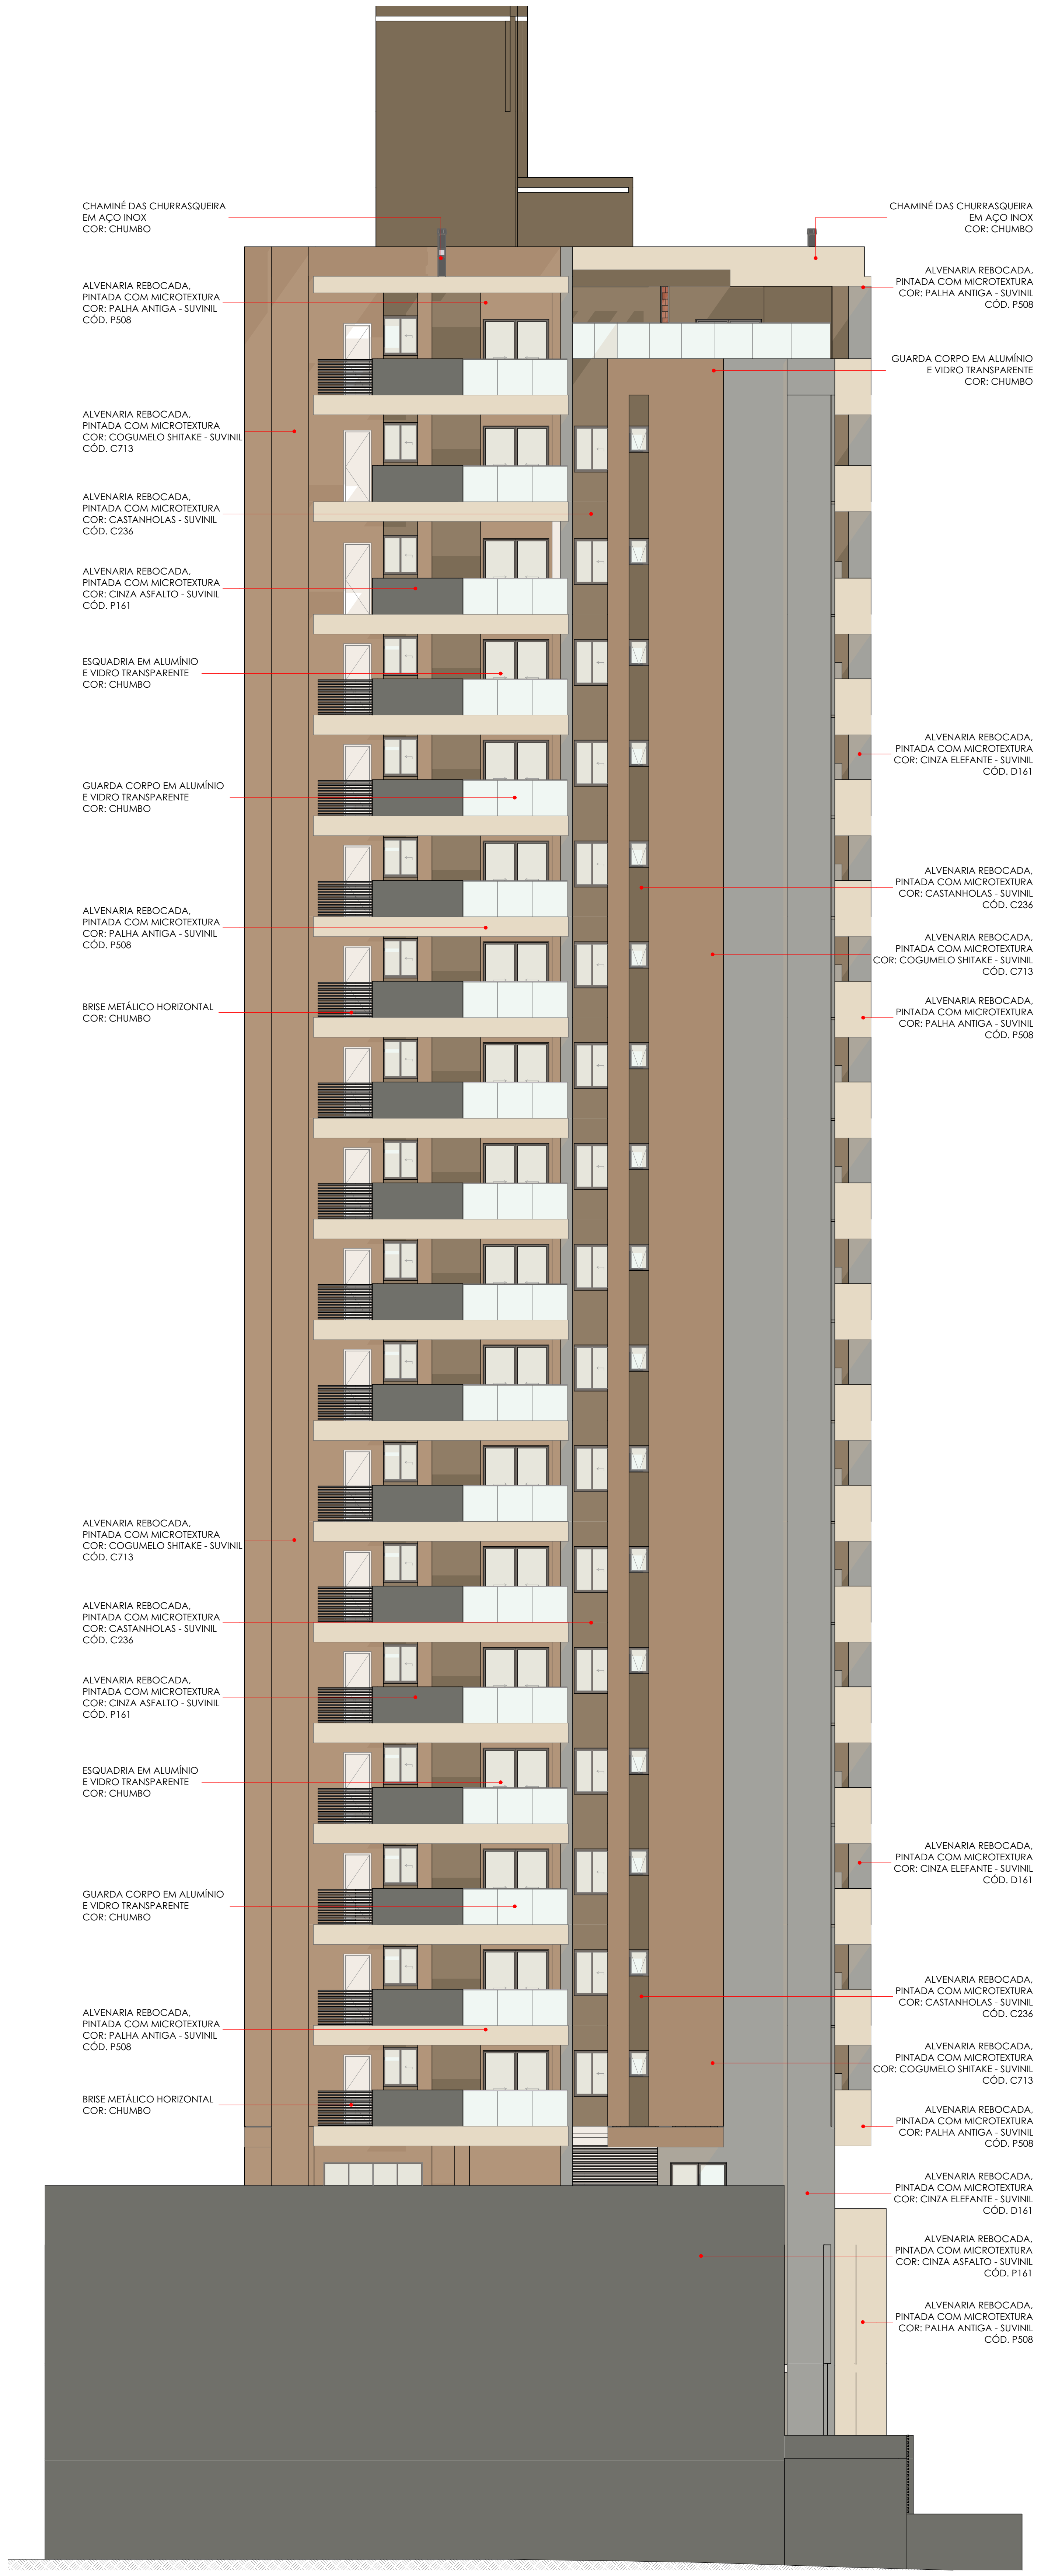
CHAMINÉ DAS CHURRASQUEIRA
EM AÇO INOX
COR: CHUMBO
ALVENARIA REBOCADA,
PINTADA COM MICROTEXTURA
COR: PALHA ANTIGA - SUVINIL
CÓD. P508
ALVENARIA REBOCADA,
PINTADA COM MICROTEXTURA
COR: COGUMELO SHITAKE - SUVINIL
CÓD. C713
ALVENARIA REBOCADA,
PINTADA COM MICROTEXTURA
COR: CASTANHOLAS - SUVINIL
CÓD. C236
ALVENARIA REBOCADA,
PINTADA COM MICROTEXTURA
COR: CINZA ASFALTO - SUVINIL
CÓD. P161
ESQUADRIA EM ALUMÍNIO
E VIDRO TRANSPARENTE
COR: CHUMBO
GUARDA CORPO EM ALUMÍNIO
E VIDRO TRANSPARENTE
COR: CHUMBO
ALVENARIA REBOCADA,
PINTADA COM MICROTEXTURA
COR: PALHA ANTIGA - SUVINIL
CÓD. P508
BRISE METÁLICO HORIZONTAL
COR: CHUMBO
ALVENARIA REBOCADA,
PINTADA COM MICROTEXTURA
COR: COGUMELO SHITAKE - SUVINIL
CÓD. C713
ALVENARIA REBOCADA,
PINTADA COM MICROTEXTURA
COR: CASTANHOLAS - SUVINIL
CÓD. C236
ALVENARIA REBOCADA,
PINTADA COM MICROTEXTURA
COR: CINZA ASFALTO - SUVINIL
CÓD. P161
ESQUADRIA EM ALUMÍNIO
E VIDRO TRANSPARENTE
COR: CHUMBO
GUARDA CORPO EM ALUMÍNIO
E VIDRO TRANSPARENTE
COR: CHUMBO
ALVENARIA REBOCADA,
PINTADA COM MICROTEXTURA
COR: PALHA ANTIGA - SUVINIL
CÓD. P508
BRISE METÁLICO HORIZONTAL
COR: CHUMBO
CHAMINÉ DAS CHURRASQUEIRA
EM AÇO INOX
COR: CHUMBO
ALVENARIA REBOCADA,
PINTADA COM MICROTEXTURA
COR: PALHA ANTIGA - SUVINIL
CÓD. P508
GUARDA CORPO EM ALUMÍNIO
E VIDRO TRANSPARENTE
COR: CHUMBO
ALVENARIA REBOCADA,
PINTADA COM MICROTEXTURA
COR: CINZA ELEFANTE - SUVINIL
CÓD. D161
ALVENARIA REBOCADA,
PINTADA COM MICROTEXTURA
COR: CASTANHOLAS - SUVINIL
CÓD. C236
ALVENARIA REBOCADA,
PINTADA COM MICROTEXTURA
COR: COGUMELO SHITAKE - SUVINIL
CÓD. C713
ALVENARIA REBOCADA,
PINTADA COM MICROTEXTURA
COR: PALHA ANTIGA - SUVINIL
CÓD. P508
ALVENARIA REBOCADA,
PINTADA COM MICROTEXTURA
COR: CINZA ELEFANTE - SUVINIL
CÓD. D161
ALVENARIA REBOCADA,
PINTADA COM MICROTEXTURA
COR: CASTANHOLAS - SUVINIL
CÓD. C236
ALVENARIA REBOCADA,
PINTADA COM MICROTEXTURA
COR: COGUMELO SHITAKE - SUVINIL
CÓD. C713
ALVENARIA REBOCADA,
PINTADA COM MICROTEXTURA
COR: PALHA ANTIGA - SUVINIL
CÓD. P508
ALVENARIA REBOCADA,
PINTADA COM MICROTEXTURA
COR: CINZA ELEFANTE - SUVINIL
CÓD. D161
ALVENARIA REBOCADA,
PINTADA COM MICROTEXTURA
COR: CINZA ASFALTO - SUVINIL
CÓD. P161
ALVENARIA REBOCADA,
PINTADA COM MICROTEXTURA
COR: PALHA ANTIGA - SUVINIL
CÓD. P508

02 ELEVAÇÃO 02
1:100

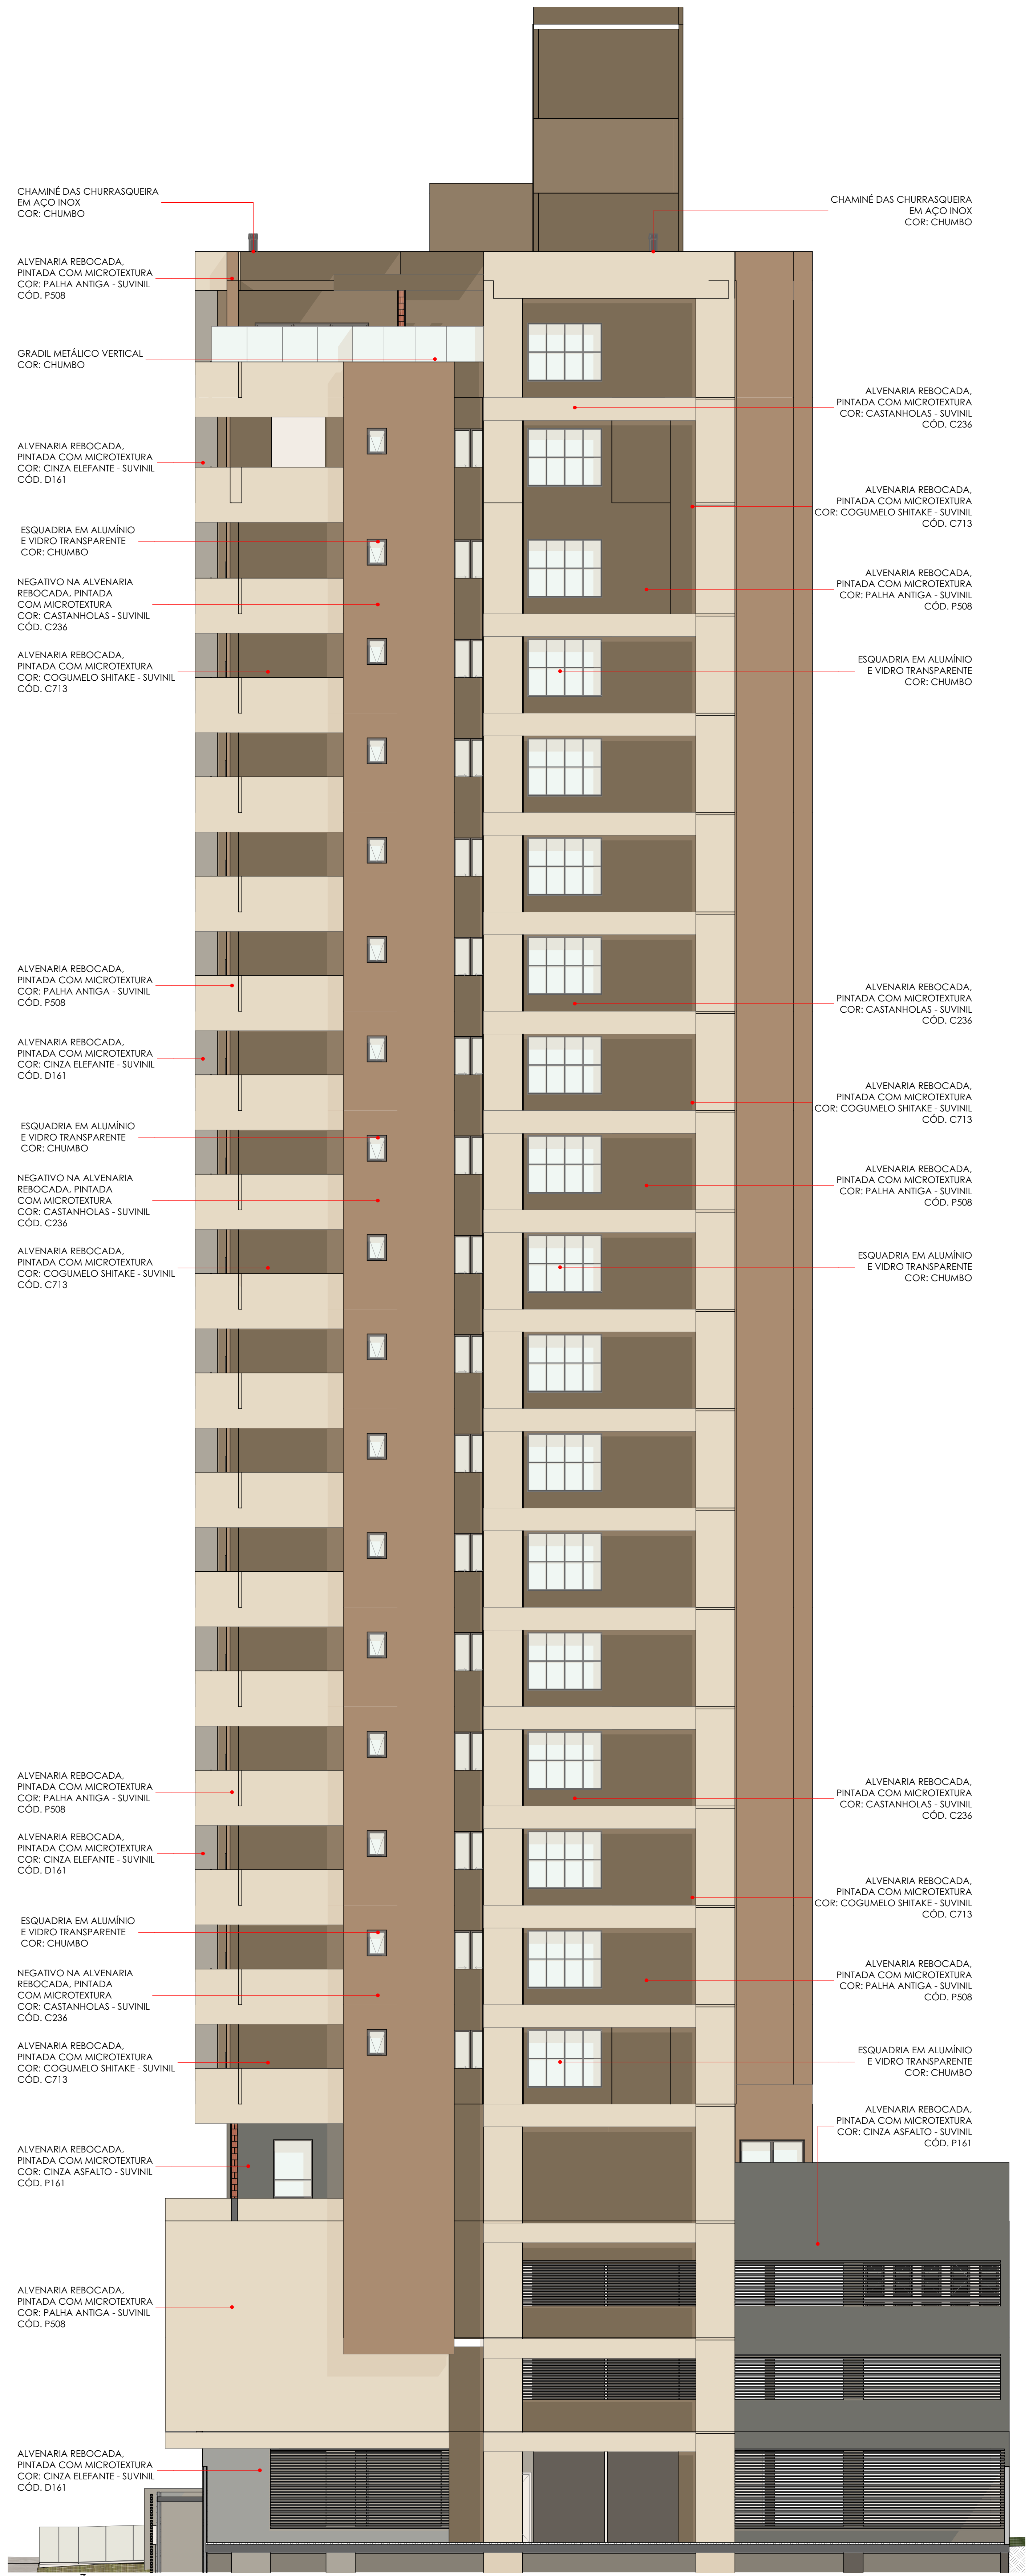
CHAMINÉ DAS CHURRASQUEIRA
EM AÇO INOX
COR: CHUMBO
ALVENARIA REBOCADA,
PINTADA COM MICROTEXTURA
COR: PALHA ANTIGA - SUVINIL
CÓD. P508
GRADIL METÁLICO VERTICAL
COR: CHUMBO
ALVENARIA REBOCADA,
PINTADA COM MICROTEXTURA
COR: CINZA ELEFANTE - SUVINIL
CÓD. D161
ESQUADRIA EM ALUMÍNIO
E VIDRO TRANSPARENTE
COR: CHUMBO
NEGATIVO NA ALVENARIA
REBOCADA, PINTADA
COM MICROTEXTURA
COR: CASTANHOLAS - SUVINIL
CÓD. C236
ALVENARIA REBOCADA,
PINTADA COM MICROTEXTURA
COR: COGUMELO SHITAKE - SUVINIL
CÓD. C713
ALVENARIA REBOCADA,
PINTADA COM MICROTEXTURA
COR: PALHA ANTIGA - SUVINIL
CÓD. P508
ALVENARIA REBOCADA,
PINTADA COM MICROTEXTURA
COR: CINZA ELEFANTE - SUVINIL
CÓD. D161
ESQUADRIA EM ALUMÍNIO
E VIDRO TRANSPARENTE
COR: CHUMBO
NEGATIVO NA ALVENARIA
REBOCADA, PINTADA
COM MICROTEXTURA
COR: CASTANHOLAS - SUVINIL
CÓD. C236
ALVENARIA REBOCADA,
PINTADA COM MICROTEXTURA
COR: COGUMELO SHITAKE - SUVINIL
CÓD. C713
ALVENARIA REBOCADA,
PINTADA COM MICROTEXTURA
COR: PALHA ANTIGA - SUVINIL
CÓD. P508
ALVENARIA REBOCADA,
PINTADA COM MICROTEXTURA
COR: CINZA ELEFANTE - SUVINIL
CÓD. D161
ESQUADRIA EM ALUMÍNIO
E VIDRO TRANSPARENTE
COR: CHUMBO
NEGATIVO NA ALVENARIA
REBOCADA, PINTADA
COM MICROTEXTURA
COR: CASTANHOLAS - SUVINIL
CÓD. C236
ALVENARIA REBOCADA,
PINTADA COM MICROTEXTURA
COR: COGUMELO SHITAKE - SUVINIL
CÓD. C713
ALVENARIA REBOCADA,
PINTADA COM MICROTEXTURA
COR: CINZA ASFALTO - SUVINIL
CÓD. P161
ALVENARIA REBOCADA,
PINTADA COM MICROTEXTURA
COR: PALHA ANTIGA - SUVINIL
CÓD. P508
ALVENARIA REBOCADA,
PINTADA COM MICROTEXTURA
COR: CINZA ELEFANTE - SUVINIL
CÓD. D161
CHAMINÉ DAS CHURRASQUEIRA
EM AÇO INOX
COR: CHUMBO
ALVENARIA REBOCADA,
PINTADA COM MICROTEXTURA
COR: CASTANHOLAS - SUVINIL
CÓD. C236
ALVENARIA REBOCADA,
PINTADA COM MICROTEXTURA
COR: COGUMELO SHITAKE - SUVINIL
CÓD. C713
ALVENARIA REBOCADA,
PINTADA COM MICROTEXTURA
COR: PALHA ANTIGA - SUVINIL
CÓD. P508
ESQUADRIA EM ALUMÍNIO
E VIDRO TRANSPARENTE
COR: CHUMBO
ALVENARIA REBOCADA,
PINTADA COM MICROTEXTURA
COR: CASTANHOLAS - SUVINIL
CÓD. C236
ALVENARIA REBOCADA,
PINTADA COM MICROTEXTURA
COR: COGUMELO SHITAKE - SUVINIL
CÓD. C713
ALVENARIA REBOCADA,
PINTADA COM MICROTEXTURA
COR: PALHA ANTIGA - SUVINIL
CÓD. P508
ESQUADRIA EM ALUMÍNIO
E VIDRO TRANSPARENTE
COR: CHUMBO
ALVENARIA REBOCADA,
PINTADA COM MICROTEXTURA
COR: CASTANHOLAS - SUVINIL
CÓD. C236
ALVENARIA REBOCADA,
PINTADA COM MICROTEXTURA
COR: COGUMELO SHITAKE - SUVINIL
CÓD. C713
ALVENARIA REBOCADA,
PINTADA COM MICROTEXTURA
COR: PALHA ANTIGA - SUVINIL
CÓD. P508
ESQUADRIA EM ALUMÍNIO
E VIDRO TRANSPARENTE
COR: CHUMBO
ALVENARIA REBOCADA,
PINTADA COM MICROTEXTURA
COR: CINZA ASFALTO - SUVINIL
CÓD. P161

03 ELEVAÇÃO 01
1:100

Projeto Pré-executivo

RODRIGO KIRCK ARQUITETURA
Av. Coronel Marcos Konder nº805, Sala 1108, Centro, Itajaí/Santa Catarina CEP 88301-470
Contato | (47) 3349-7161 | contato@rodrigokirck.com.br

DOM | RAYMUNDI BRAVA

ASSUNTO
PE | | Projeto Pré-executivo
02 ELEVAÇÃO 02, 03 ELEVAÇÃO 01
552_EM_Raymundi_DOM_PE_R01.pln

ARQ RESP Danilo Garcia
DESENHO Thaís Pinheiro
REVISÃO
DATA 14/08/2026

PRANCHA
14

OBRA
DOM | RAYMUNDI BRAVA

LOCAL
R. Pra. Jucilia Maria da Silva Miguel - Itajaí - -
Santa Catarina

RESPONSÁVEL TÉCNICO

PROPRIETÁRIO

Danilo dos Santos Garcia
A55244-5

Raymundi Brava RB SPE LTDA
56.344.375/0001-23

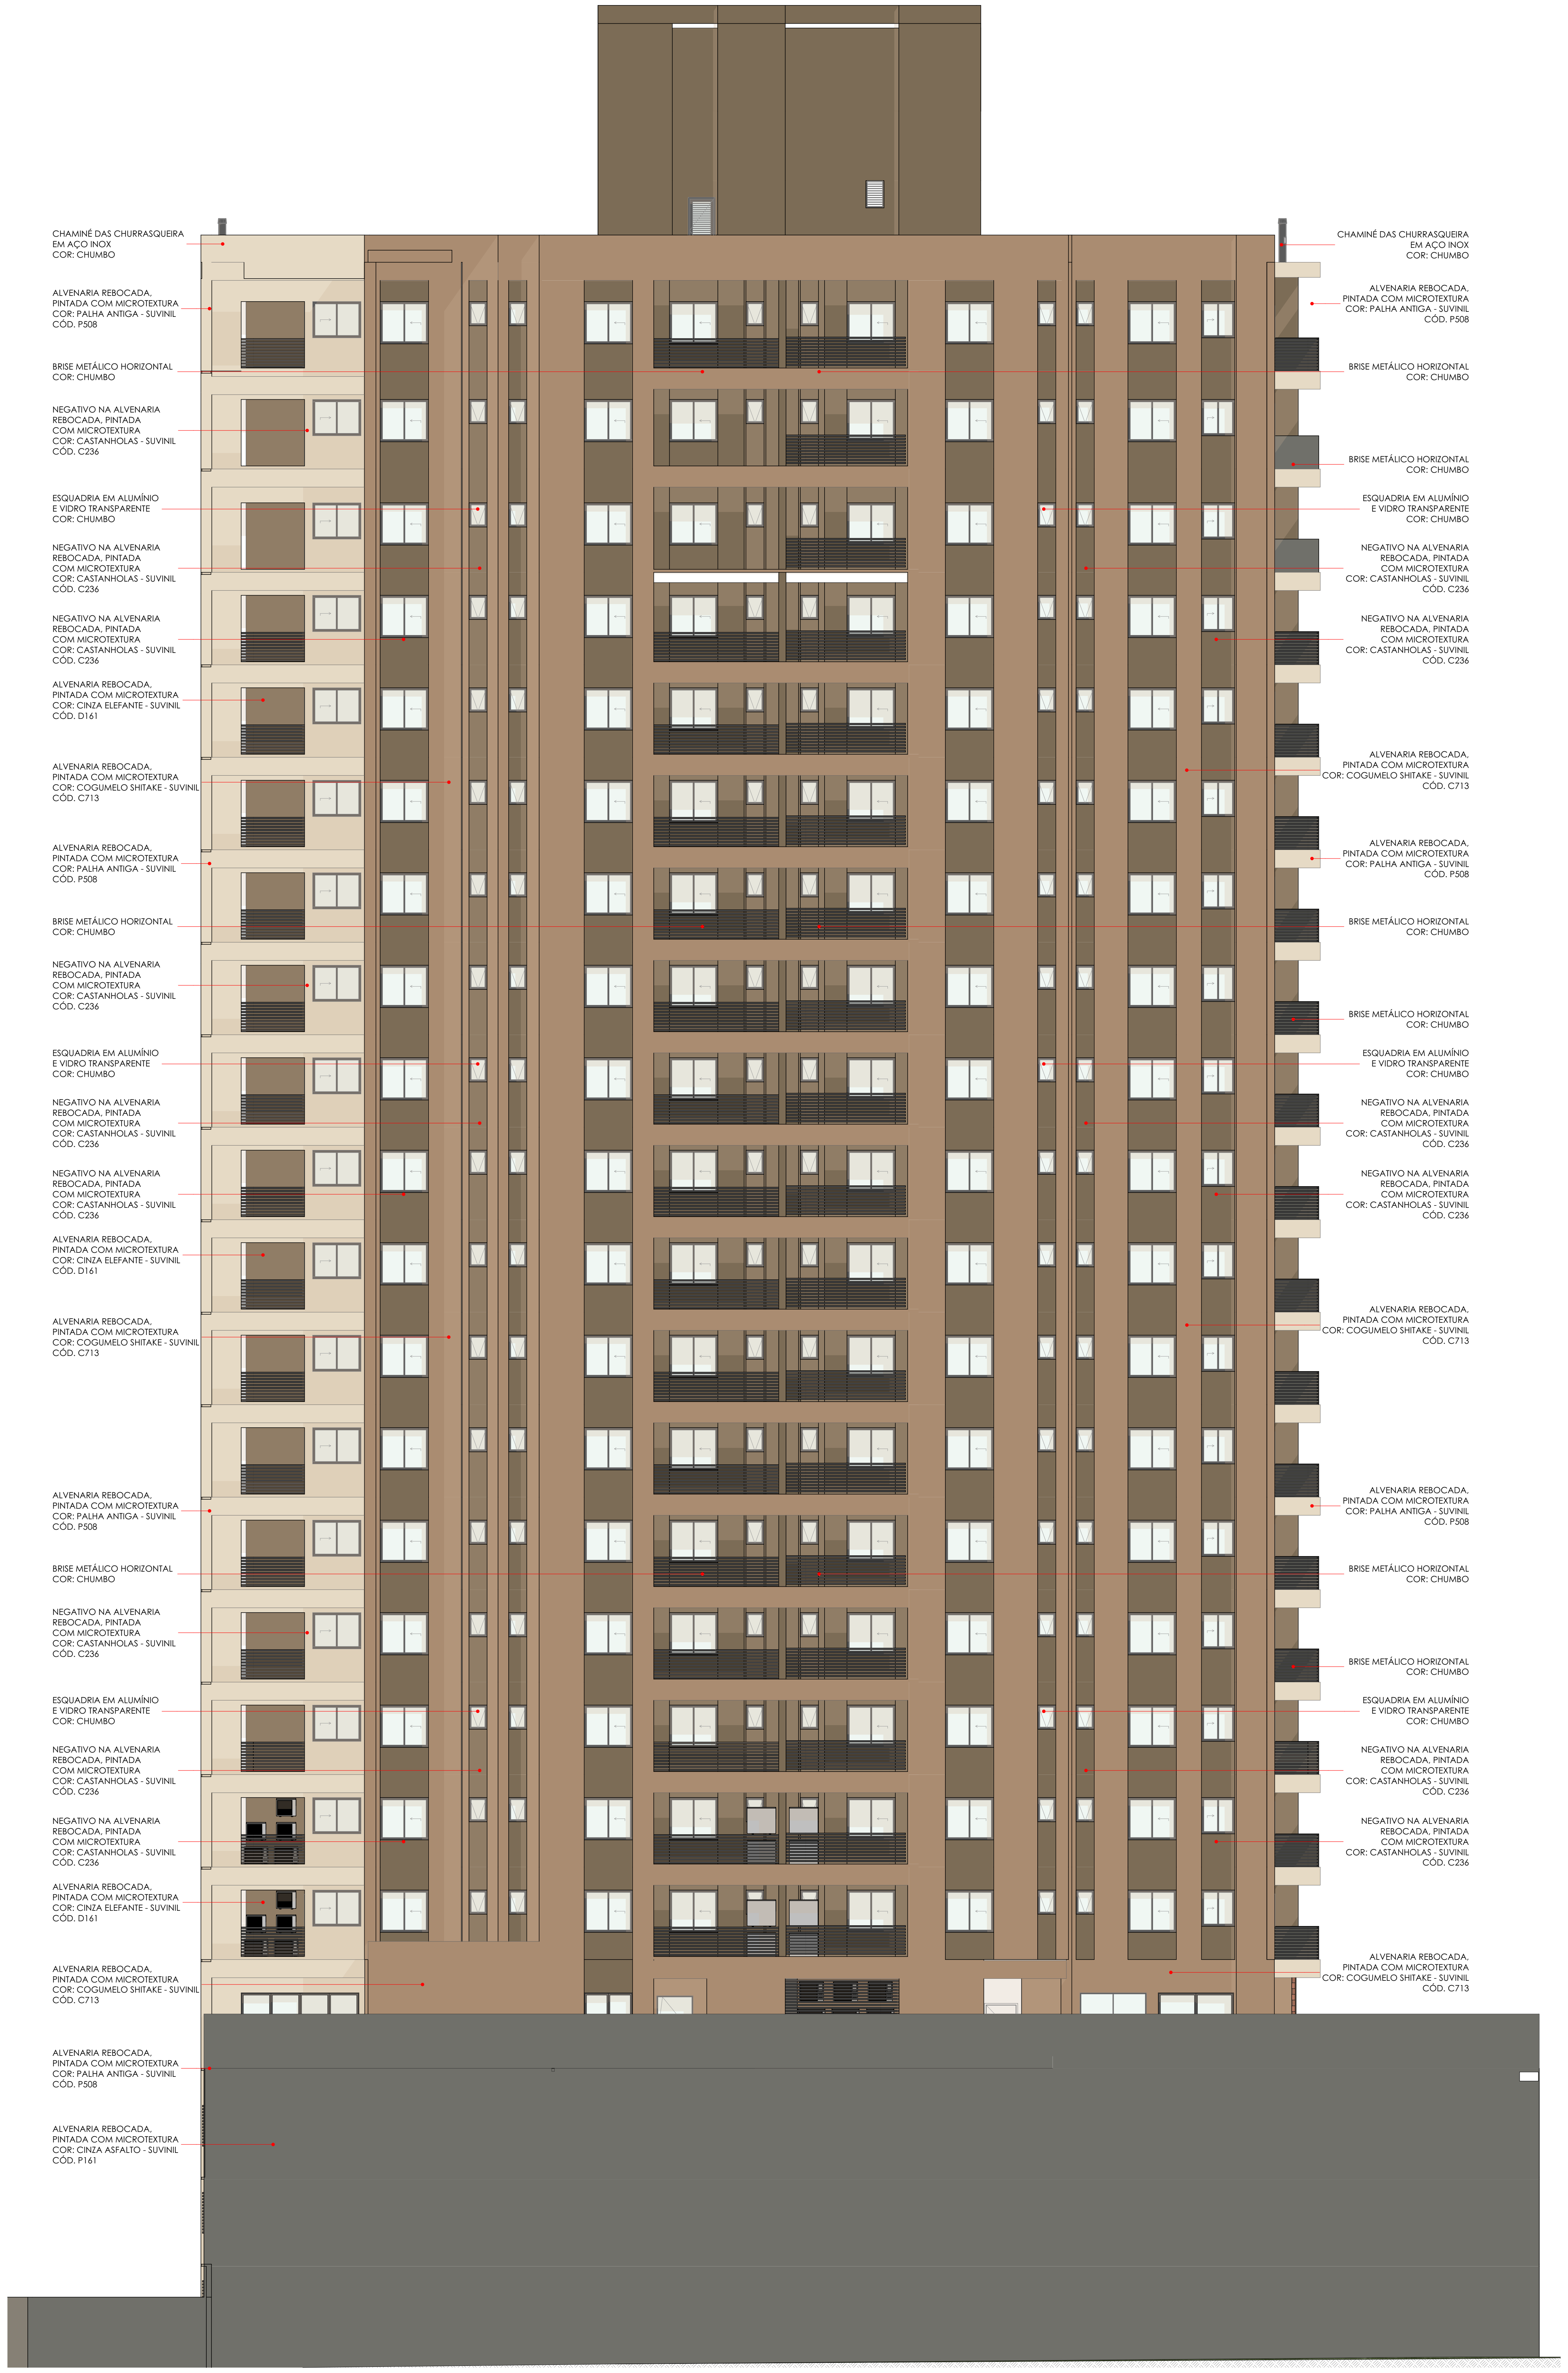
CHAMINÉ DAS CHURRASQUEIRA EM AÇO INOX COR: CHUMBO
ALVENARIA REBOCADA, PINTADA COM MICROTEXTURA COR: PALHA ANTIGA - SUVINIL CÓD. P508
BRISE METÁLICO HORIZONTAL COR: CHUMBO
NEGATIVO NA ALVENARIA REBOCADA, PINTADA COM MICROTEXTURA COR: CASTANHOLAS - SUVINIL CÓD. C236
ESQUADRIA EM ALUMÍNIO E VIDRO TRANSPARENTE COR: CHUMBO
NEGATIVO NA ALVENARIA REBOCADA, PINTADA COM MICROTEXTURA COR: CASTANHOLAS - SUVINIL CÓD. C236
NEGATIVO NA ALVENARIA REBOCADA, PINTADA COM MICROTEXTURA COR: CASTANHOLAS - SUVINIL CÓD. C236
ALVENARIA REBOCADA, PINTADA COM MICROTEXTURA COR: CINZA ELEFANTE - SUVINIL CÓD. D161
ALVENARIA REBOCADA, PINTADA COM MICROTEXTURA COR: COGUMELO SHITAKE - SUVINIL CÓD. C713
ALVENARIA REBOCADA, PINTADA COM MICROTEXTURA COR: PALHA ANTIGA - SUVINIL CÓD. P508
BRISE METÁLICO HORIZONTAL COR: CHUMBO
NEGATIVO NA ALVENARIA REBOCADA, PINTADA COM MICROTEXTURA COR: CASTANHOLAS - SUVINIL CÓD. C236
ESQUADRIA EM ALUMÍNIO E VIDRO TRANSPARENTE COR: CHUMBO
NEGATIVO NA ALVENARIA REBOCADA, PINTADA COM MICROTEXTURA COR: CASTANHOLAS - SUVINIL CÓD. C236
NEGATIVO NA ALVENARIA REBOCADA, PINTADA COM MICROTEXTURA COR: CASTANHOLAS - SUVINIL CÓD. C236
ALVENARIA REBOCADA, PINTADA COM MICROTEXTURA COR: CINZA ELEFANTE - SUVINIL CÓD. D161
ALVENARIA REBOCADA, PINTADA COM MICROTEXTURA COR: COGUMELO SHITAKE - SUVINIL CÓD. C713
ALVENARIA REBOCADA, PINTADA COM MICROTEXTURA COR: PALHA ANTIGA - SUVINIL CÓD. P508
BRISE METÁLICO HORIZONTAL COR: CHUMBO
NEGATIVO NA ALVENARIA REBOCADA, PINTADA COM MICROTEXTURA COR: CASTANHOLAS - SUVINIL CÓD. C236
ESQUADRIA EM ALUMÍNIO E VIDRO TRANSPARENTE COR: CHUMBO
NEGATIVO NA ALVENARIA REBOCADA, PINTADA COM MICROTEXTURA COR: CASTANHOLAS - SUVINIL CÓD. C236
NEGATIVO NA ALVENARIA REBOCADA, PINTADA COM MICROTEXTURA COR: CASTANHOLAS - SUVINIL CÓD. C236
ALVENARIA REBOCADA, PINTADA COM MICROTEXTURA COR: CINZA ELEFANTE - SUVINIL CÓD. D161
ALVENARIA REBOCADA, PINTADA COM MICROTEXTURA COR: COGUMELO SHITAKE - SUVINIL CÓD. C713
ALVENARIA REBOCADA, PINTADA COM MICROTEXTURA COR: PALHA ANTIGA - SUVINIL CÓD. P508
ALVENARIA REBOCADA, PINTADA COM MICROTEXTURA COR: CINZA ASFALTO - SUVINIL CÓD. P161
CHAMINÉ DAS CHURRASQUEIRA EM AÇO INOX COR: CHUMBO
ALVENARIA REBOCADA, PINTADA COM MICROTEXTURA COR: PALHA ANTIGA - SUVINIL CÓD. P508
BRISE METÁLICO HORIZONTAL COR: CHUMBO
BRISE METÁLICO HORIZONTAL COR: CHUMBO
ESQUADRIA EM ALUMÍNIO E VIDRO TRANSPARENTE COR: CHUMBO
NEGATIVO NA ALVENARIA REBOCADA, PINTADA COM MICROTEXTURA COR: CASTANHOLAS - SUVINIL CÓD. C236
NEGATIVO NA ALVENARIA REBOCADA, PINTADA COM MICROTEXTURA COR: CASTANHOLAS - SUVINIL CÓD. C236
ALVENARIA REBOCADA, PINTADA COM MICROTEXTURA COR: COGUMELO SHITAKE - SUVINIL CÓD. C713
ALVENARIA REBOCADA, PINTADA COM MICROTEXTURA COR: PALHA ANTIGA - SUVINIL CÓD. P508
BRISE METÁLICO HORIZONTAL COR: CHUMBO
BRISE METÁLICO HORIZONTAL COR: CHUMBO
ESQUADRIA EM ALUMÍNIO E VIDRO TRANSPARENTE COR: CHUMBO
NEGATIVO NA ALVENARIA REBOCADA, PINTADA COM MICROTEXTURA COR: CASTANHOLAS - SUVINIL CÓD. C236
NEGATIVO NA ALVENARIA REBOCADA, PINTADA COM MICROTEXTURA COR: CASTANHOLAS - SUVINIL CÓD. C236
ALVENARIA REBOCADA, PINTADA COM MICROTEXTURA COR: COGUMELO SHITAKE - SUVINIL CÓD. C713
ALVENARIA REBOCADA, PINTADA COM MICROTEXTURA COR: PALHA ANTIGA - SUVINIL CÓD. P508
BRISE METÁLICO HORIZONTAL COR: CHUMBO
BRISE METÁLICO HORIZONTAL COR: CHUMBO
ESQUADRIA EM ALUMÍNIO E VIDRO TRANSPARENTE COR: CHUMBO
NEGATIVO NA ALVENARIA REBOCADA, PINTADA COM MICROTEXTURA COR: CASTANHOLAS - SUVINIL CÓD. C236
NEGATIVO NA ALVENARIA REBOCADA, PINTADA COM MICROTEXTURA COR: CASTANHOLAS - SUVINIL CÓD. C236
ALVENARIA REBOCADA, PINTADA COM MICROTEXTURA COR: COGUMELO SHITAKE - SUVINIL CÓD. C713

04 ELEVAÇÃO 04
1:100

Projeto Pré-executivo

RODRIGO KIRCK ARQUITETURA
Av. Coronel Marcos Konder nº805, Sala 1108, Centro, Itajaí/Santa Catarina CEP 88301-470
Contato | (47) 3349-7161 | contato@rodrigokirck.com.br

DOM | RAYMUNDI BRAVA

ASSUNTO
PE | | Projeto Pré-executivo
04 ELEVAÇÃO 04
552_EM_Raymundi_DOM_PE_R01.pln

ARQ RESP Danilo Garcia
DESENHO Thaís Pinheiro
REVISÃO
DATA 14/08/2026

PRANCHA
15

OBRA
DOM | RAYMUNDI BRAVA

LOCAL
R. Pra. Jucilia Maria da Silva Miguel - Itajaí - -
Santa Catarina

RESPONSÁVEL TÉCNICO
Danilo dos Santos Garcia
A55244-5

PROPRIETÁRIO
Raymundi Brava RB SPE LTDA
56.344.375/0001-23